


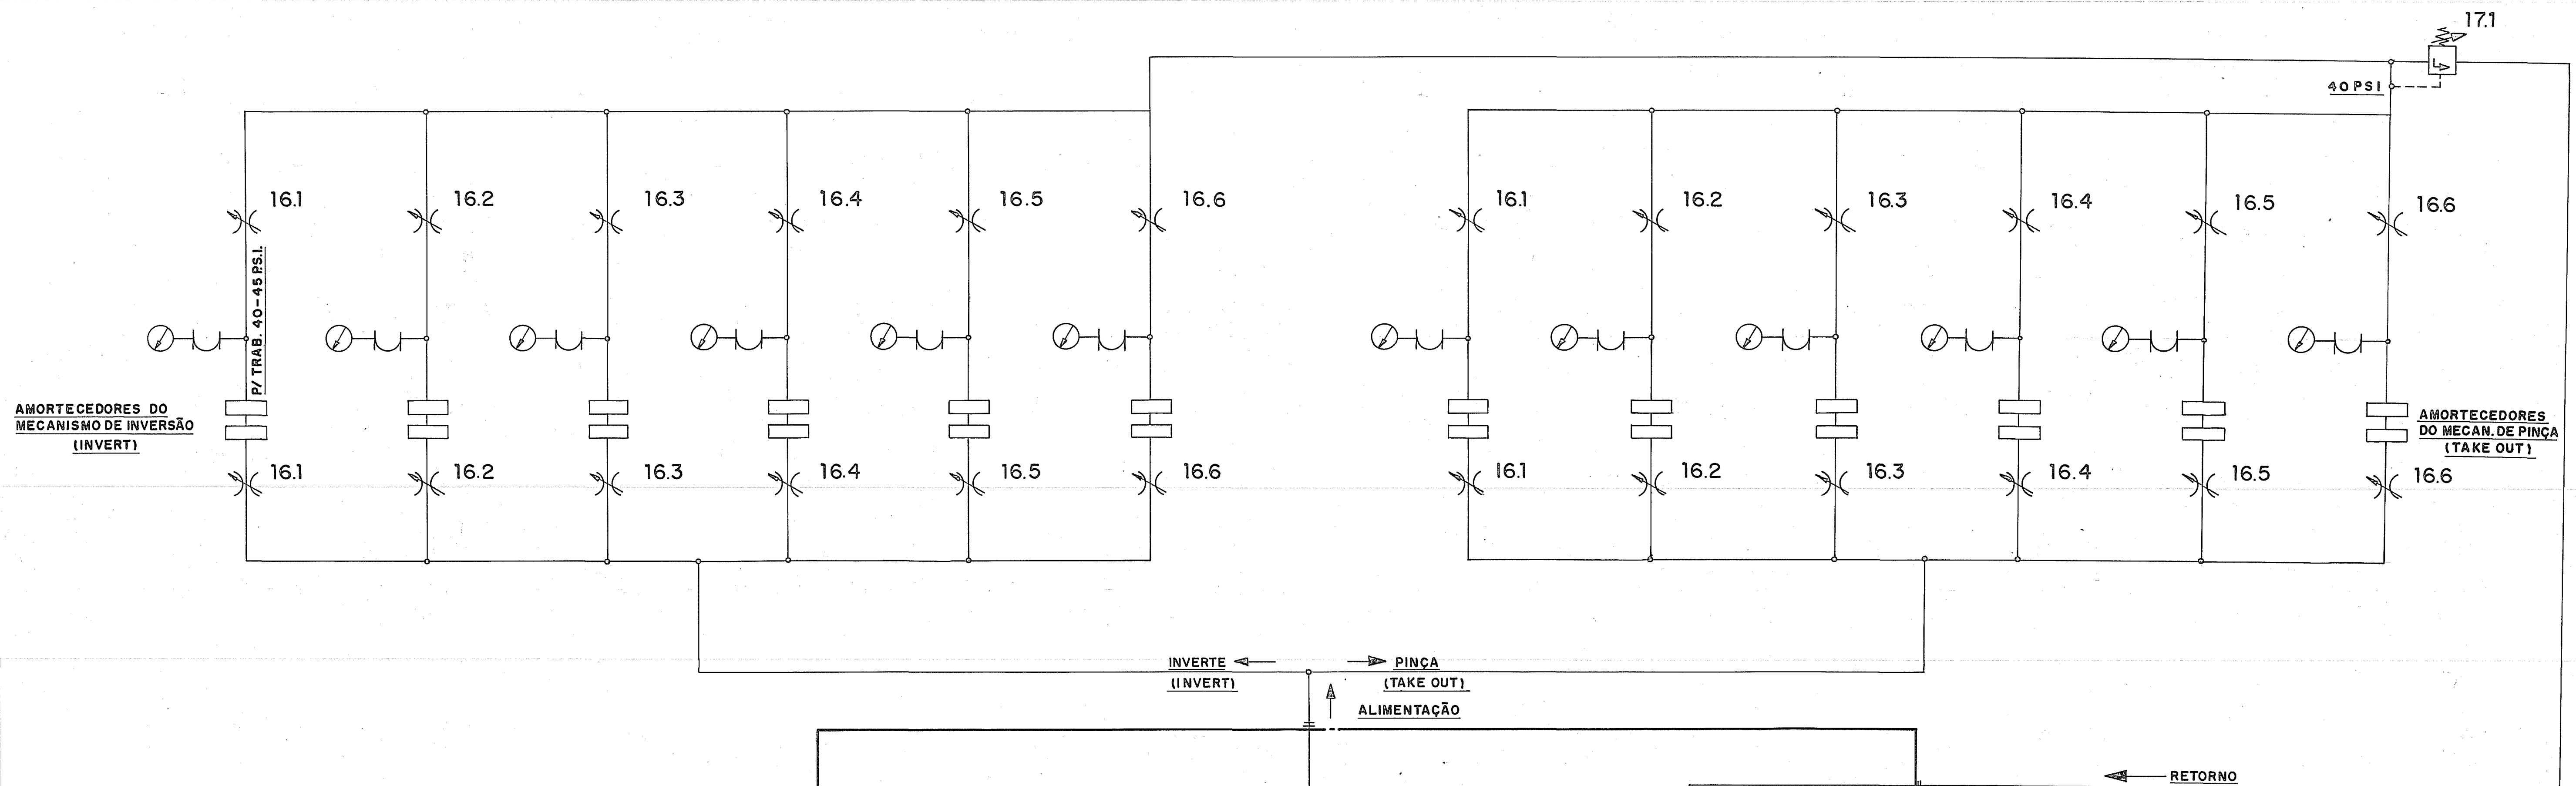


ITEM	DESCRIÇÃO	FORNECEDOR
1	RESERVATÓRIO 30 LITROS	REXROTH
2-1	BOMBA IPV-V3-40/12 RAO I MC 25-AI	REXROTH
2-2	ACOPLAMENTO - AC 28	REXROTH
2-3	FLANGE INTERMEDIÁRIA B3/B5	REXROTH
2-4	MOTOR ELÉTRICO EC 83/B5 0,7HP/1150RPM (220/380V - 60W2) TRIFÁSICO	REXROTH
3	MANÔMETRO COM GLICERINA-DIAMETRO 63mm ESCALA 0 - 25 BAR	REXROTH
4	VALVULA DR6-DF2-31/JOYEE 2713 (COMMOLA R44735) C/ PLACA DE LIGAÇÃO 6341/01 (1/4 BSP)	REXROTH
5	FILTRO - BR-FJ/HR-4AI	REXROTH
6	FILTRO DE AR	REXROTH
7	VISOR DE NÍVEL	REXROTH
8	INDICADOR ELÉTRICO DE NÍVEL NM 100/I	REXROTH
16	VÁLVULA - 1812-BB-04 (1/4NPT) VCL-127	DETROIT
17	VÁLVULA - DBDS6 613/200	REXROTH

NOTA

O INDICADOR DE NÍVEL EMITIRÁ UM SINAL ELÉTRICO QUANDO O NÍVEL CHEGAR AO MÍNIMO. ESTE SINAL DEVERÁ DESLIGAR O MOTOR DA BOMBA, DEVENDO ASSIM SER INTERLIGADO COM A CHAVE DE PARTIDA DO MOTOR. É RECOMENDÁVEL TAMBÉM QUE SEJA FEITA UMA DERIVAÇÃO DESTES SINAL PARA ACIONAR UM ALARME A CRITÉRIO DO CLIENTE.

ATENÇÃO

A BOMBA NÃO DEVERÁ OPERAR SEM ÓLEO, CASO CONTRÁRIO SE ESTRAGARÁ.

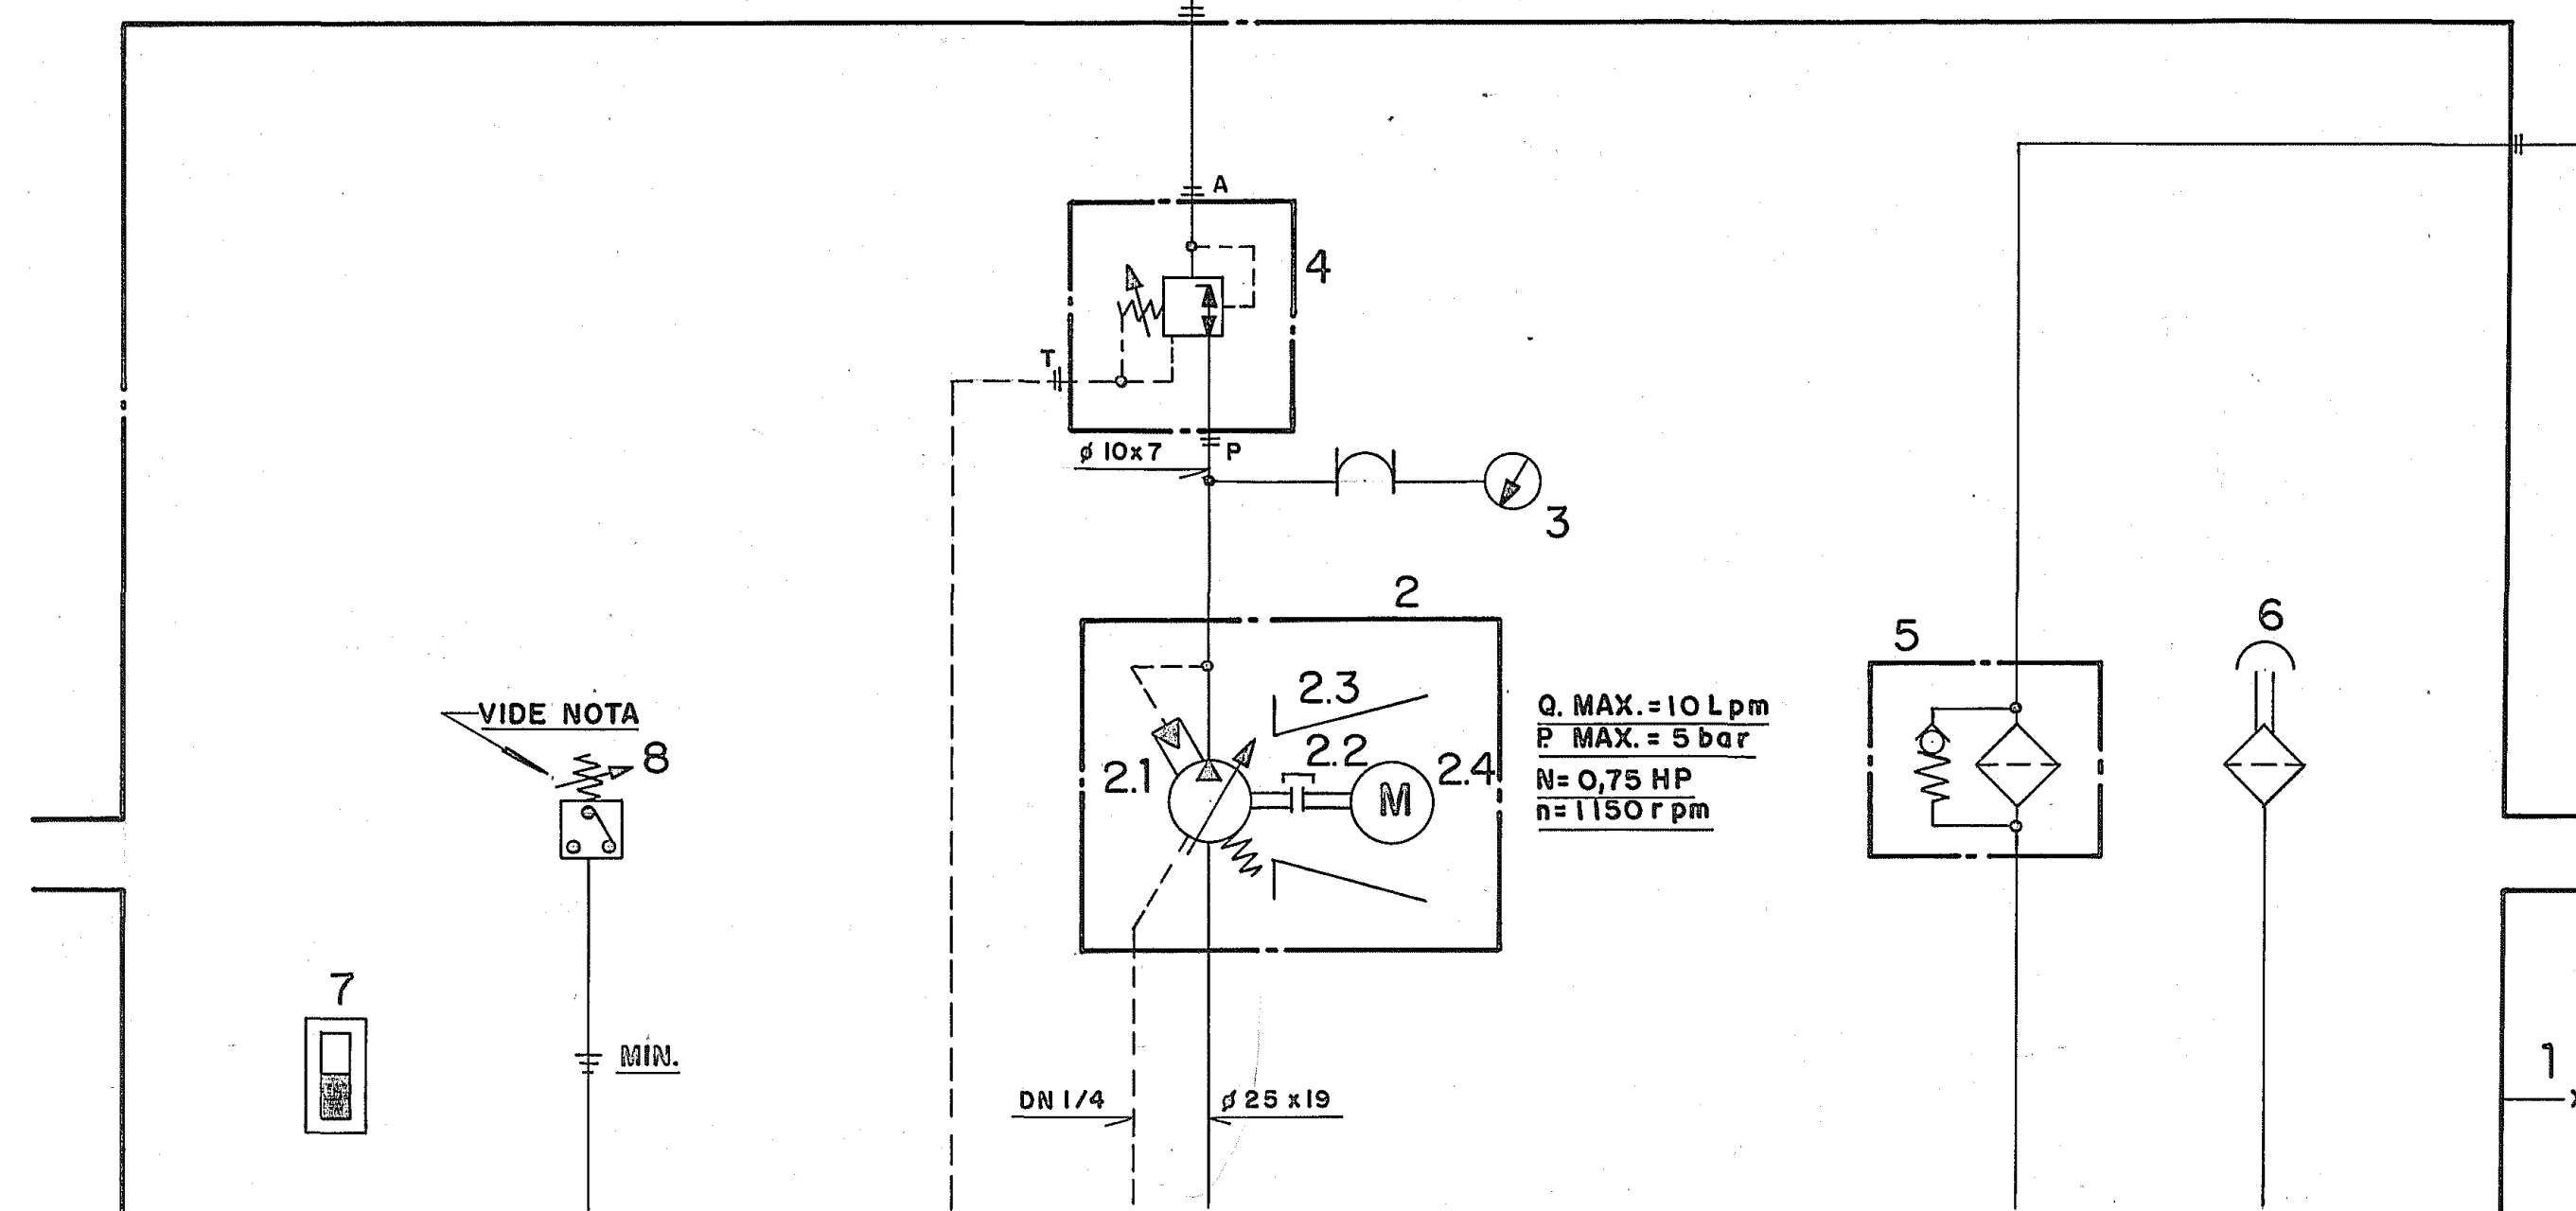

OBS:

ESQUEMA HIDRAULICO DE OPERAÇÃO DOS MECANISMOS DE INVERSÃO E PINÇA COM AMORTECIMENTO CONSTANTE, E FLUXO DE ÓLEO CONTÍNUO.

VIDROS VITON LTDA.		DES.	VER.
M.T.		DATA	14-05-93
ENC. P/ MECAN. DE INVERSÃO E		N.º DO PROJ.	VVL-124
PINÇA C/ AMORT. CONST. HIDRAUL.		N.º DA PEÇA	VV-5211
VIDE OBS.		ESCALA	N.º DO DES.
TRAT. TERM.			