


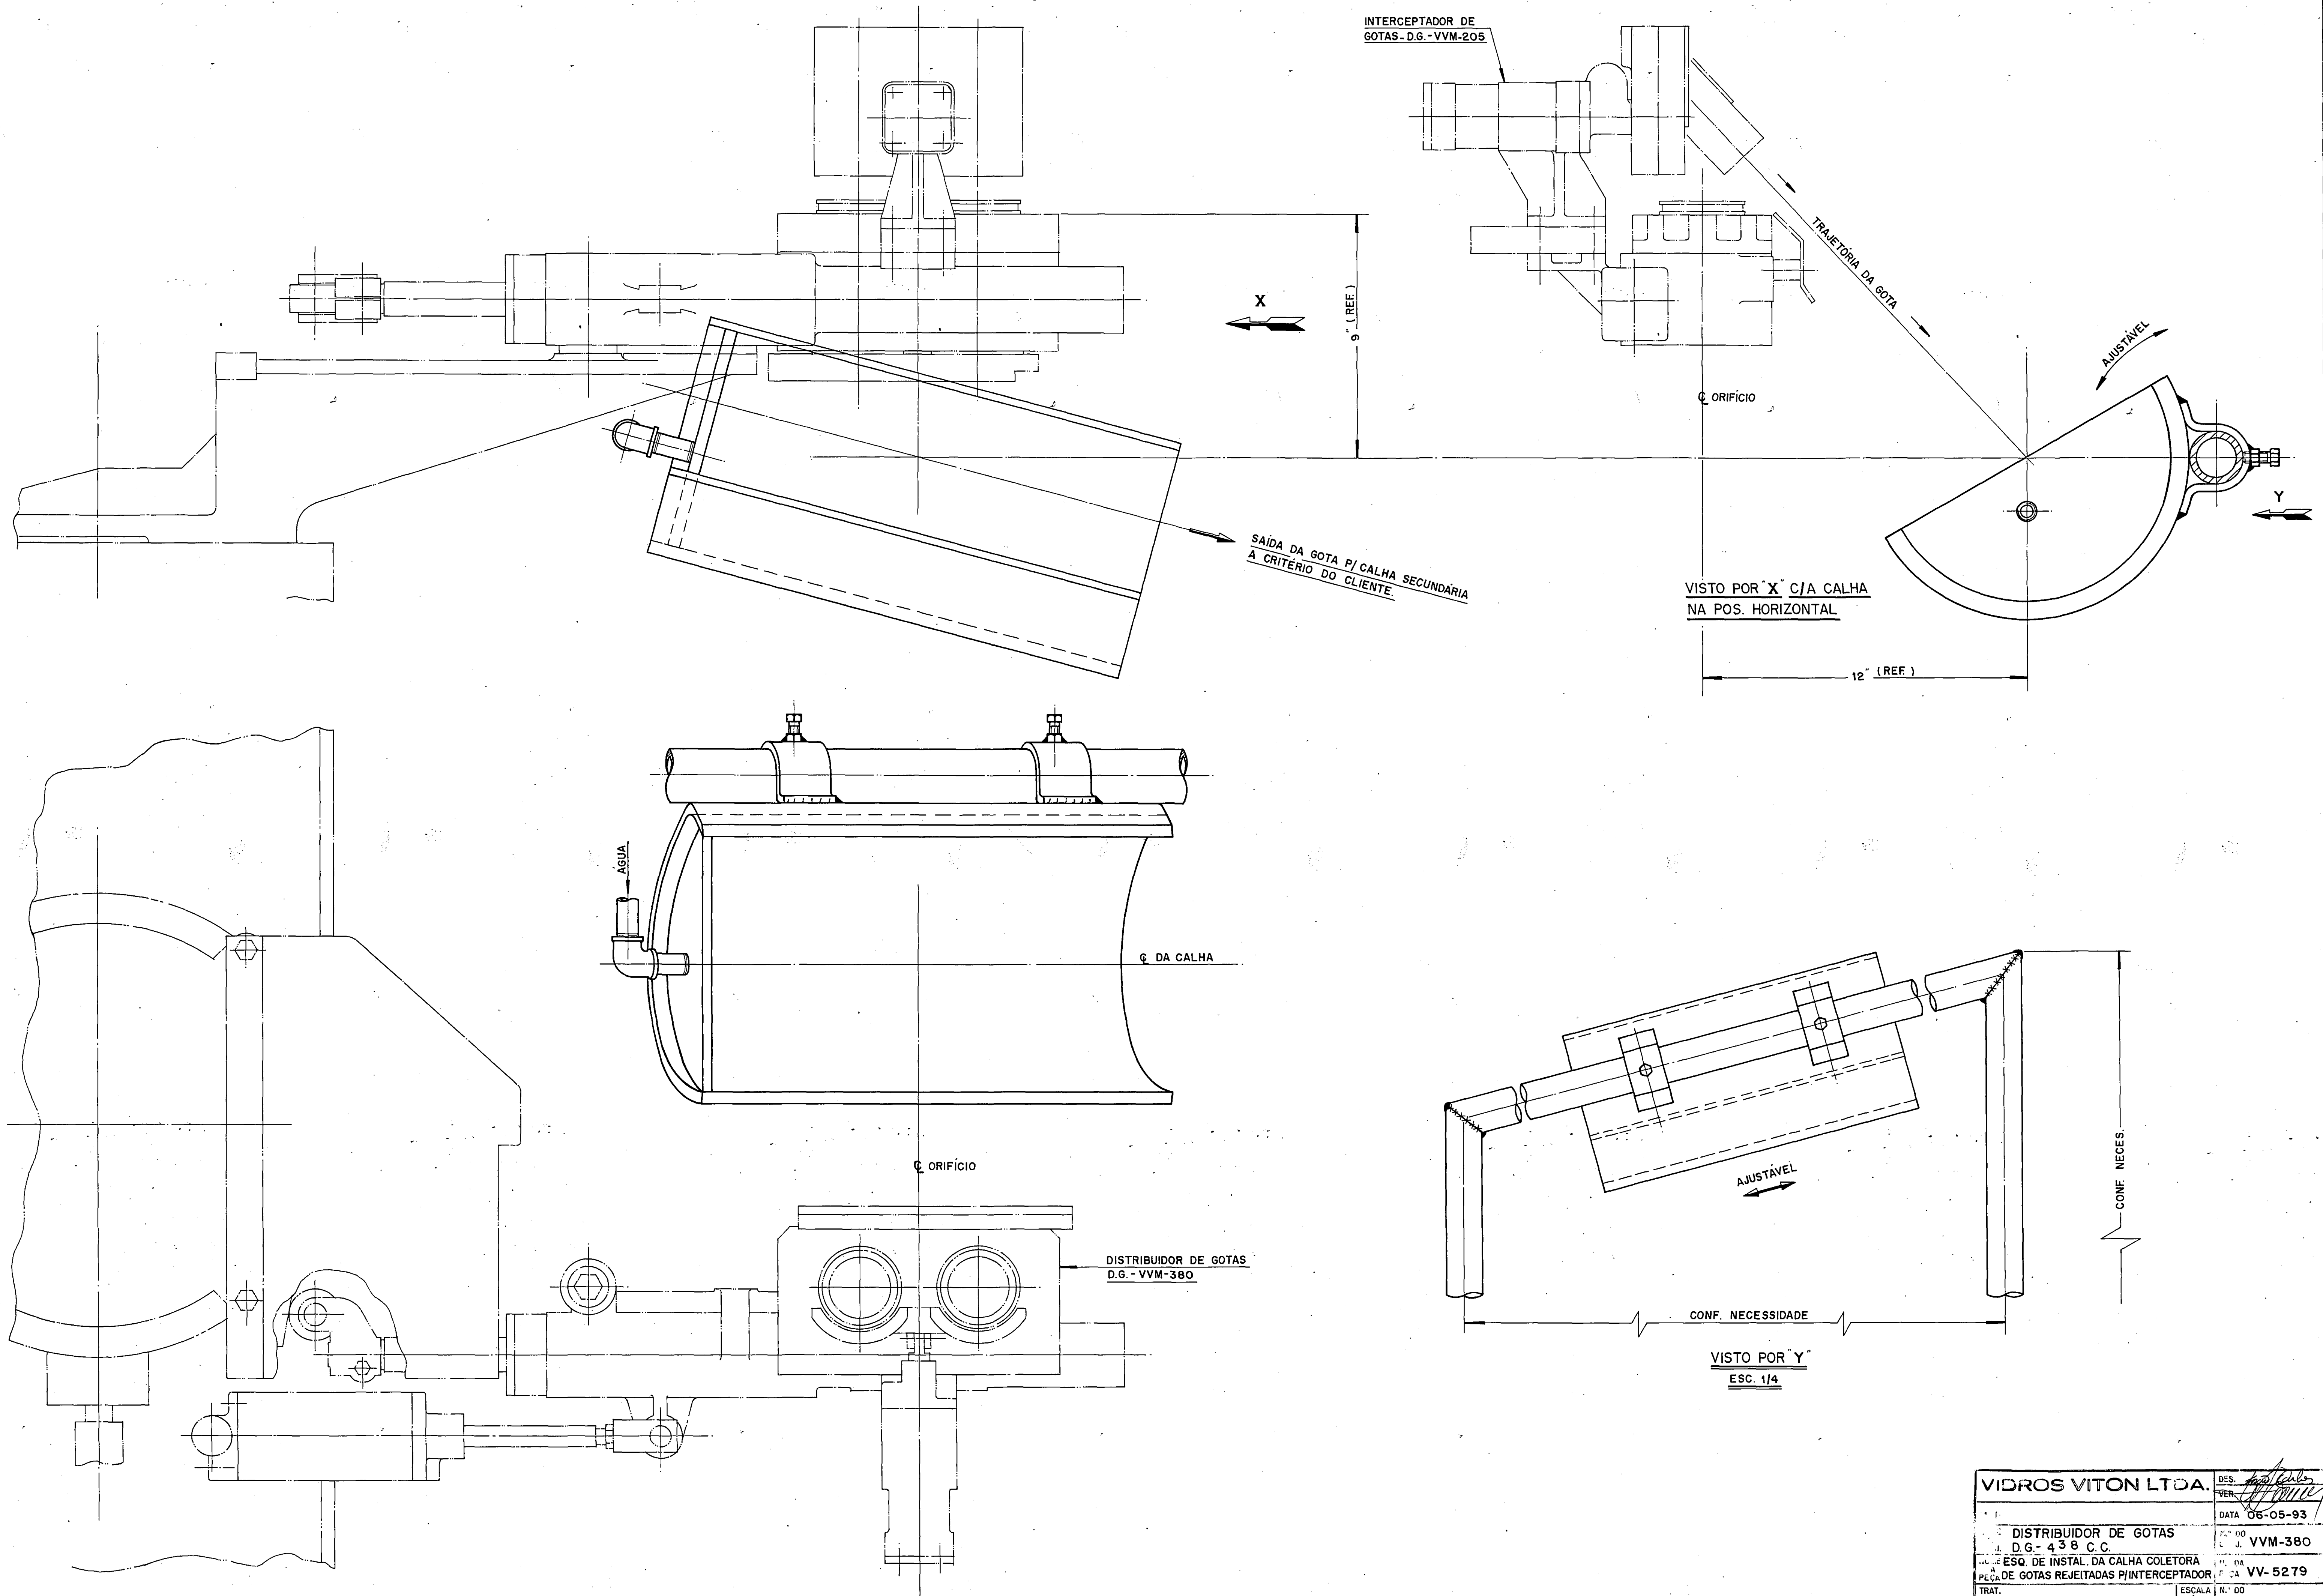

VIDROS VITON LTDA.		DES. <i>[assinatura]</i>
		VER. <i>[assinatura]</i>
		DATA 06-05-93
DISTRIBUIDOR DE GOTAS		REV. 00
D.G. - 438 C.C.		REV. 01 VVM-380
ESQ. DE INSTAL. DA CALHA COLETORA		REV. 02
PEÇA DE GOTAS REJEITADAS P/INTERCEPTADOR		REV. 03 VV-5279
TRAT.	ESCALA 3/8	N.º DO DES.
TERM.		