
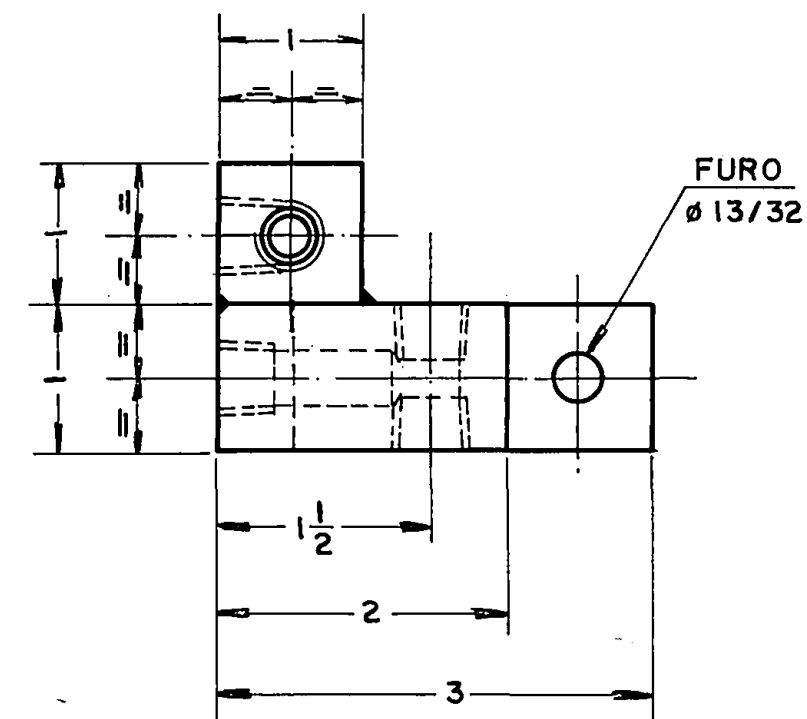



4 FUROS $\phi 7/16 \times 1/2$ PROF.
C/ ROSCA $\phi 1/4$ NPT

FURO $\phi 5/16$ PASSANTE C/ REB. $\phi 7/16 \times 1/2$ PROF.
C/ ROSCA $\phi 1/4$ NPT NOS EXTREMOS

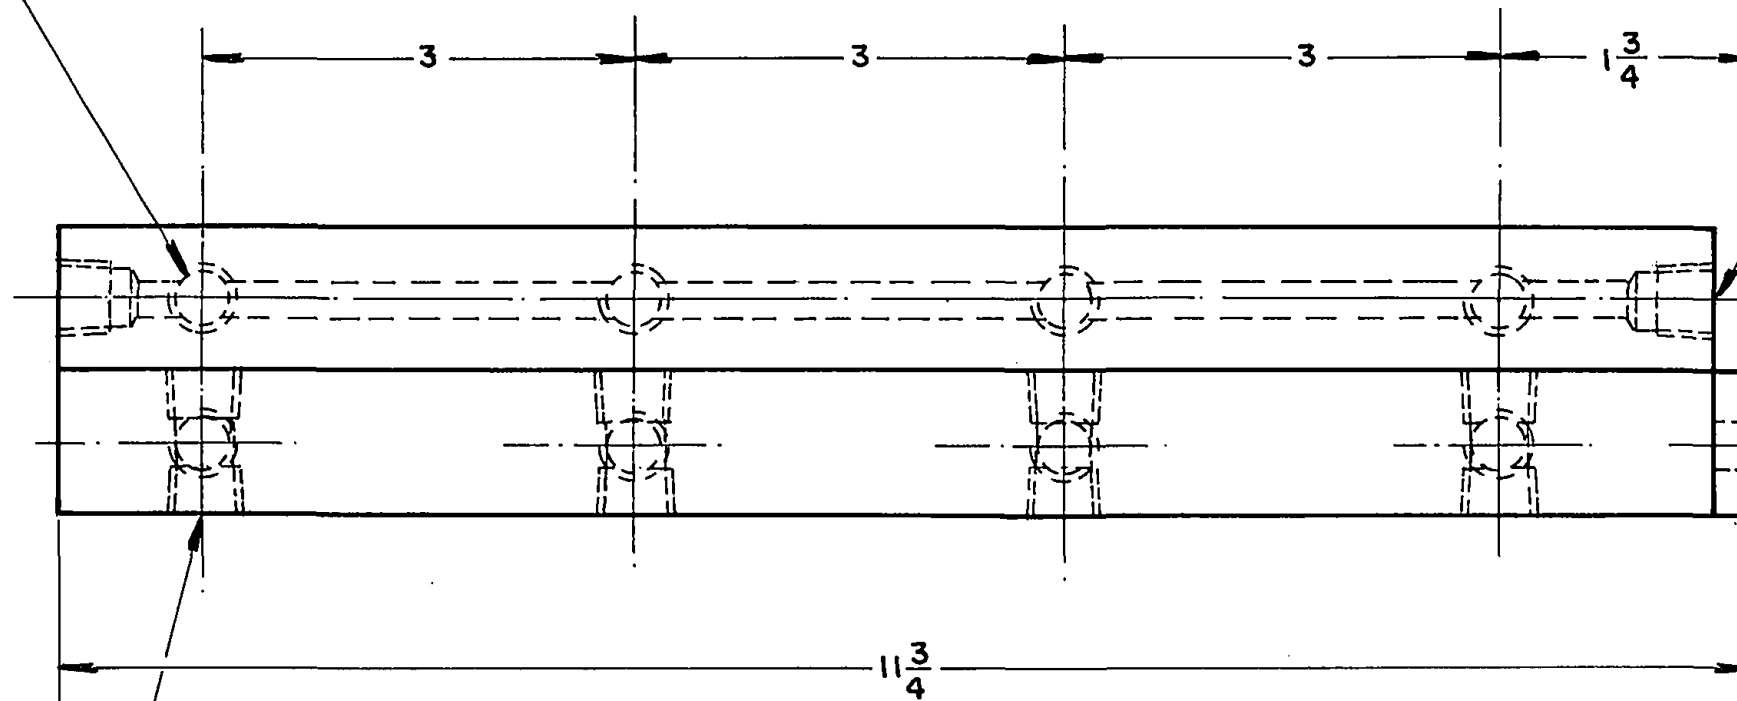

4 FUROS $\phi 7/16$ PASSANTE C/ ROSCA
 $\phi 1/4$ NPT NOS DOIS EXTREMOS

4 FUROS $\phi 7/16 \times 1 5/8$ PROF. C/
ROSCA $\phi 1/4$ NPT

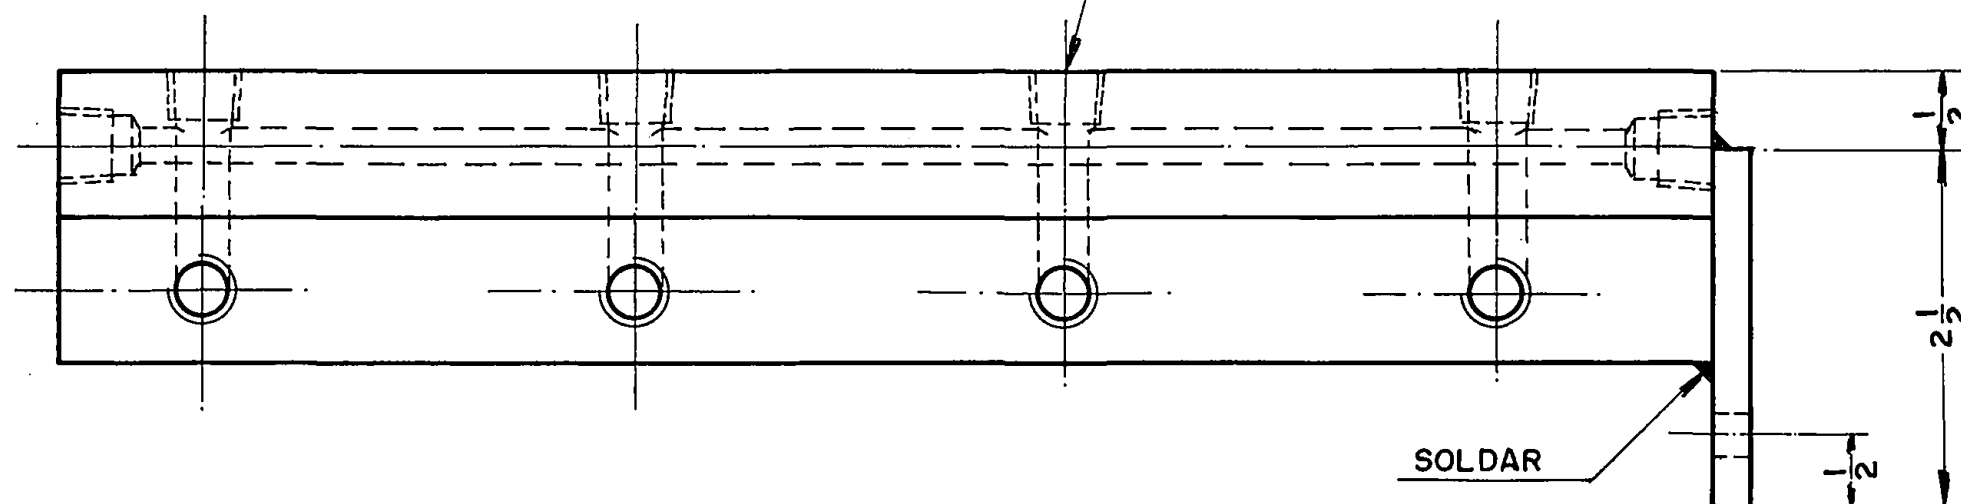

DATA: 12-11-93	VIDROS VITON LTD.	
TOLERÂNCIAS STANDARD PARA SUPERFÍCIES USINADAS SEM TOLERÂNCIA INDICADA	PROJ. AÇO SAE 1.020	
DECIMAL $\pm 0.05"$	NOME DO CCNJ. PAINEL DE CONTROLE	Nº DA CCNJ. VVL-125-A
FRAÇÃO	NOME DA PFCA BLOCO L.D	Nº DA PFCA VV-5412
DE 0" ATÉ 5" $\pm 1/64$	TRAT. TERM.	Nº DO BLOCO
DE 5" ATÉ 24" $\pm 1/32$		
ACIMA DE 24" $\pm 1/16$		
		3/4