


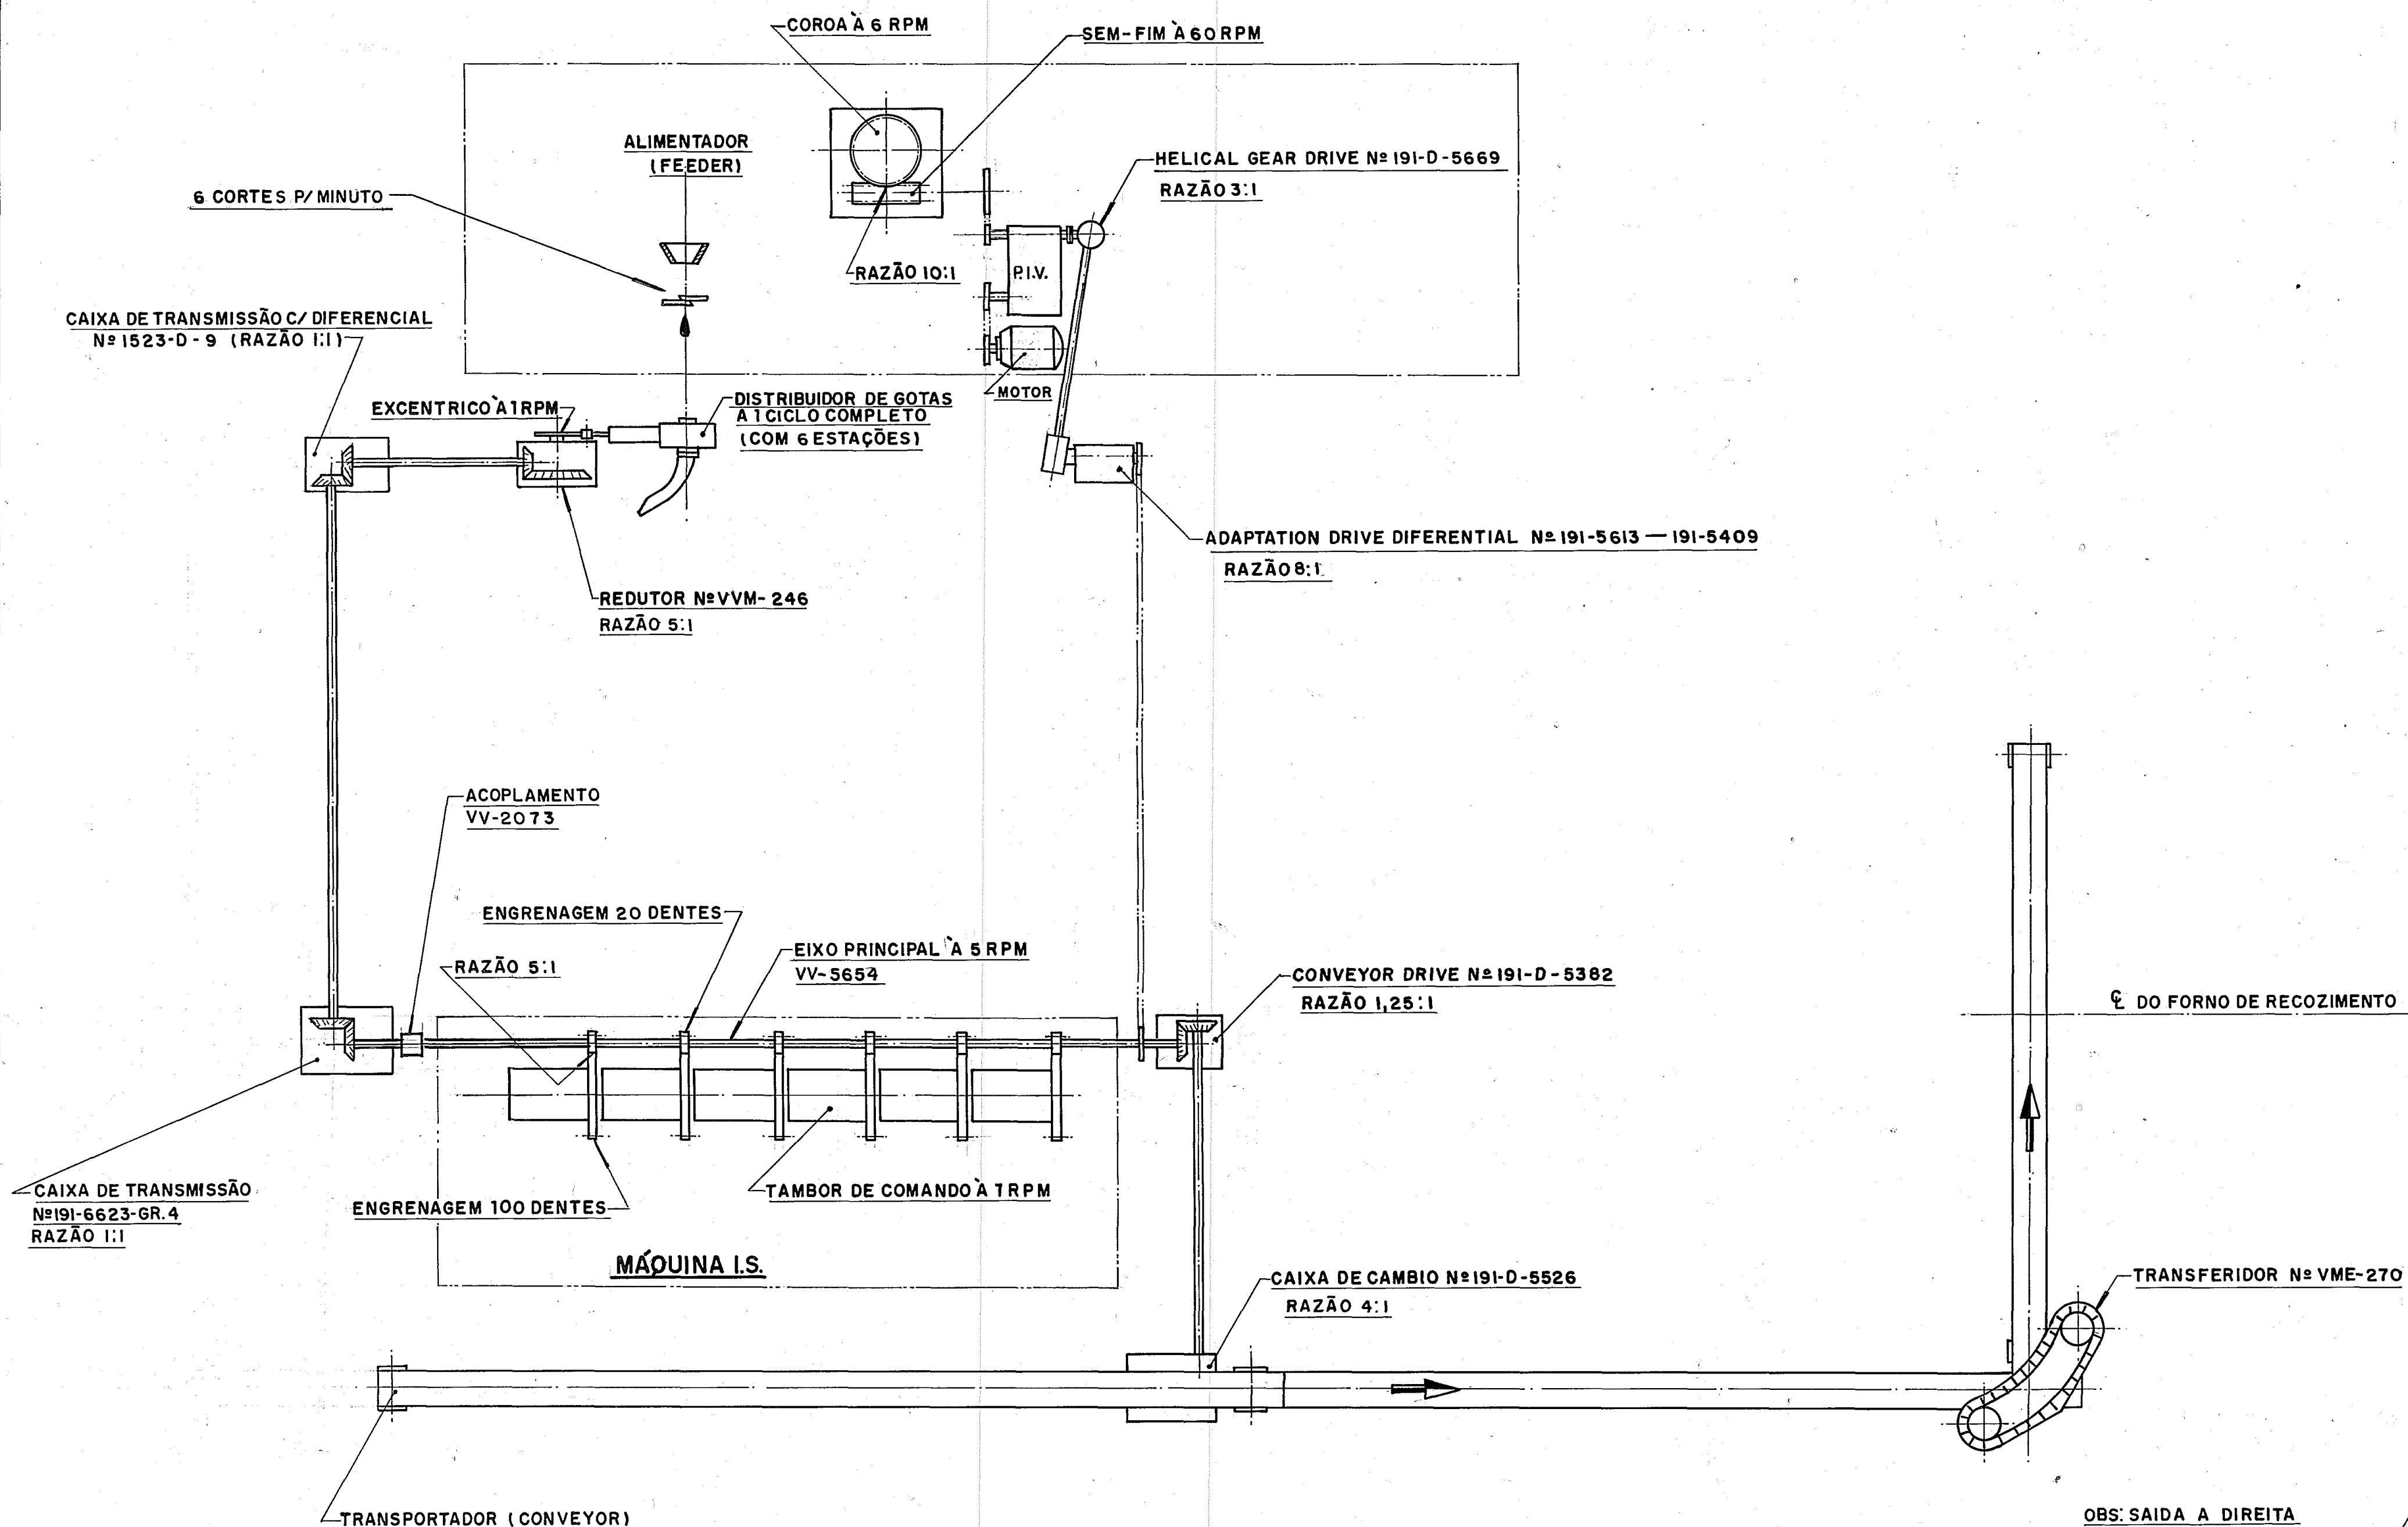

OBS: SAIDA A DIREITA

VIDROS VITON LTDA.		DES. <i>X/10</i>
		VER.
MAT:		DATA 17-11-94
NOME DO CONJ.	SISTEMA DE TRANSMISSÃO	N.º DO CONJ. VVM-362
NOME DA PEÇA	ESQUEMA DE ACIONAMENTO DA PEÇA	N.º DA PEÇA VV-5630
TRAT. TERM.	ESCALA	N.º DO DES.