


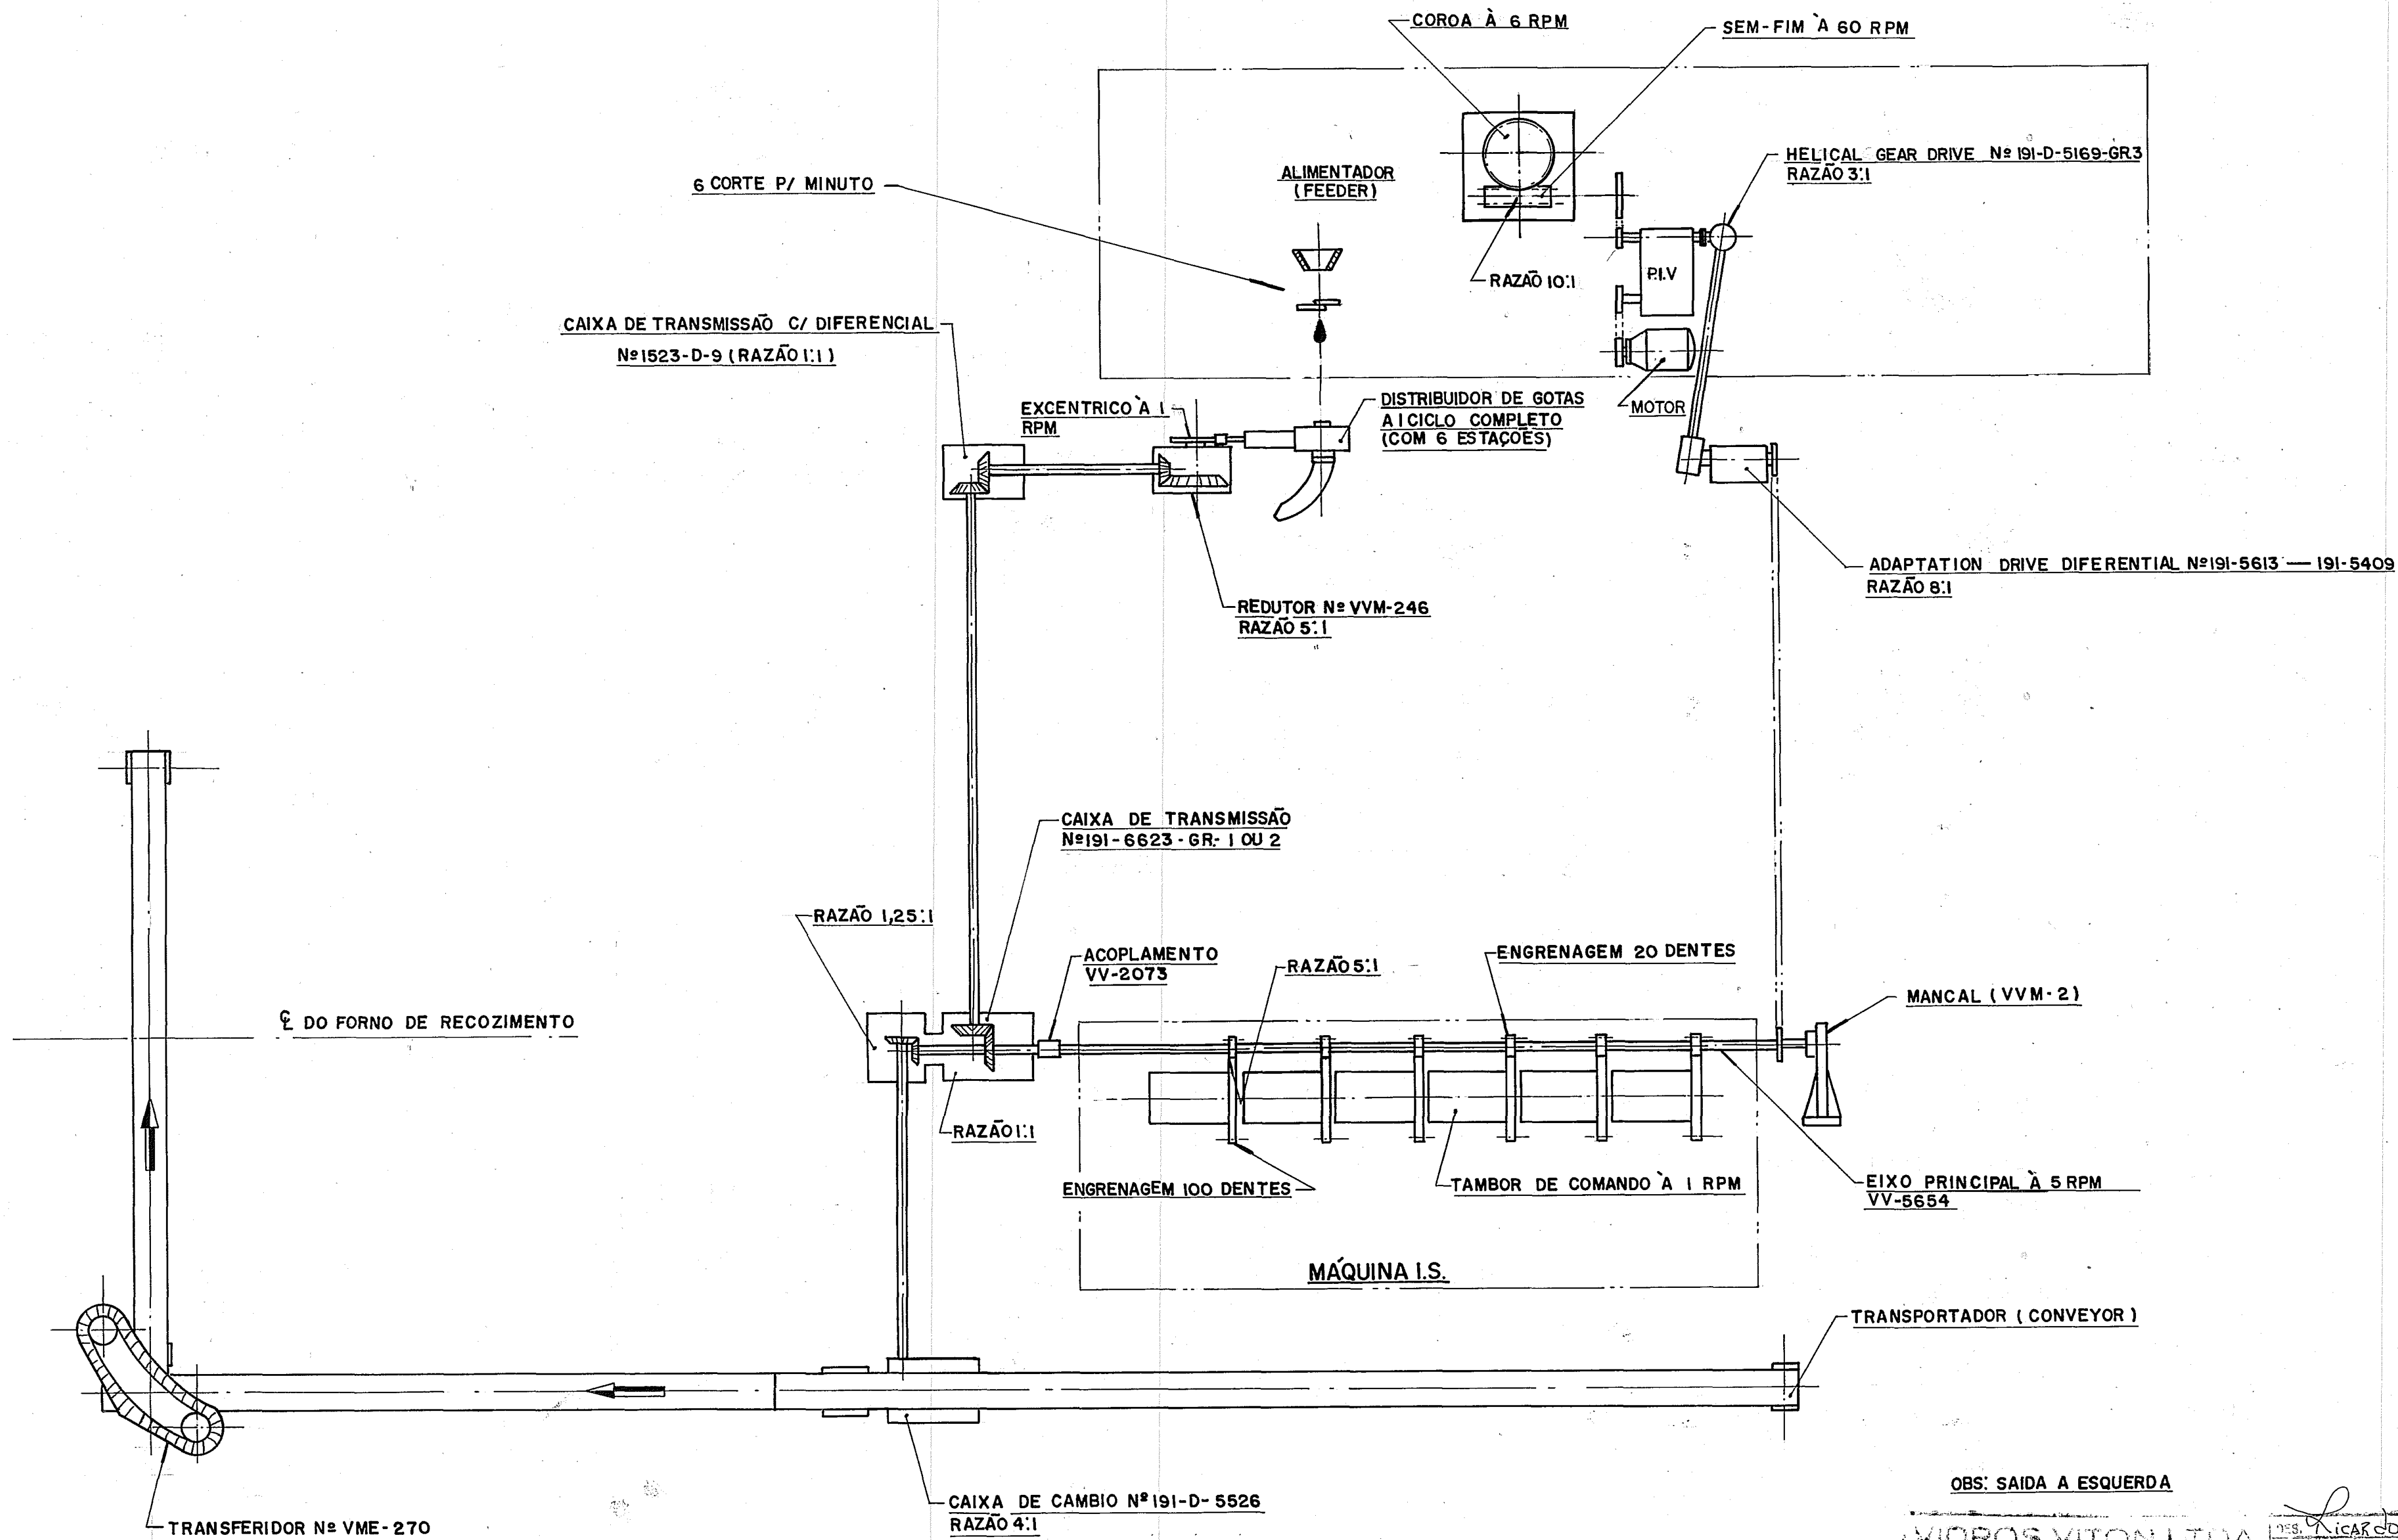

OBS: SAIDA A ESQUERDA

VIDROS VITON LTDA.		DES. <i>Ricardo</i>
MAT:		VER.
NOME DO CONJ. SISTEMA DE TRANSMISSÃO		DATA 31-03-95
NOME DA PEÇA ESQUEMA DE ACIONAMENTO DA MAQ. I.S. 6 SEQ. C/ SIST. CARDANICO		Nº DO CONJ. VVM-362
TRAT. TERM.		Nº DA PEÇA VV-5671
ESCALA		Nº DO DES.