


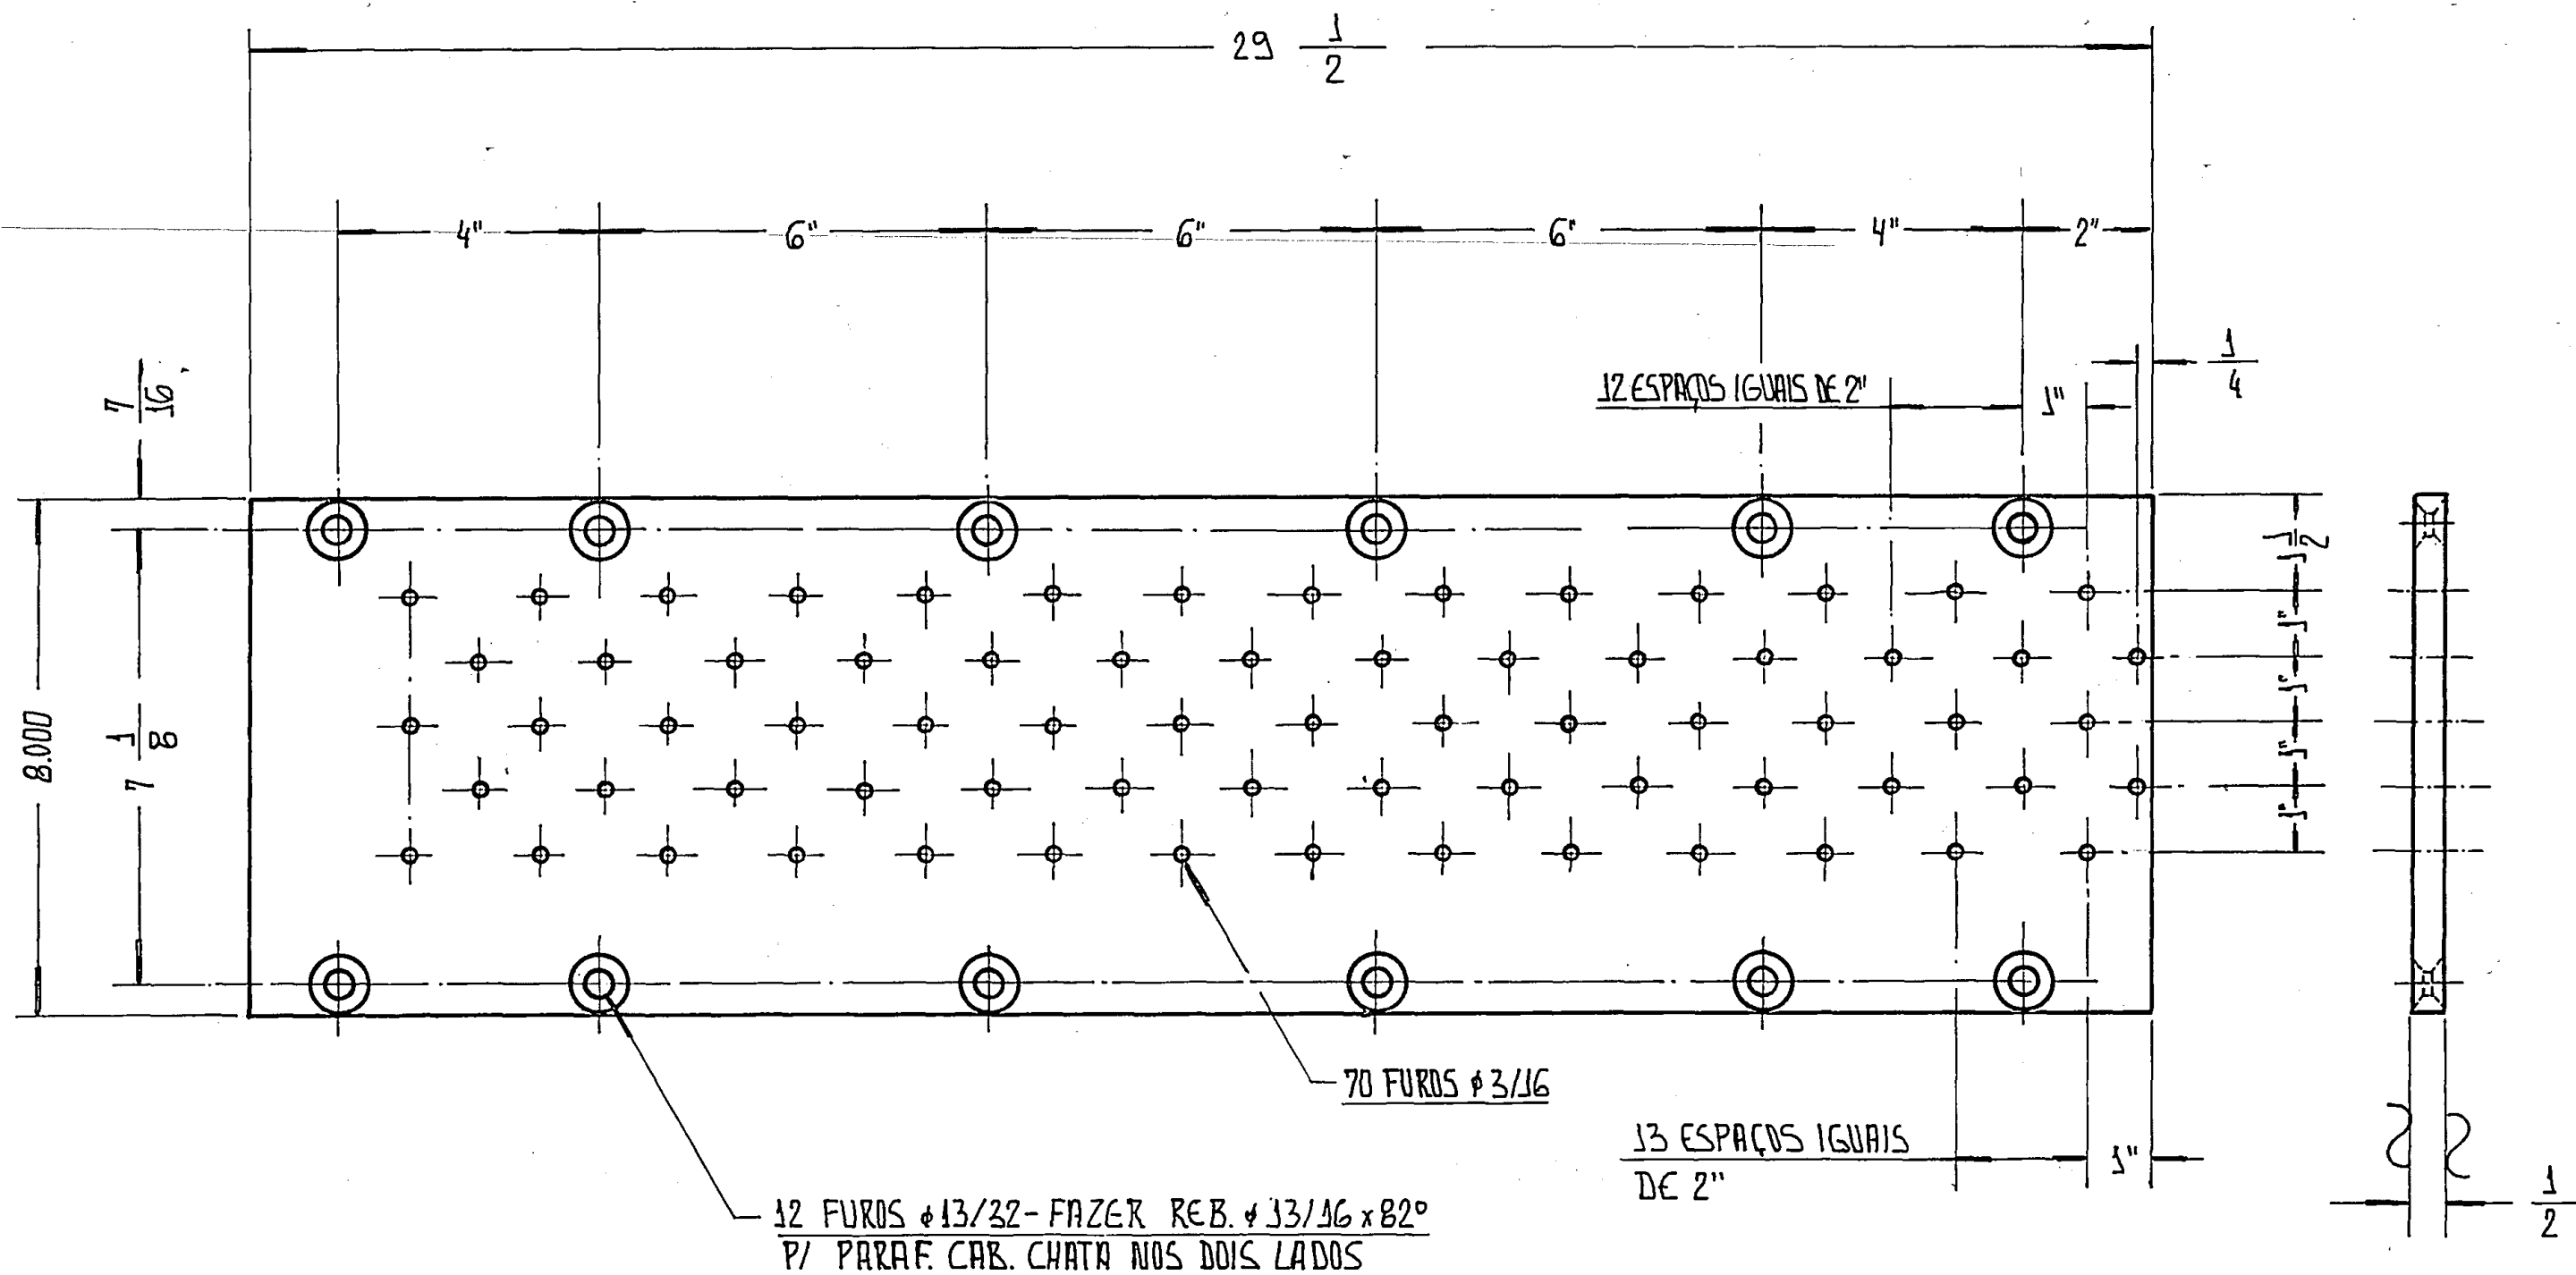

$\nabla(\sim)$

DATA: 30/03/2001	VIDROS VITON LTDA.
TOLERÂNCIAS STANDARD PARA SUPERFÍCIES USUÁRIAS SEM TOLERÂNCIA INDICADA	ACD SAE 1045
FRACAO	FRAME COVERS & TOP PLATES
DE 0" ATÉ 5" $\pm 1/64$	CONJ. DUAL AIR 2 SECTION CONVEYOR
DE 5" ATÉ 24" $\pm 1/32$	PLACA PERFORADA
ACIMA DE 24" $\pm 1/16$	W-206
	W-6268
	3/8"