
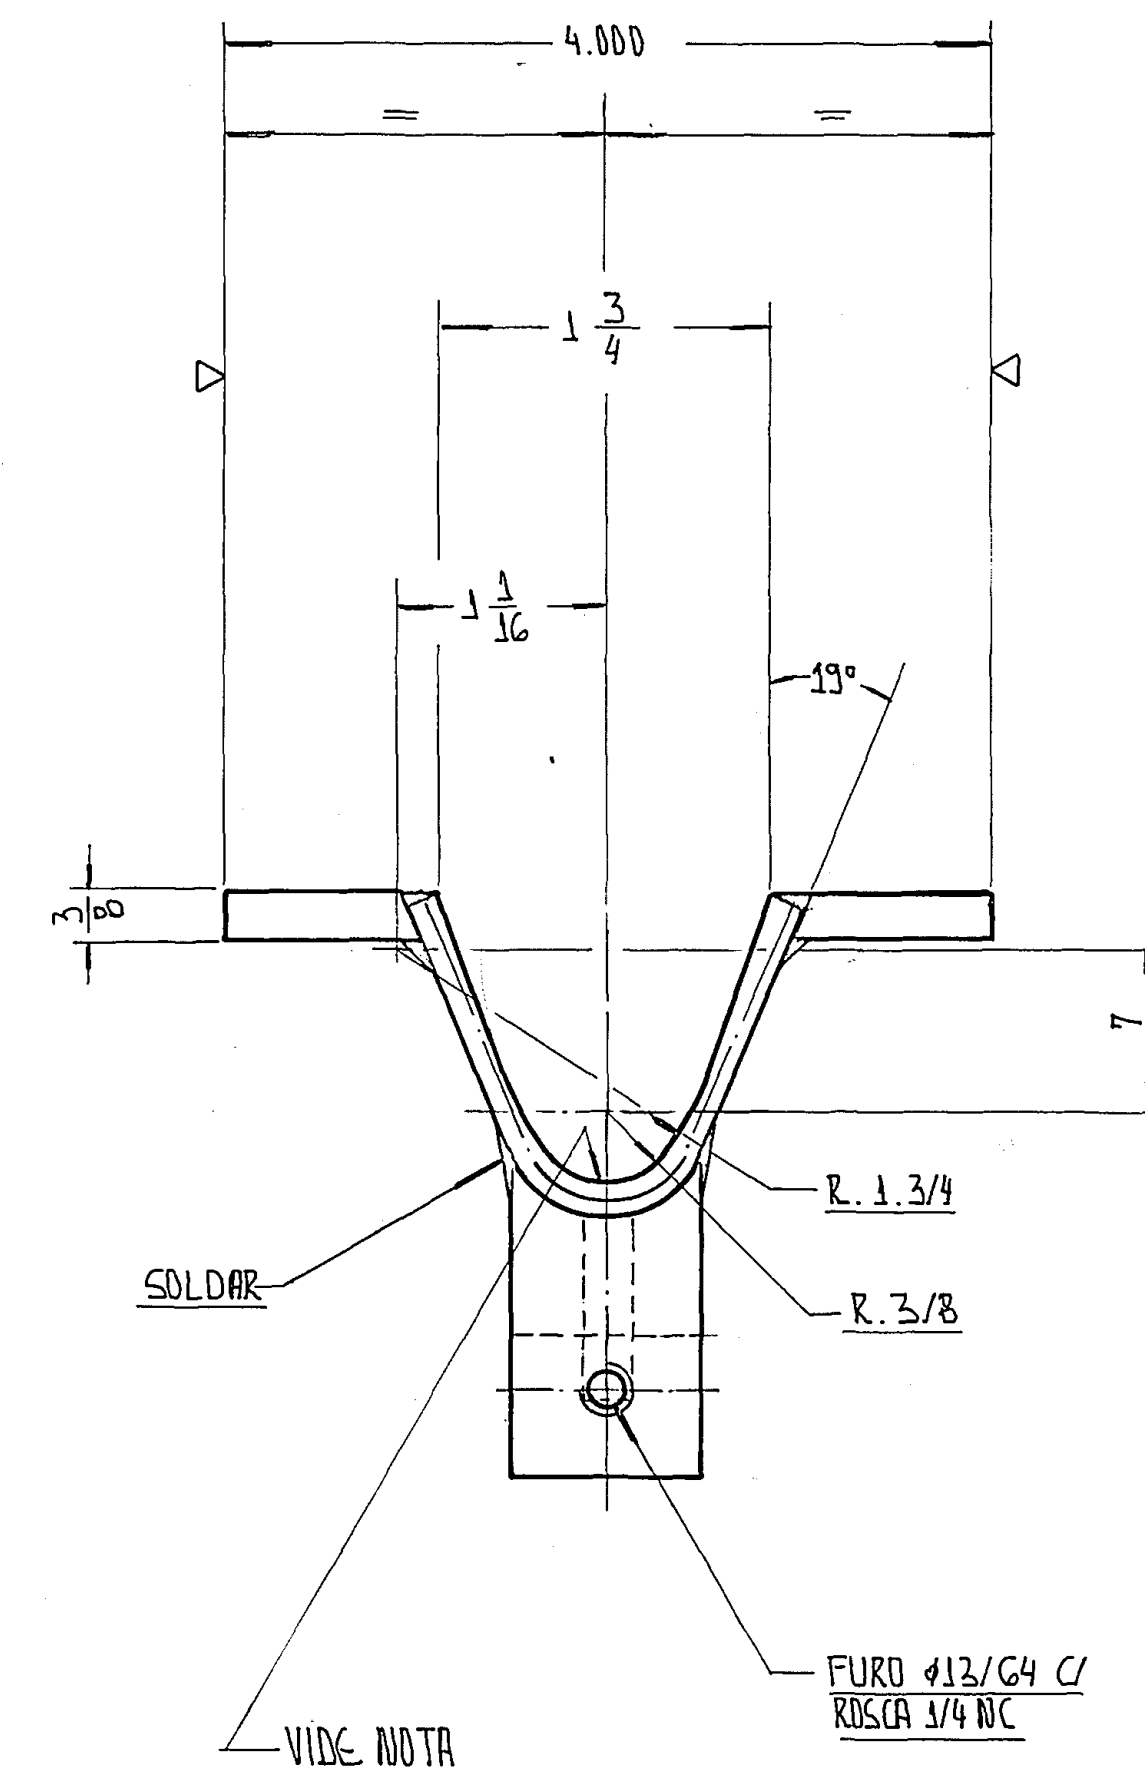


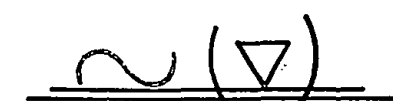

ESTAS SUPERFÍCIES INTERNAS DEVEM SER PERFEITAMENTE LISAS P/ ACEITAR SOMENTE POLIMENTO.

DOBRAR CHAPA C/ PUNÇÃO Nº VD-1829

[illegible]