

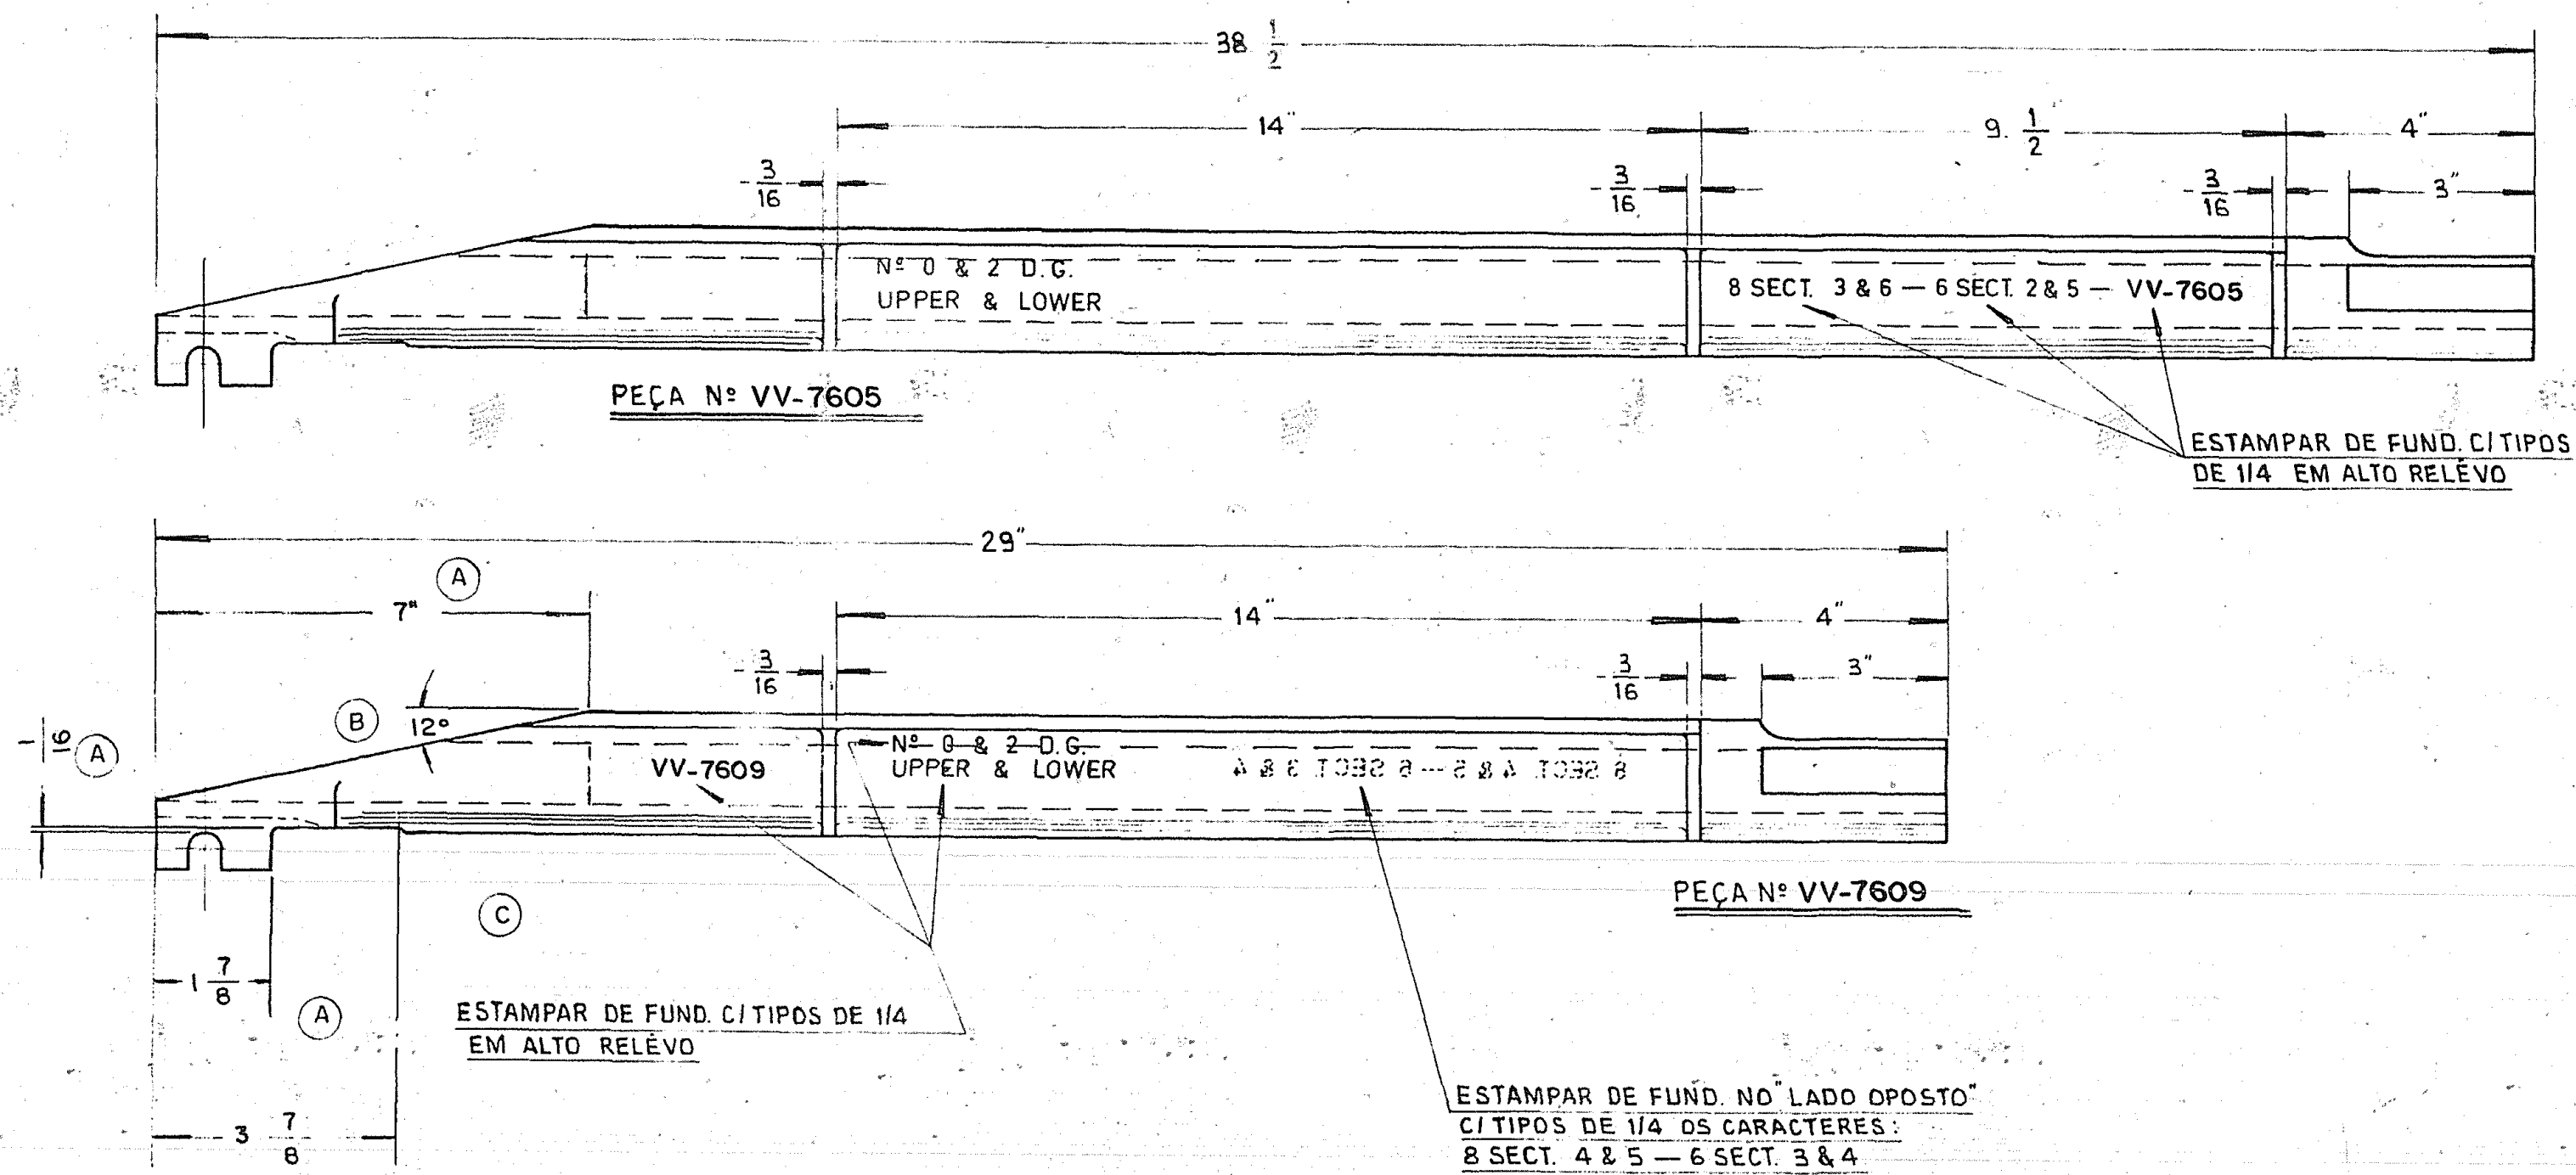
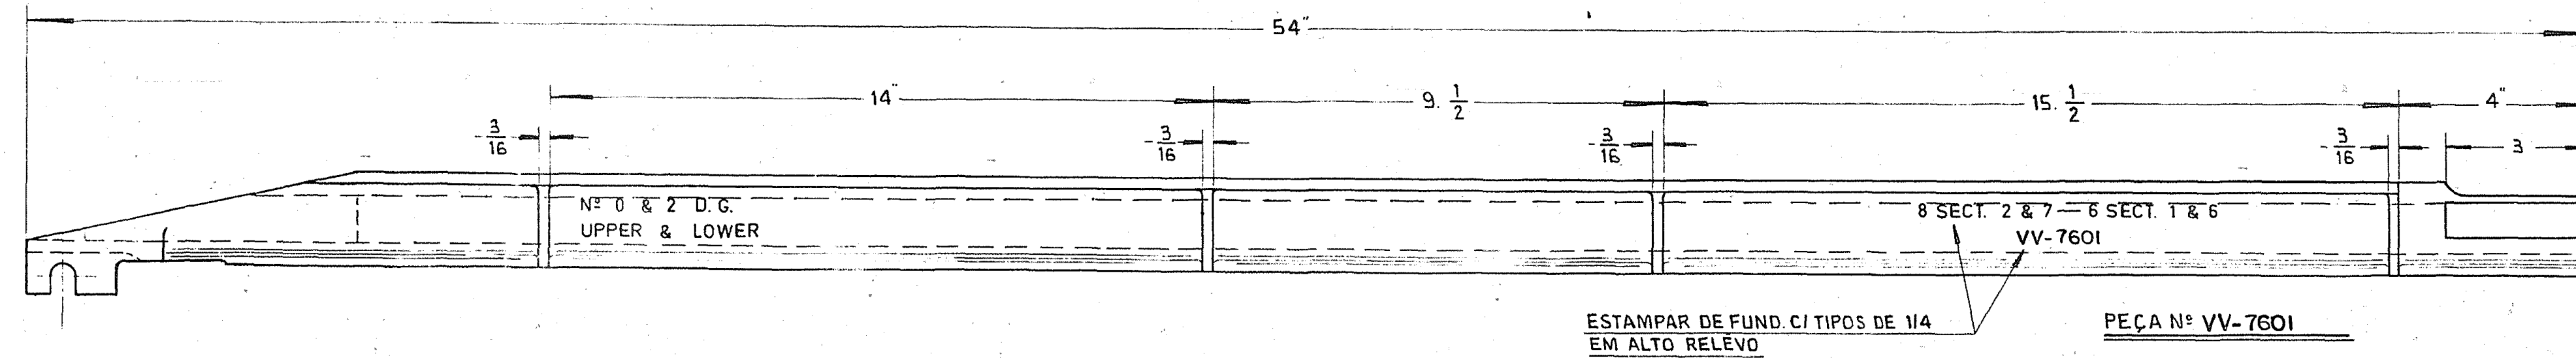
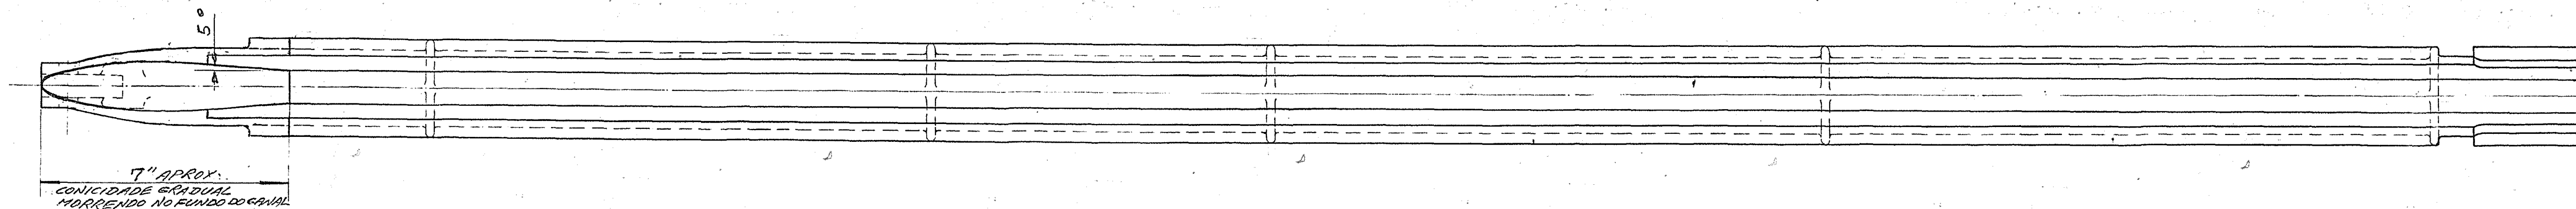
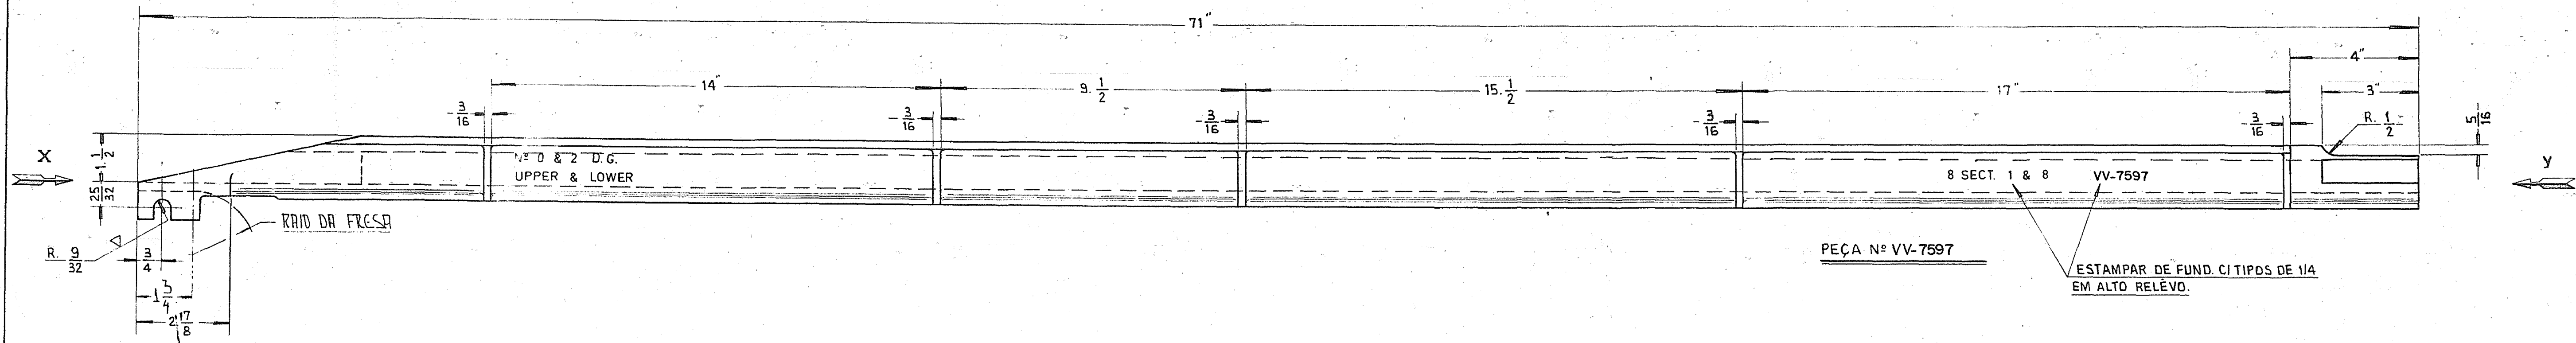


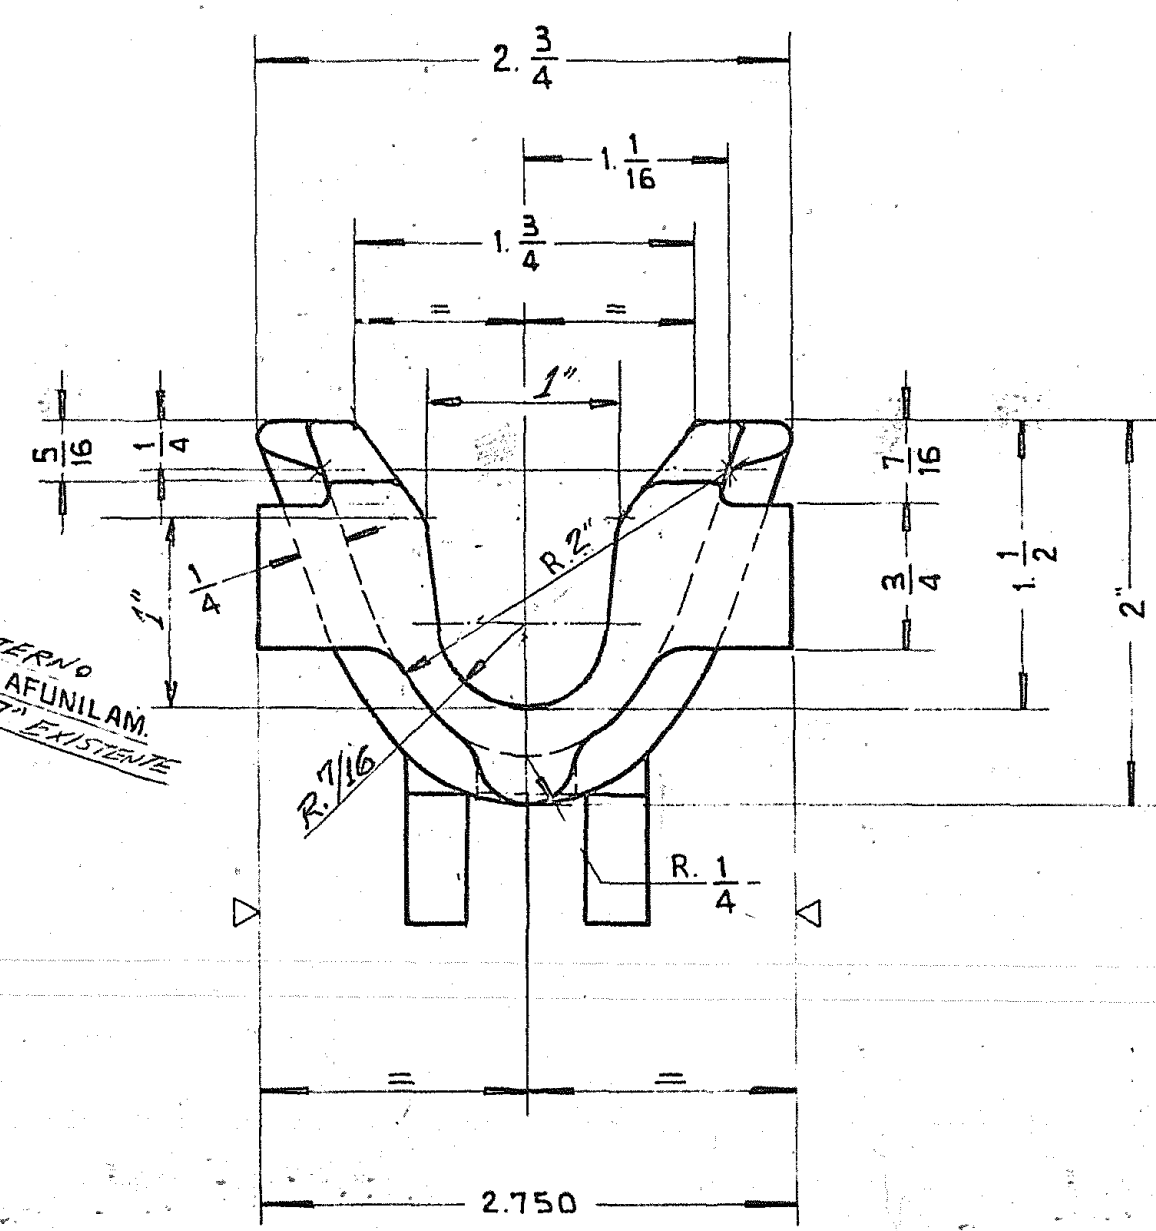

ESTAS SUPERFÍCIES DEVEM SER PERFEITAMENTE LISAS DE FUNDIÇÃO, P/ ACEITAR SOMENTE POLIMENTO.

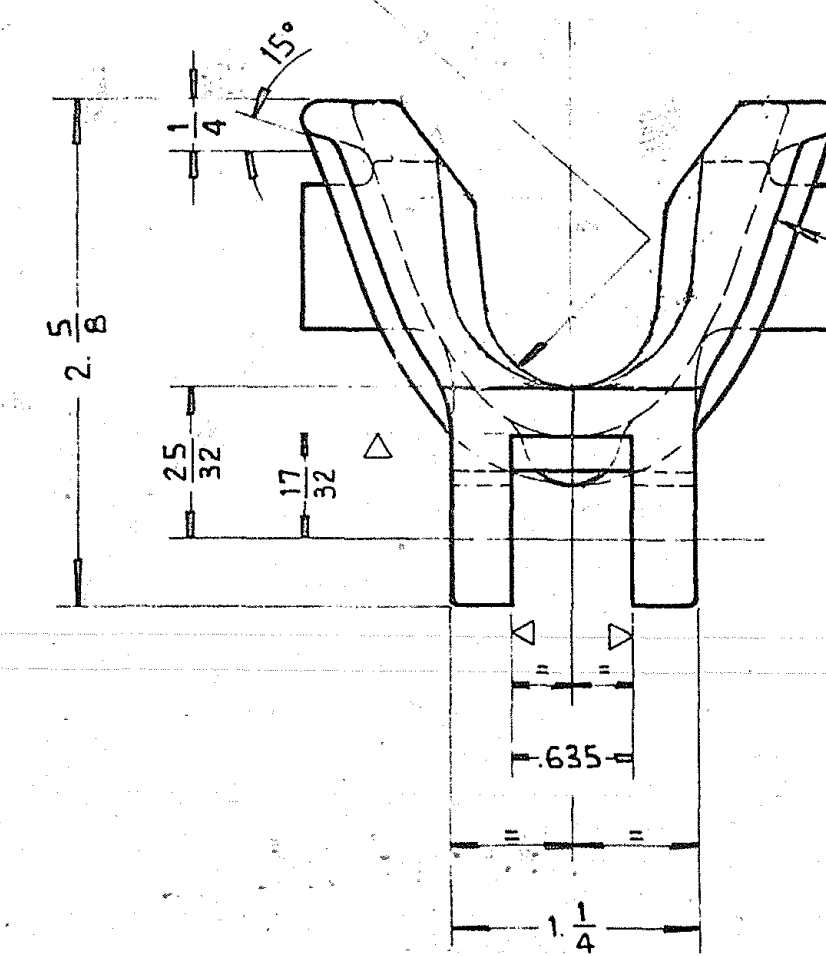

VISTO POR "X" - ESC. 1:1

VISTO POR "Y" - ESC. 1:1

"NOTA PARA FUNDIÇÃO"
USAR MODELOS Nº 191-1545/6/7/8-F
CLAS RESPECTIVAS ALIXAS DE
MACHO VV-7597 VV-7601 VV-7605 VV-7609

PEÇAS Nº
VV-7597
VV-7601
VV-7605
VV-7609

ALTERADA	INOMENCL.	D
4.308	ELIM. 3.11	C
5.100	ERR. 20	B
5.100	ERR. 20	A

VIERO VISION 1.1
FERRO FUND. 66-15
DELIVERY EQUIPMENT D.G. 62
8 SECT. IN LINE I.S. MACHINE
TROUGH TAM. I D.G.
UPPER & LOWER
191-6613
VIDE ANOT.