
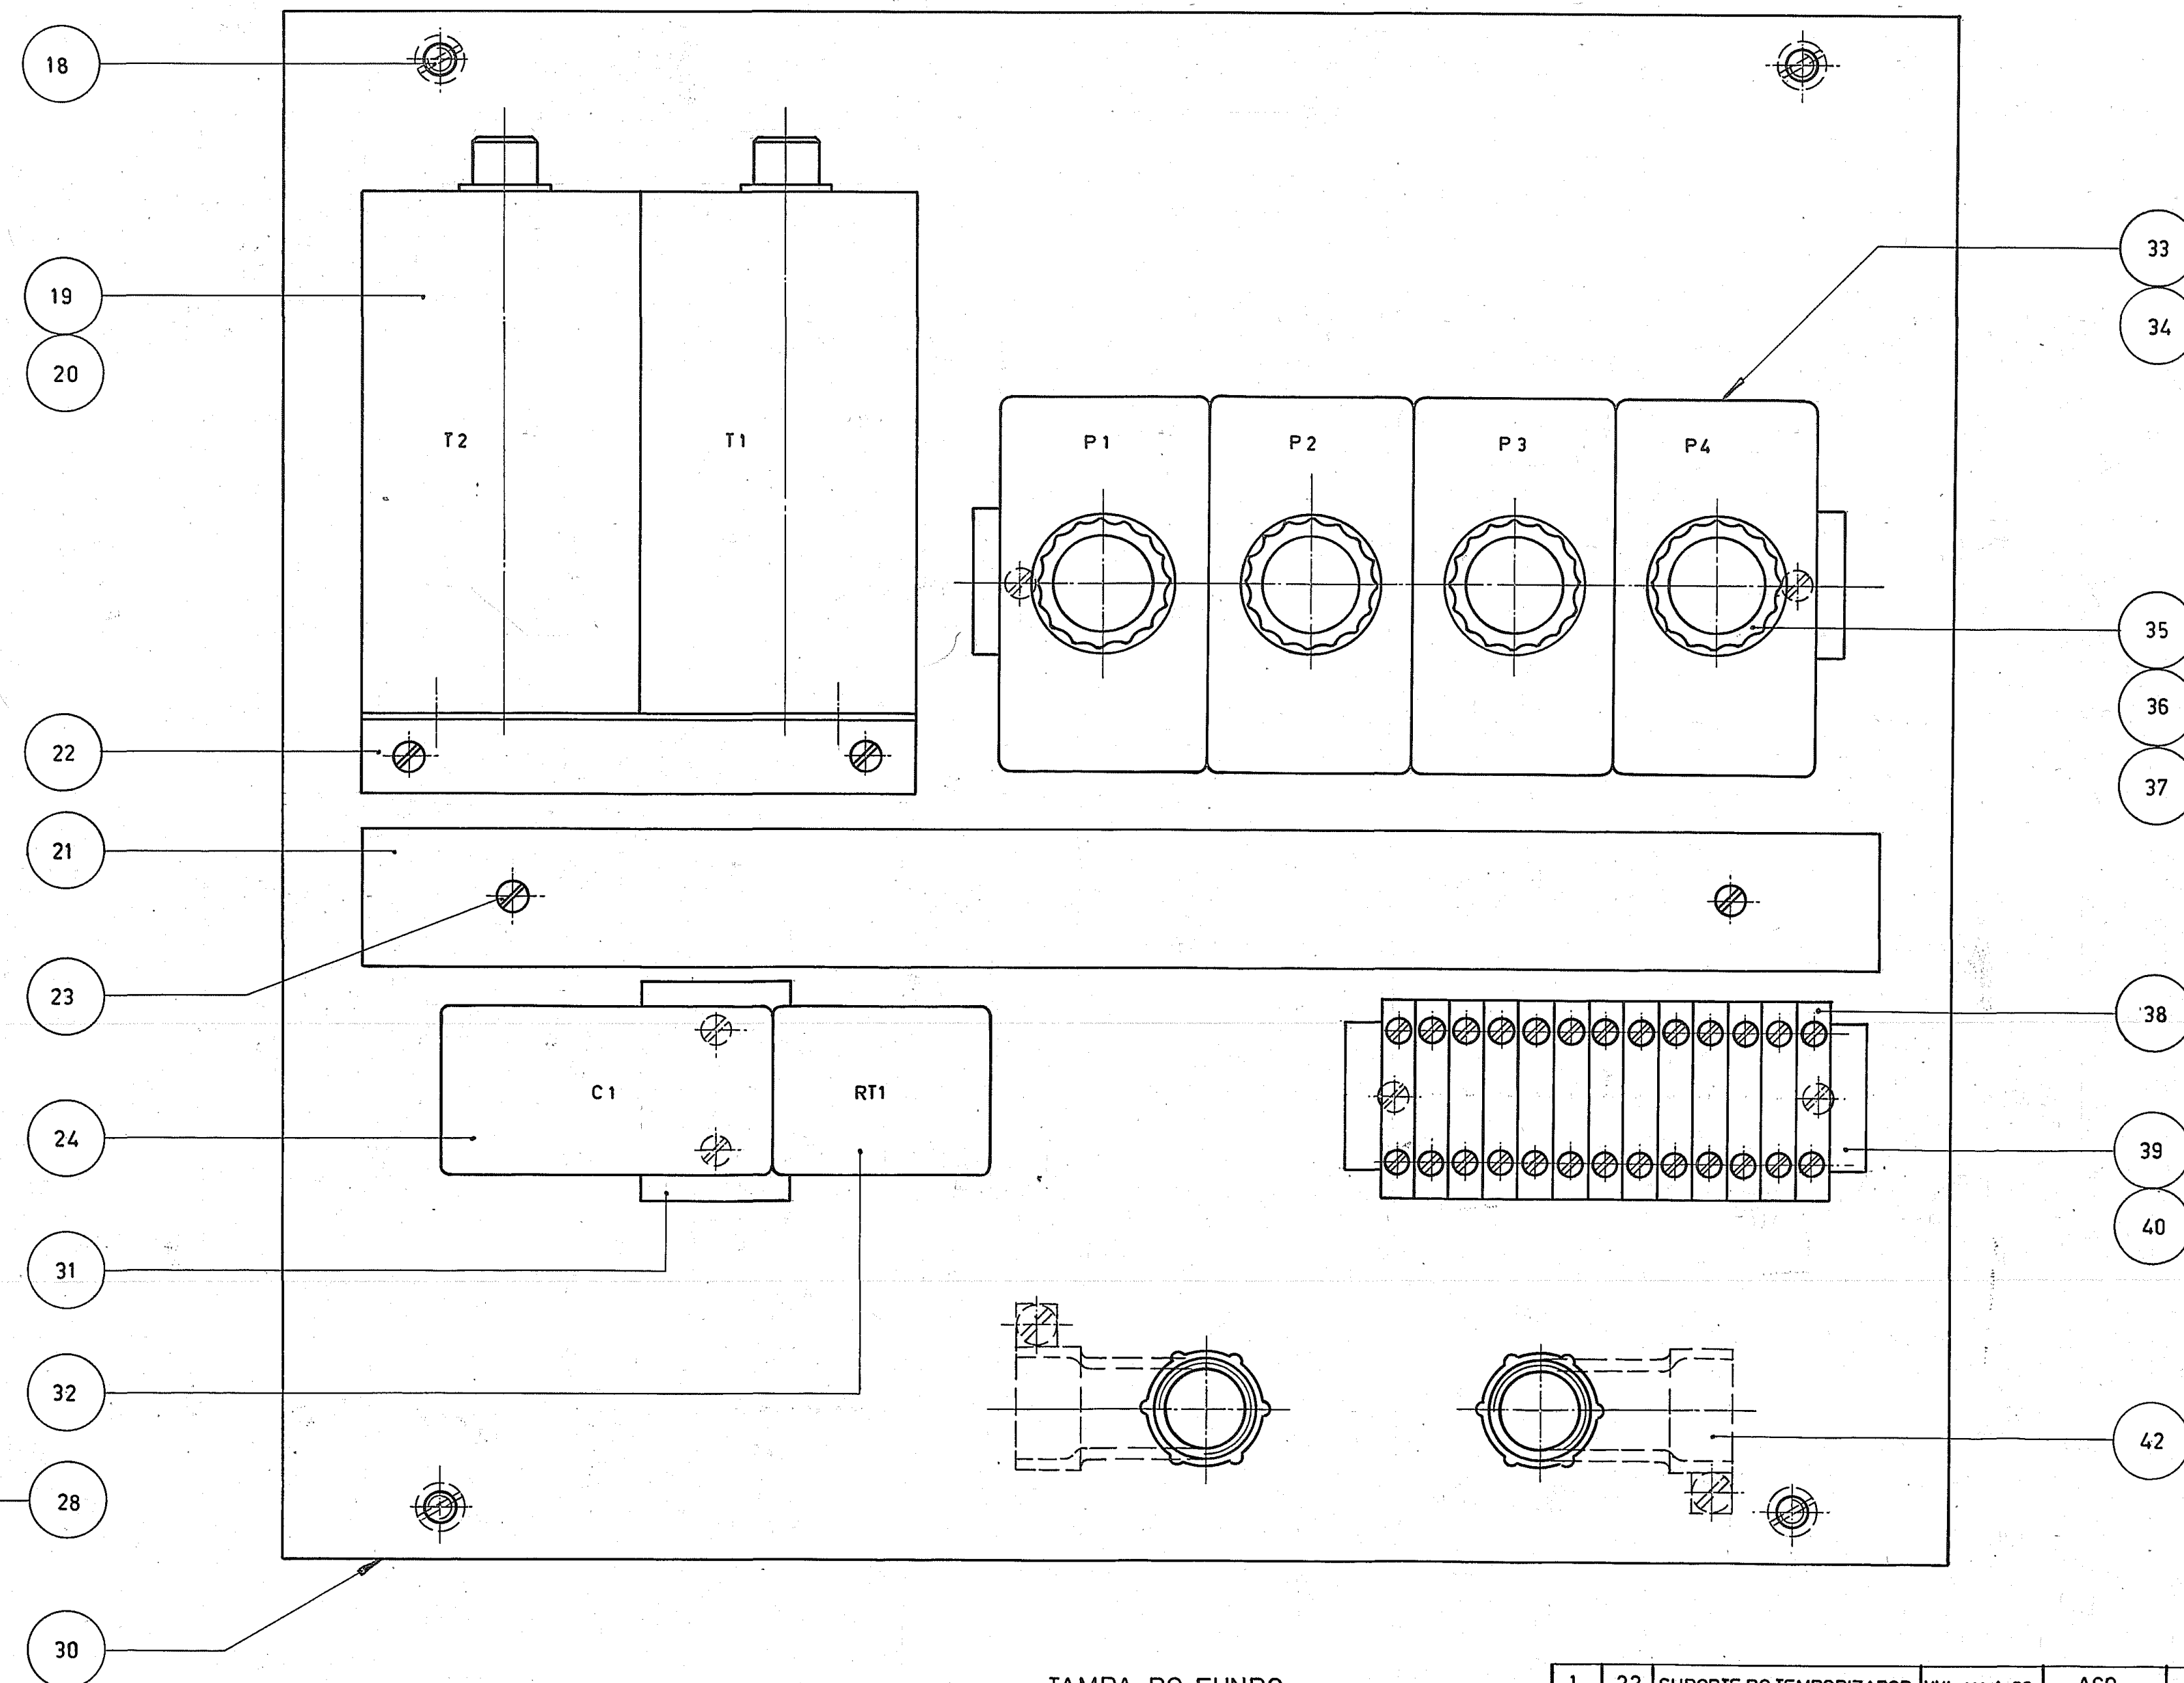


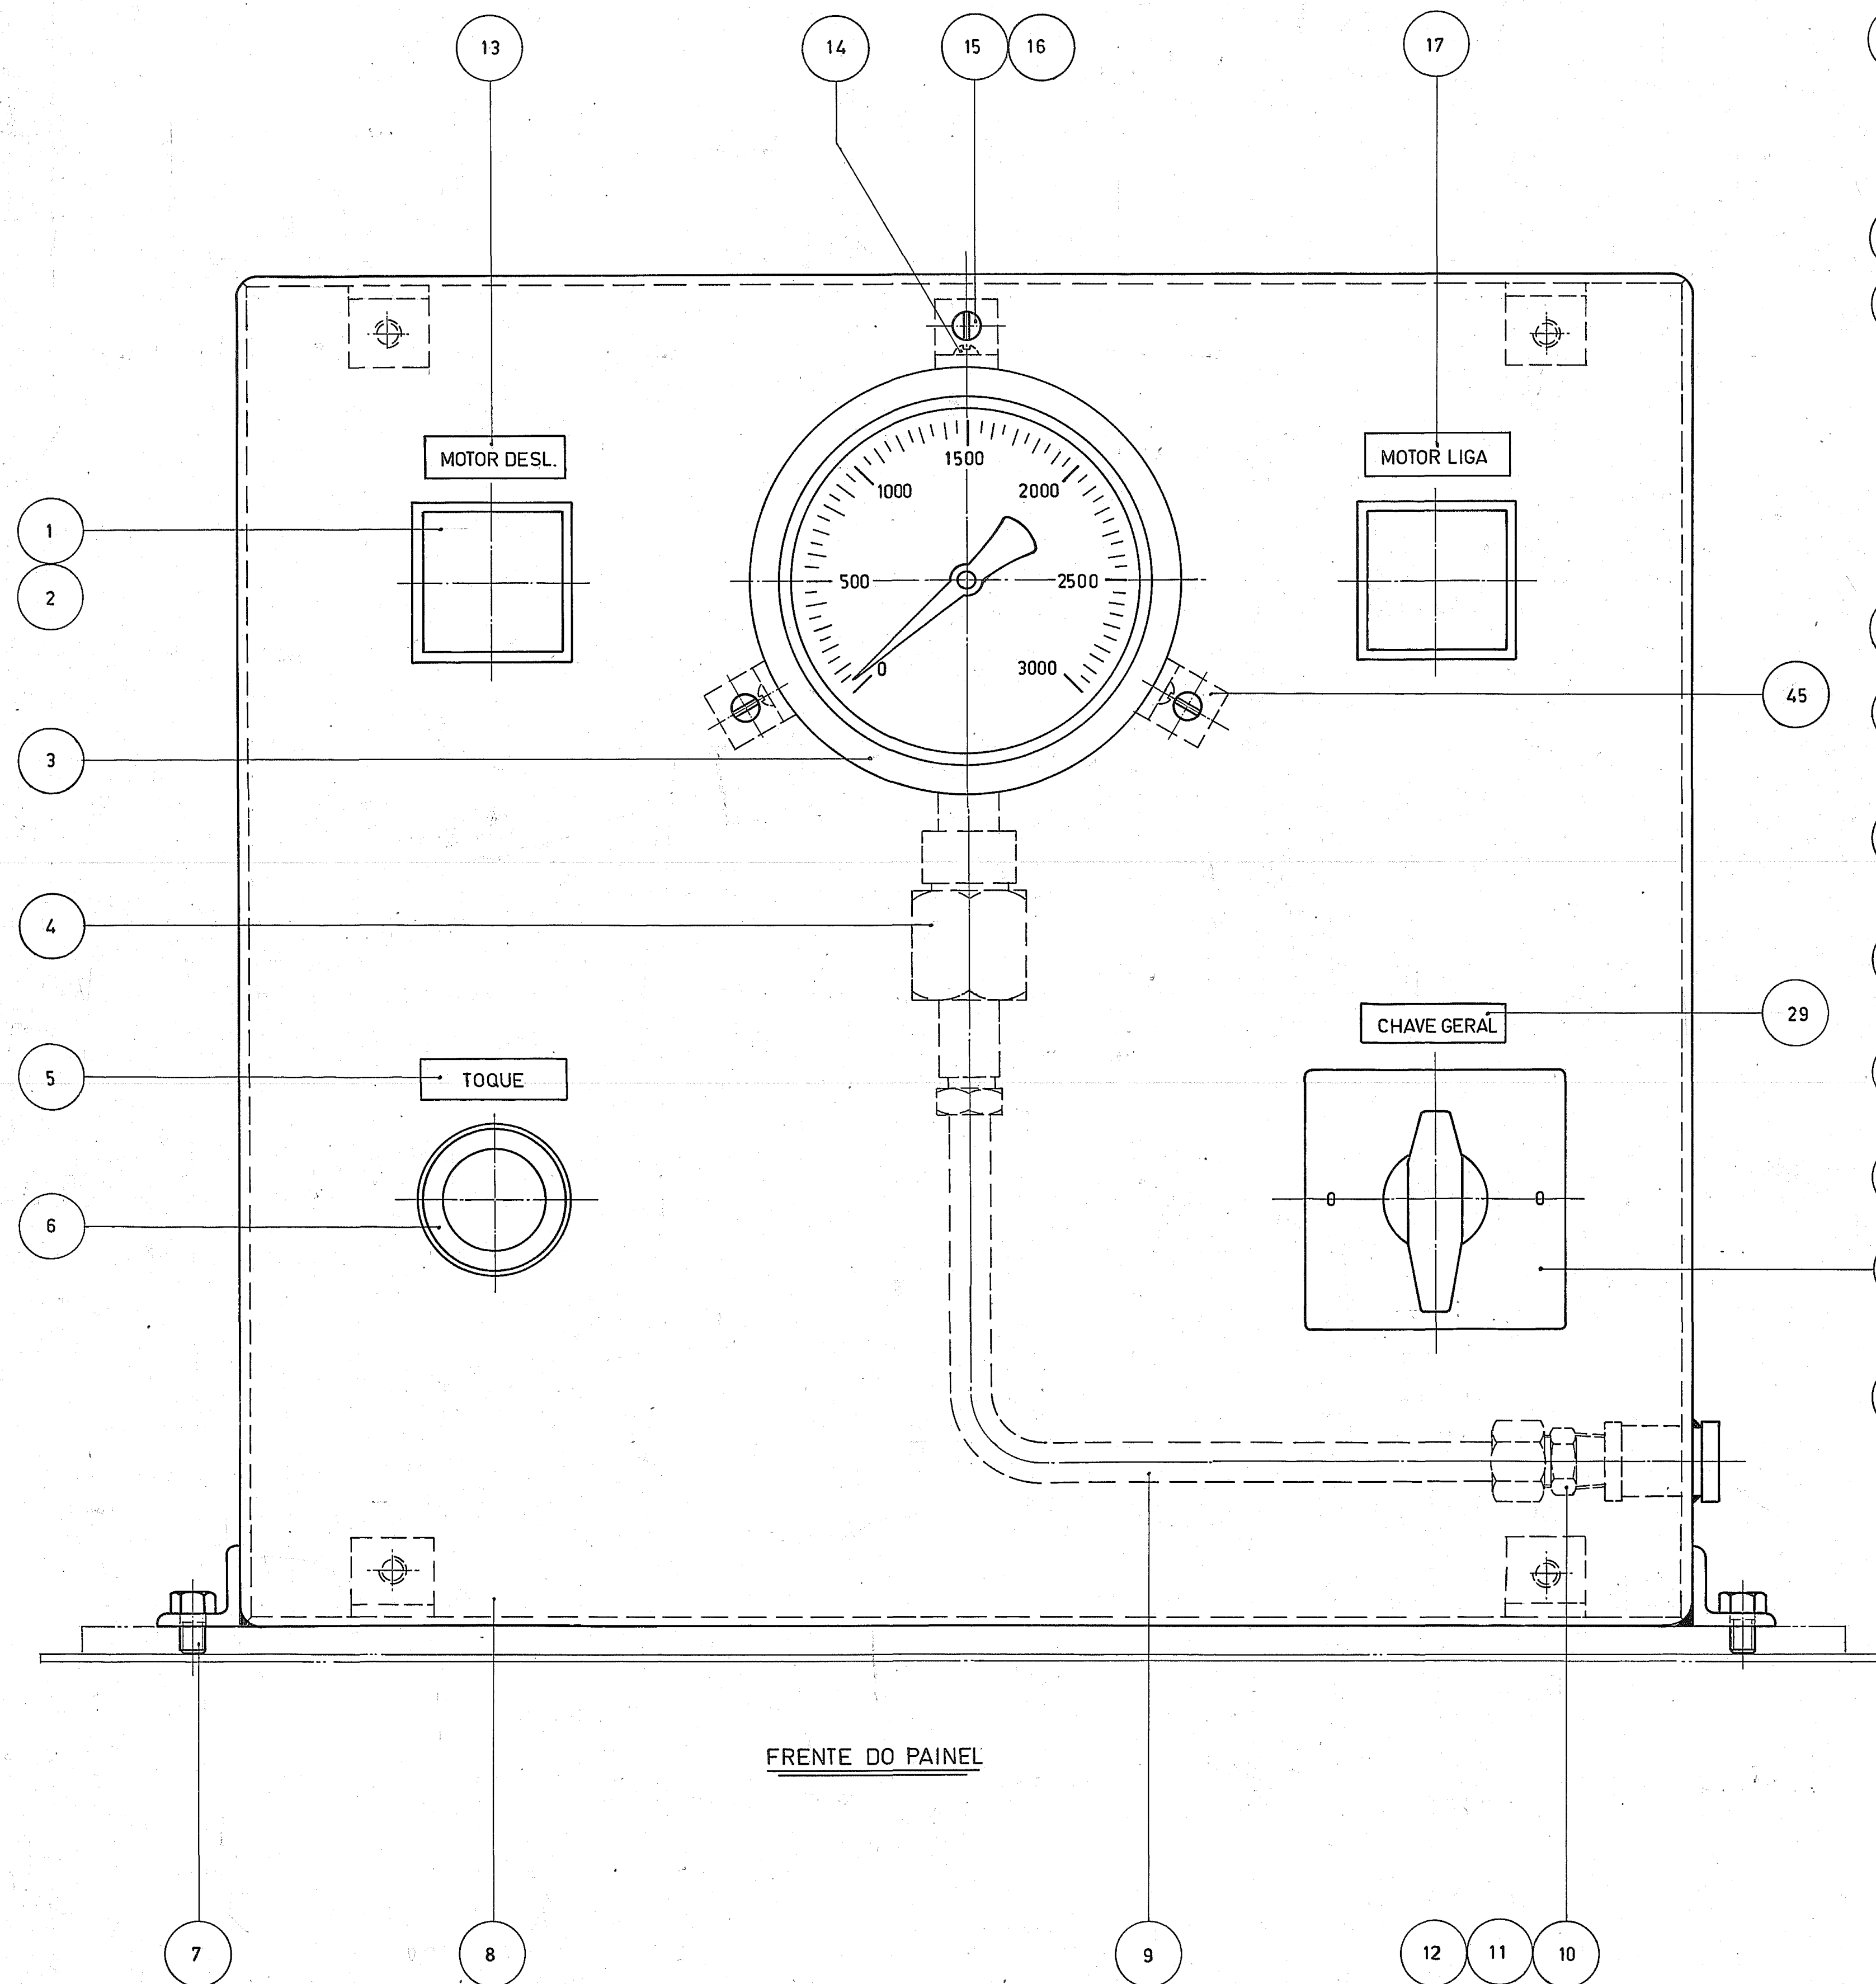

1	48	ESQUEMA ELÉTRICO	VVL-111-A-48	—	—
50	47	ABRACADEIRA INSULOK HELLERMANN	COMERCIAL	—	COD. T-18-R
1	46	CONDUITE FLEXIVEL	COMERCIAL	—	φ 9/8 x 60
3	45	SUPORTE DO MANÔMETRO	VVL-102-B-2	AÇO	—
1	44	FIO CABINHO FLEXIVEL 0,75mm (COR PRETA)	COMERCIAL	—	20 metros
1	43	FIO CABINHO FLEXIVEL 1,5mm (COR PRETA)	COMERCIAL	—	6 metros
3	42	BOX CURVO	COMERCIAL	—	φ 1/2
2	41	BLOCO FINAL SPRECHER SCHUH	COMERCIAL	—	COD. VRE-1-2,5mm ²
1	40	PLACA DE ESTREIMIDADE SPRECHER SCHUH	COMERCIAL	—	COD. VRE-1-2,5
1	39	TRILHO PARA FIXAÇÃO DE CONECTOR SPRECHER SCHUH	COMERCIAL	—	50 cm
13	38	CONECTOR SPRECHER SCHUH	COMERCIAL	—	COD. VRI-2,5 12,5 mm ²
1	37	FUSIVEL DIASED SIEMENS	COMERCIAL	—	2 AMP.
3	36	FUSIVEL DIASED SIEMENS	COMERCIAL	—	10 AMP.
4	35	TAMPA PARA BASE DIASED SIEMENS	COMERCIAL	—	COD. SSI-12
4	34	BASE DIASED SIEMENS	COMERCIAL	—	COD. SS F1002-B
4	33	COBERTURA P/ BASE DIASED SIEMENS	COMERCIAL	—	COD. SS H2-02
1	32	RELE BIMETÁLICO SIEMENS	COMERCIAL	—	COD. 3A 0,50 IE 2,5 a 4 AMP.
1	31	TRILHO PARA FIXAÇÃO RÁPIDA SIEMENS	COMERCIAL	—	50 cm
1	30	TAMPA	VVL-111-A-9	AÇO	—
1	29	PLACA INDICADORA (C. GERAL)	COMERCIAL	—	LARG. 10 mm
1	28	CHAVE PACO ACE	COMERCIAL	—	COD. P16-1/3 HS
50	27	TERMINAIS AMP	COMERCIAL	—	COD. 16S075
15	26	TERMINAIS AMP	COMERCIAL	—	COD. 13 05 78
50	25	TERMINAIS AMP	COMERCIAL	—	COD. 16S012
1	24	CONTATOR SIEMENS	COMERCIAL	—	COD. 319 41-1V2-0A
12	23	PARAF. CAB. REDONDA	COMERCIAL	AÇO	φ 3/32 NCx 1/4

REDES. 08-04-87

1	22	SUPORTE DO TEMPORIZADOR	VVL-111-A-22	AÇO	—
1	21	CALHA PLÁSTICA HELLERMANN	COMERCIAL	—	COD. HD-2P 50 cm
1	20	TEMPORIZADOR COEL	COMERCIAL	—	LINHA PC 0 A 180 SEG.
1	19	TEMPORIZADOR COEL	COMERCIAL	—	LINHA PE 0 A 30 min.
4	18	PARAF. CABECA REDONDA	COMERCIAL	AÇO	φ 1/2 NCx 3/8
1	17	PLAQUETA INDICADORA (LIGA)	COMERCIAL	—	LARG. 10 mm
3	16	PORCA SEXT.	COMERCIAL	AÇO	Nº 10 NC
3	15	PARAF. CAB. REDOND.	COMERCIAL	AÇO	Nº 10 NCx 1/2
3	14	PARAF. CAB. REDONDA	COMERCIAL	AÇO	Nº 5 x 1/4
1	13	PLAQUETA INDICADORA (DESL.)	COMERCIAL	—	LARG. 10 mm
1	12	PORCA DE COMPRESSÃO	COMERCIAL VCL-54	LATÃO	φ 3/8 TUBO
1	11	ANEL	COMERCIAL VCL-05	LATÃO	φ 3/8 T
1	10	UNIÃO DE COMPRESSÃO	COMERCIAL VCL-10S	LATÃO	φ 1/4 NPTx 3/8 T.
1	9	TUBO DE COBRE	COMERCIAL	COBRE	φ 3/8
1	8	CAIXA	VVL-111-A-21	AÇO	—
4	7	PARAF. CAB. SEXT.	COMERCIAL	AÇO	φ 1/4 NCx 3/8
1	6	BOTÃO DE COMANDO TIPO COGUMELO	COMERCIAL	—	BLINDEX 4A70211 V.D.
1	5	PLAQUETA INDICADORA (TOQUE)	COMERCIAL	—	LARG. 10 mm
1	4	CONECTOR FEMEA 1/2 NPTx 3/8 TUBO	COMERCIAL VCL-113	LATÃO	Nº 768-FB (DETROIT)
1	3	MANÔMETRO φ 4" 1/2 NPT SAÍDA NA VERTICAL	COMERCIAL	—	3000 lbs x pol.2
2	2	LAMP. DE FILAM. 6W-260 V	COMERCIAL	—	TIPO BAIXA-NETA 2P
2	1	SINALEIRO 1 VERMELHO	COMERCIAL	—	BLINDEX 611/251
QTD.	POS.	DENOMINAÇÃO	PEÇA Nº	MATERIAL	OBS.
1	GR. Nº	VIDROS VITON LTDA.			
1	DESCRIÇÃO DO GRUPO	PAINEL DE CONTROLE			
	TRAT. TERM.	—			
	ESCALA	1:1			
	DES.	—			