
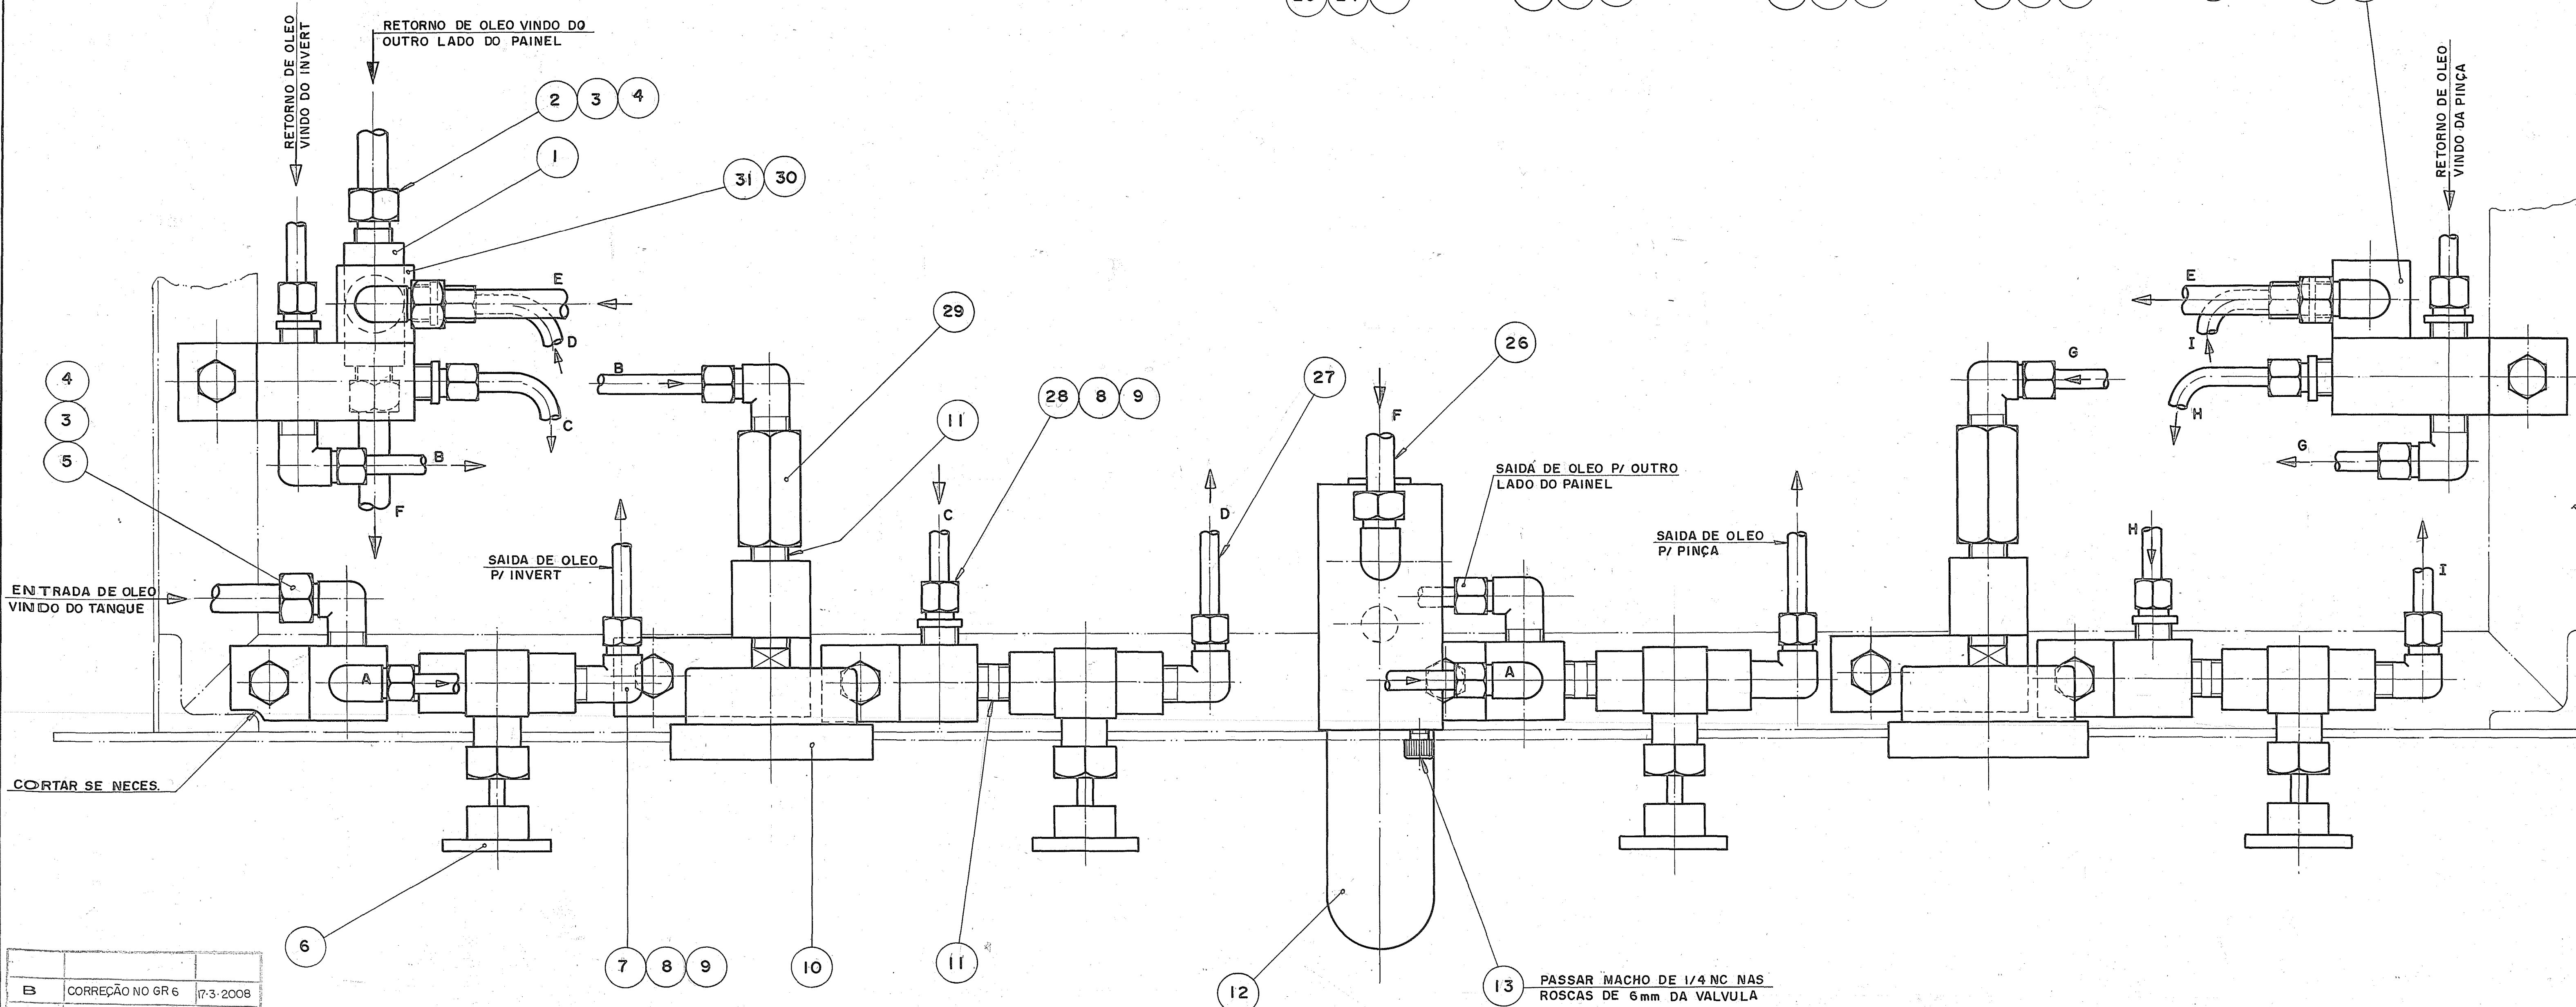


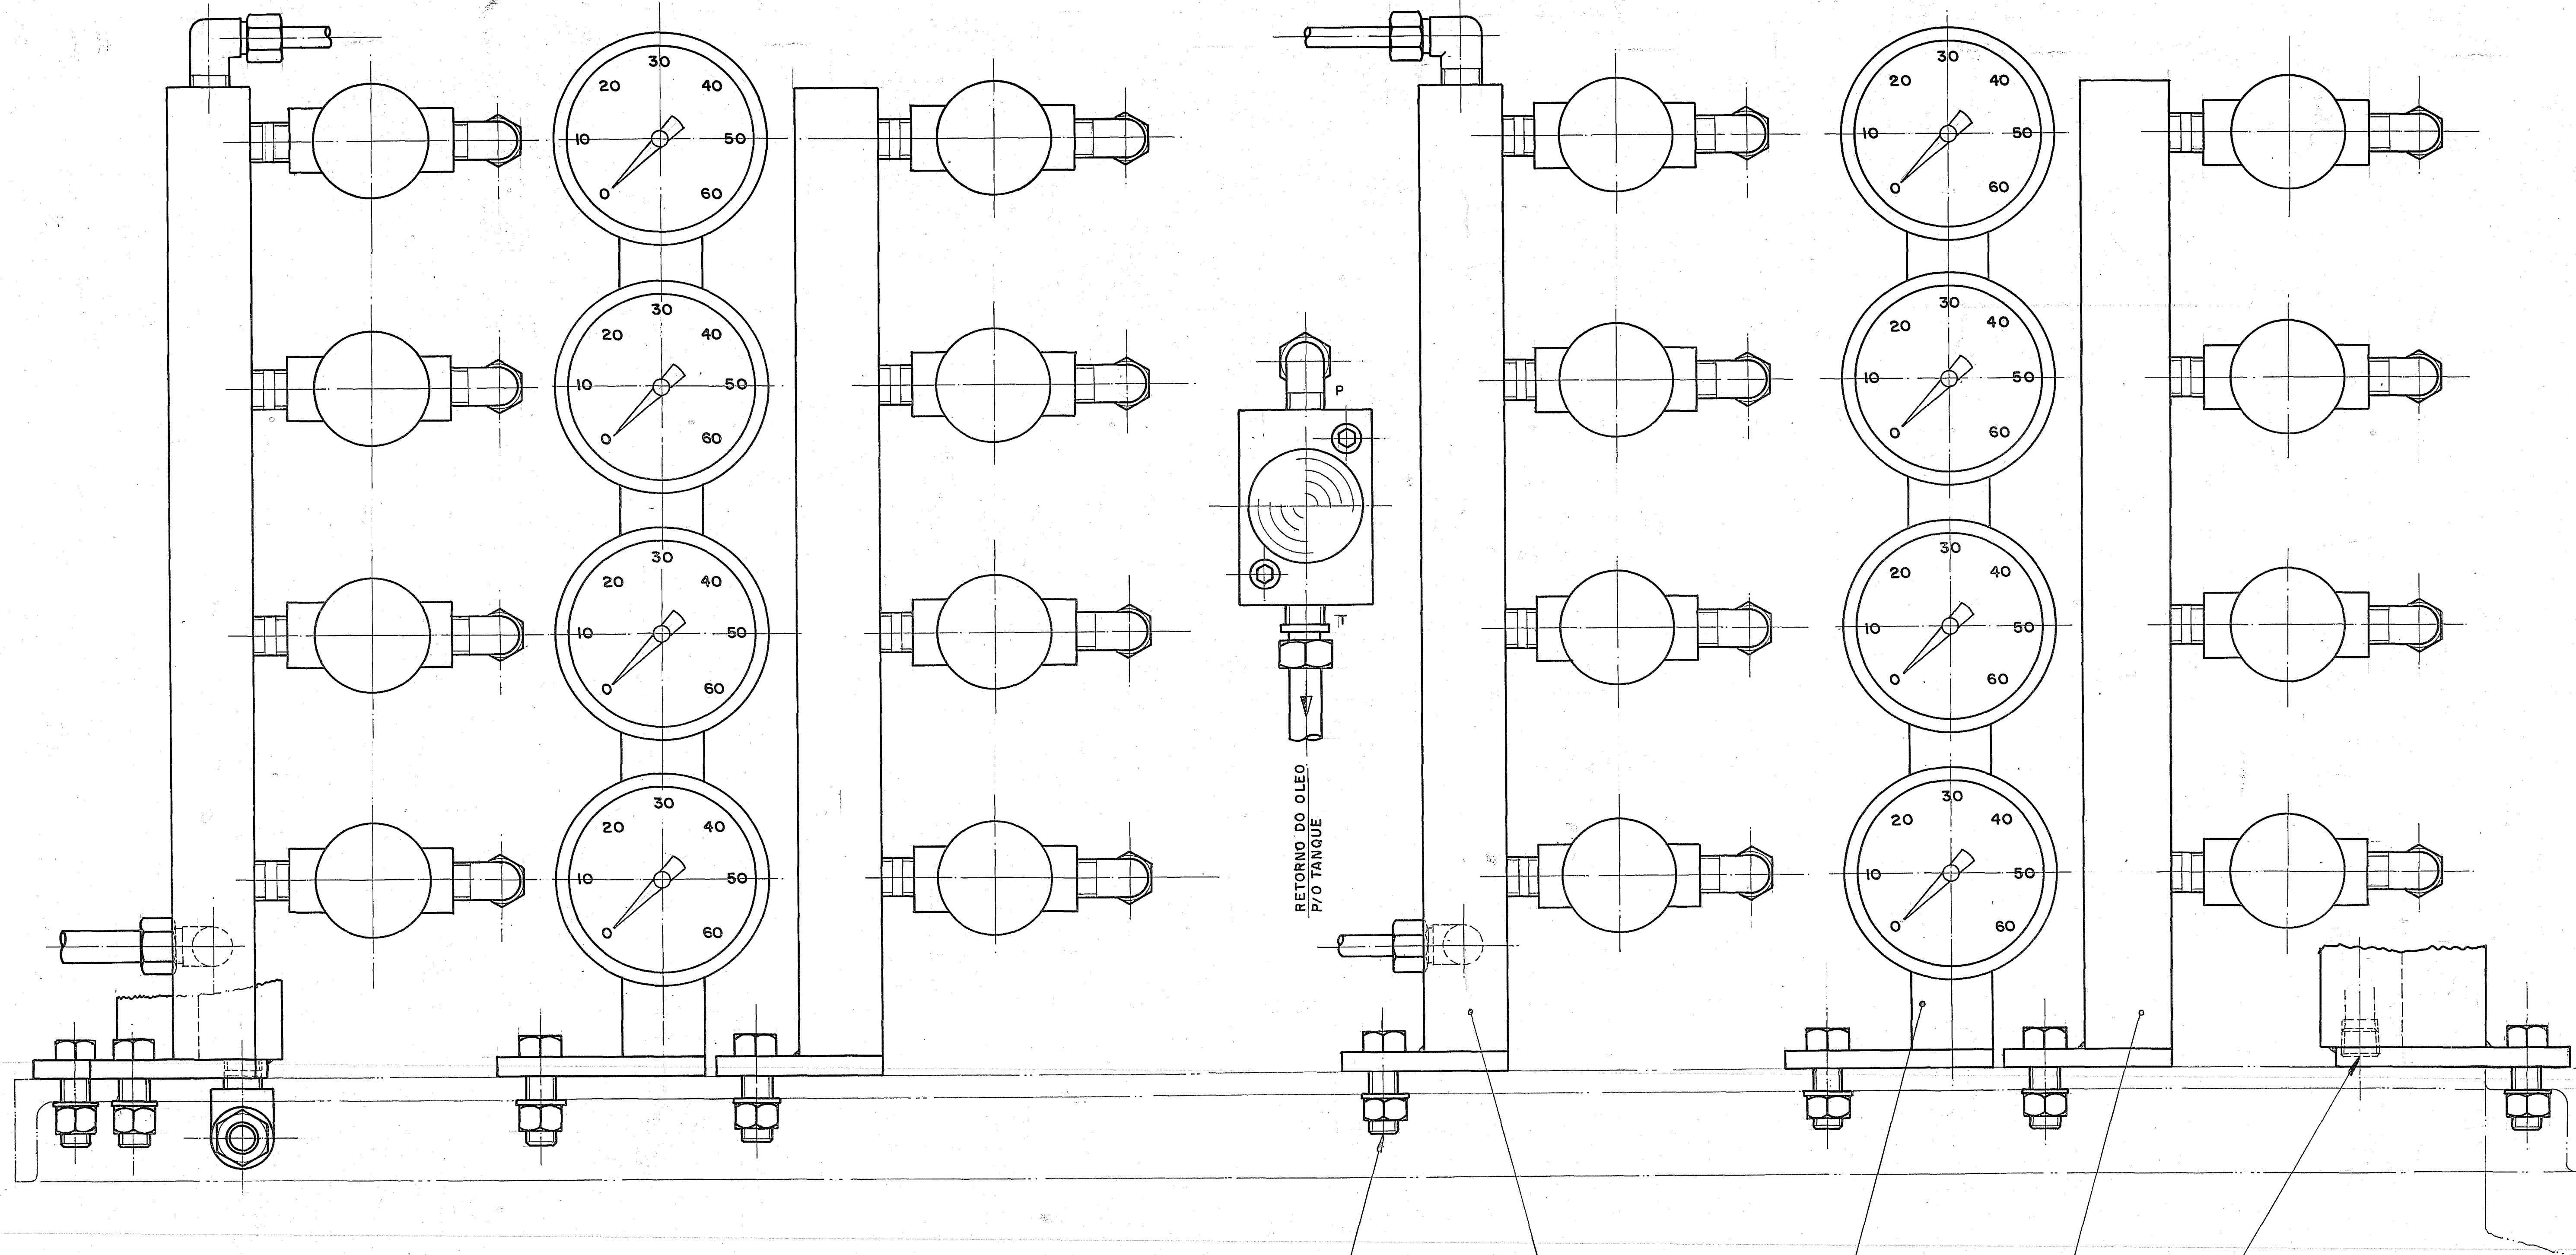

OBS:
AS QUANTIDADES SÃO PARA MÁQUINA
I.S. 6 & 6 SEÇ. COMPLETAS

OBS:
PAINEL MOSTRADO P/
MAQ. I.S. 6 SEÇ.

45					
44					
43					
42					
41					
40					
39					
38					
37					
36					
35					
2	2	34	BLOCO L.D.	VV-7241	AÇO
2	2	33	BLOCO L.D.	VV-7242	AÇO
2	2	32	BLOCO L.D.	VV-7243	AÇO
2	2	31	BLOCO L.E. & L.D.	VV-5420	AÇO
1	1	30	BLOCO L.E.	VV-5419	AÇO
16	12	29	AMORTECEDOR DE GOLPES	103-221	COMERCIAL
64	48	28	UNIAO COMP. 1/4 NPT x 1/4 T	103-221	COMERCIAL
1	1	27	TUBO 1/2		COMERCIAL
1	1	26	TUBO 3/8		COMERCIAL
16	16	25	ARRUELA DE PRESSÃO		COMERCIAL
16	16	24	PARAF. SEXTAVADA		COMERCIAL
16	16	23	PARAF. CAB. SEXT.		COMERCIAL
2	2	22	BLOCO DE 5 VIAS	VV-5418	AÇO
1	1	21	BLOCO DE 4 VIAS	VV-5417	AÇO
2	2	20	SUPORTE DO MANOMETRO	VV-5416	AÇO
1	1	19	SUPORTE DO MANOMETRO	VV-5415	AÇO
2	2	18	BLOCO DE 4 VIAS	VV-5414	AÇO
1	1	17	BLOCO DE 3 VIAS	VV-5413	AÇO
3	6	16	PLUG ALLEN 5/ CAB.		COMERCIAL
2	2	15	BLOCO L.D. & L.E.	VV-5412	AÇO
1	1	14	BLOCO L.D.	VV-5411	AÇO
2	2	13	PARAF. ALLEN C/ CAB.		COMERCIAL
1	1	12	VALVULA LIMITADORA DE PRES.		COMERCIAL
49	37	11	NIPLE 1/4 NPT x 1		COMERCIAL
16	12	10	MANOMETRO 603mm SAIDA		COMERCIAL
140	106	9	PORCA COMP. 1/4 T		COMERCIAL
140	106	8	ANEL DE COMP. 1/4 T		COMERCIAL
76	58	7	COTOV. COMP. 1/4 NPT x 1/4 T		COMERCIAL
32	24	6	VALVULA DE ASHLAND MINUTURA		COMERCIAL
7	7	5	COTOV. COMP. 1/4 NPT x 3/8 T		COMERCIAL
10	10	4	PORCA COMP. 3/8 T		COMERCIAL
10	10	3	ANEL COMP. 3/8 T		COMERCIAL
3	3	2	UNIAO COMP. 1/4 NPT x 3/8 T		COMERCIAL
1	1	1	TEE 1/4 NPT		COMERCIAL
QUANT.	POS.	DENOMINAÇÃO	PEÇA Nº	MATERIAL	OBS.
2	1	GR. Nº	VIDROS VITON LTDA.		
MAQ. I.S. 6 SEÇ. 1	MAQ. I.S. 6 SEÇ. 2	MAQ. I.S. 6 SEÇ. 3	MAQ. I.S. 6 SEÇ. 4	MAQ. I.S. 6 SEÇ. 5	MAQ. I.S. 6 SEÇ. 6
17-224	17-224	17-224	17-224	17-224	17-224
MODIFICAÇÕES	MODIFICAÇÕES	MODIFICAÇÕES	MODIFICAÇÕES	MODIFICAÇÕES	MODIFICAÇÕES
DATA	DATA	DATA	DATA	DATA	DATA