
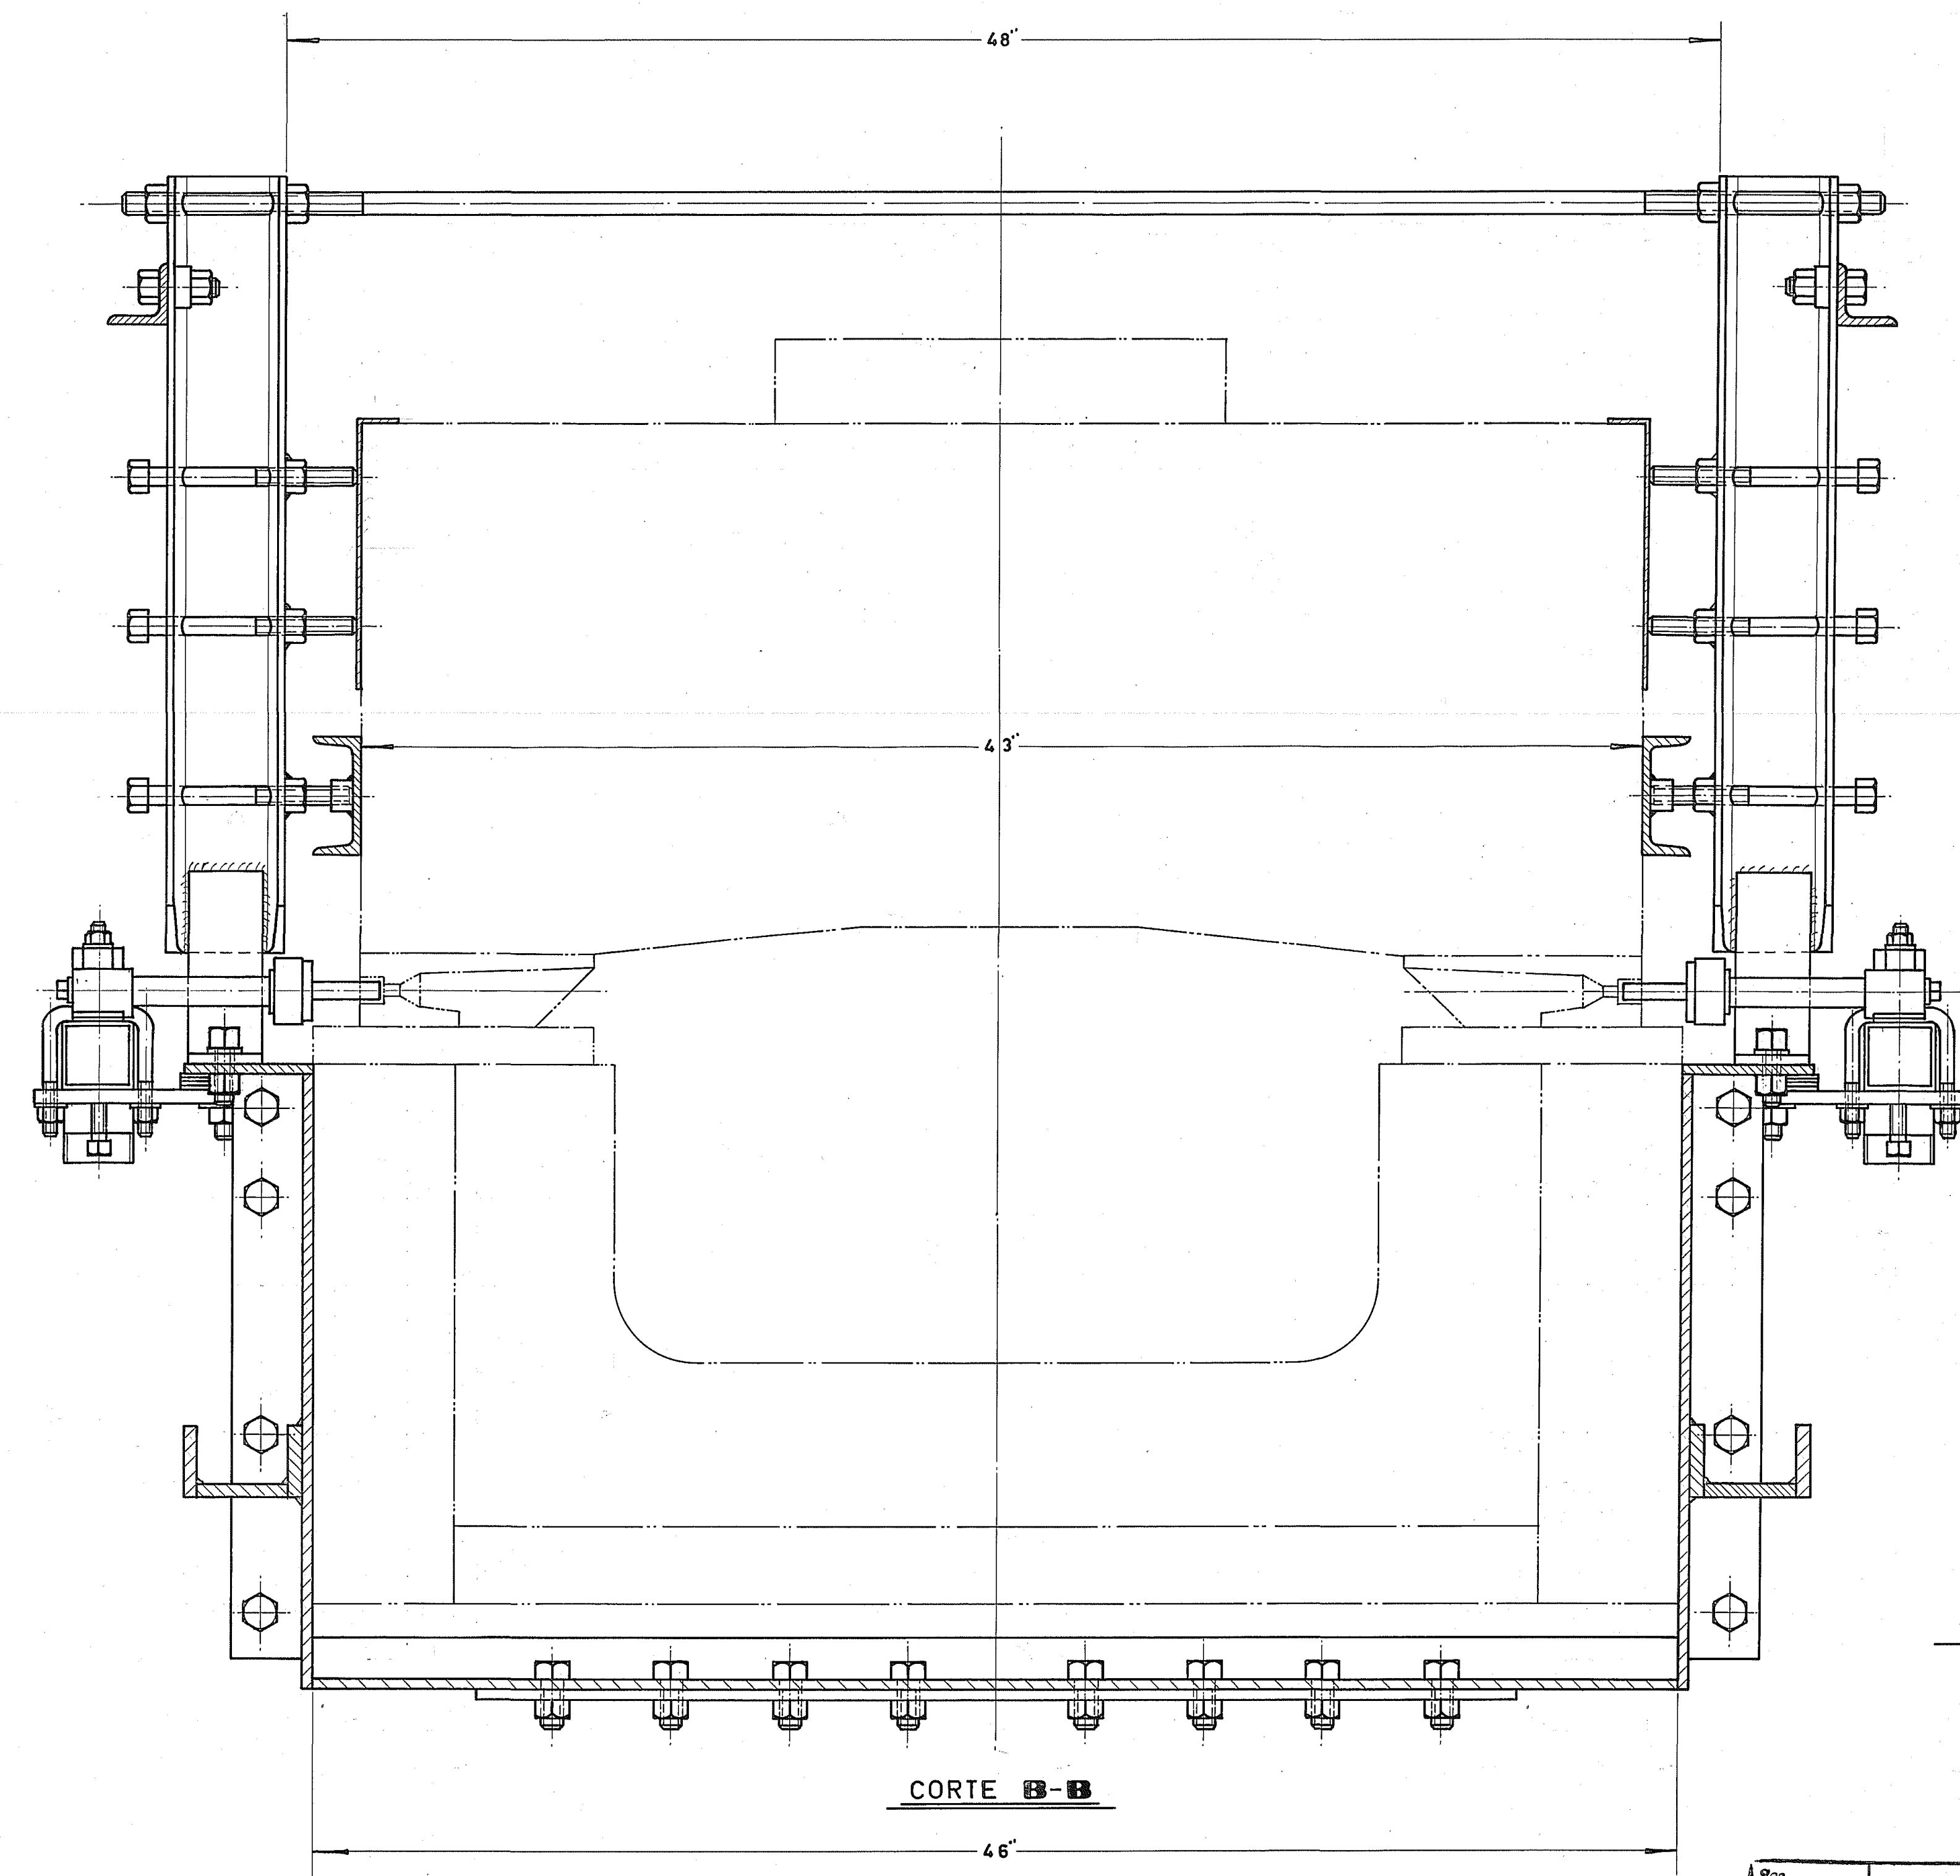


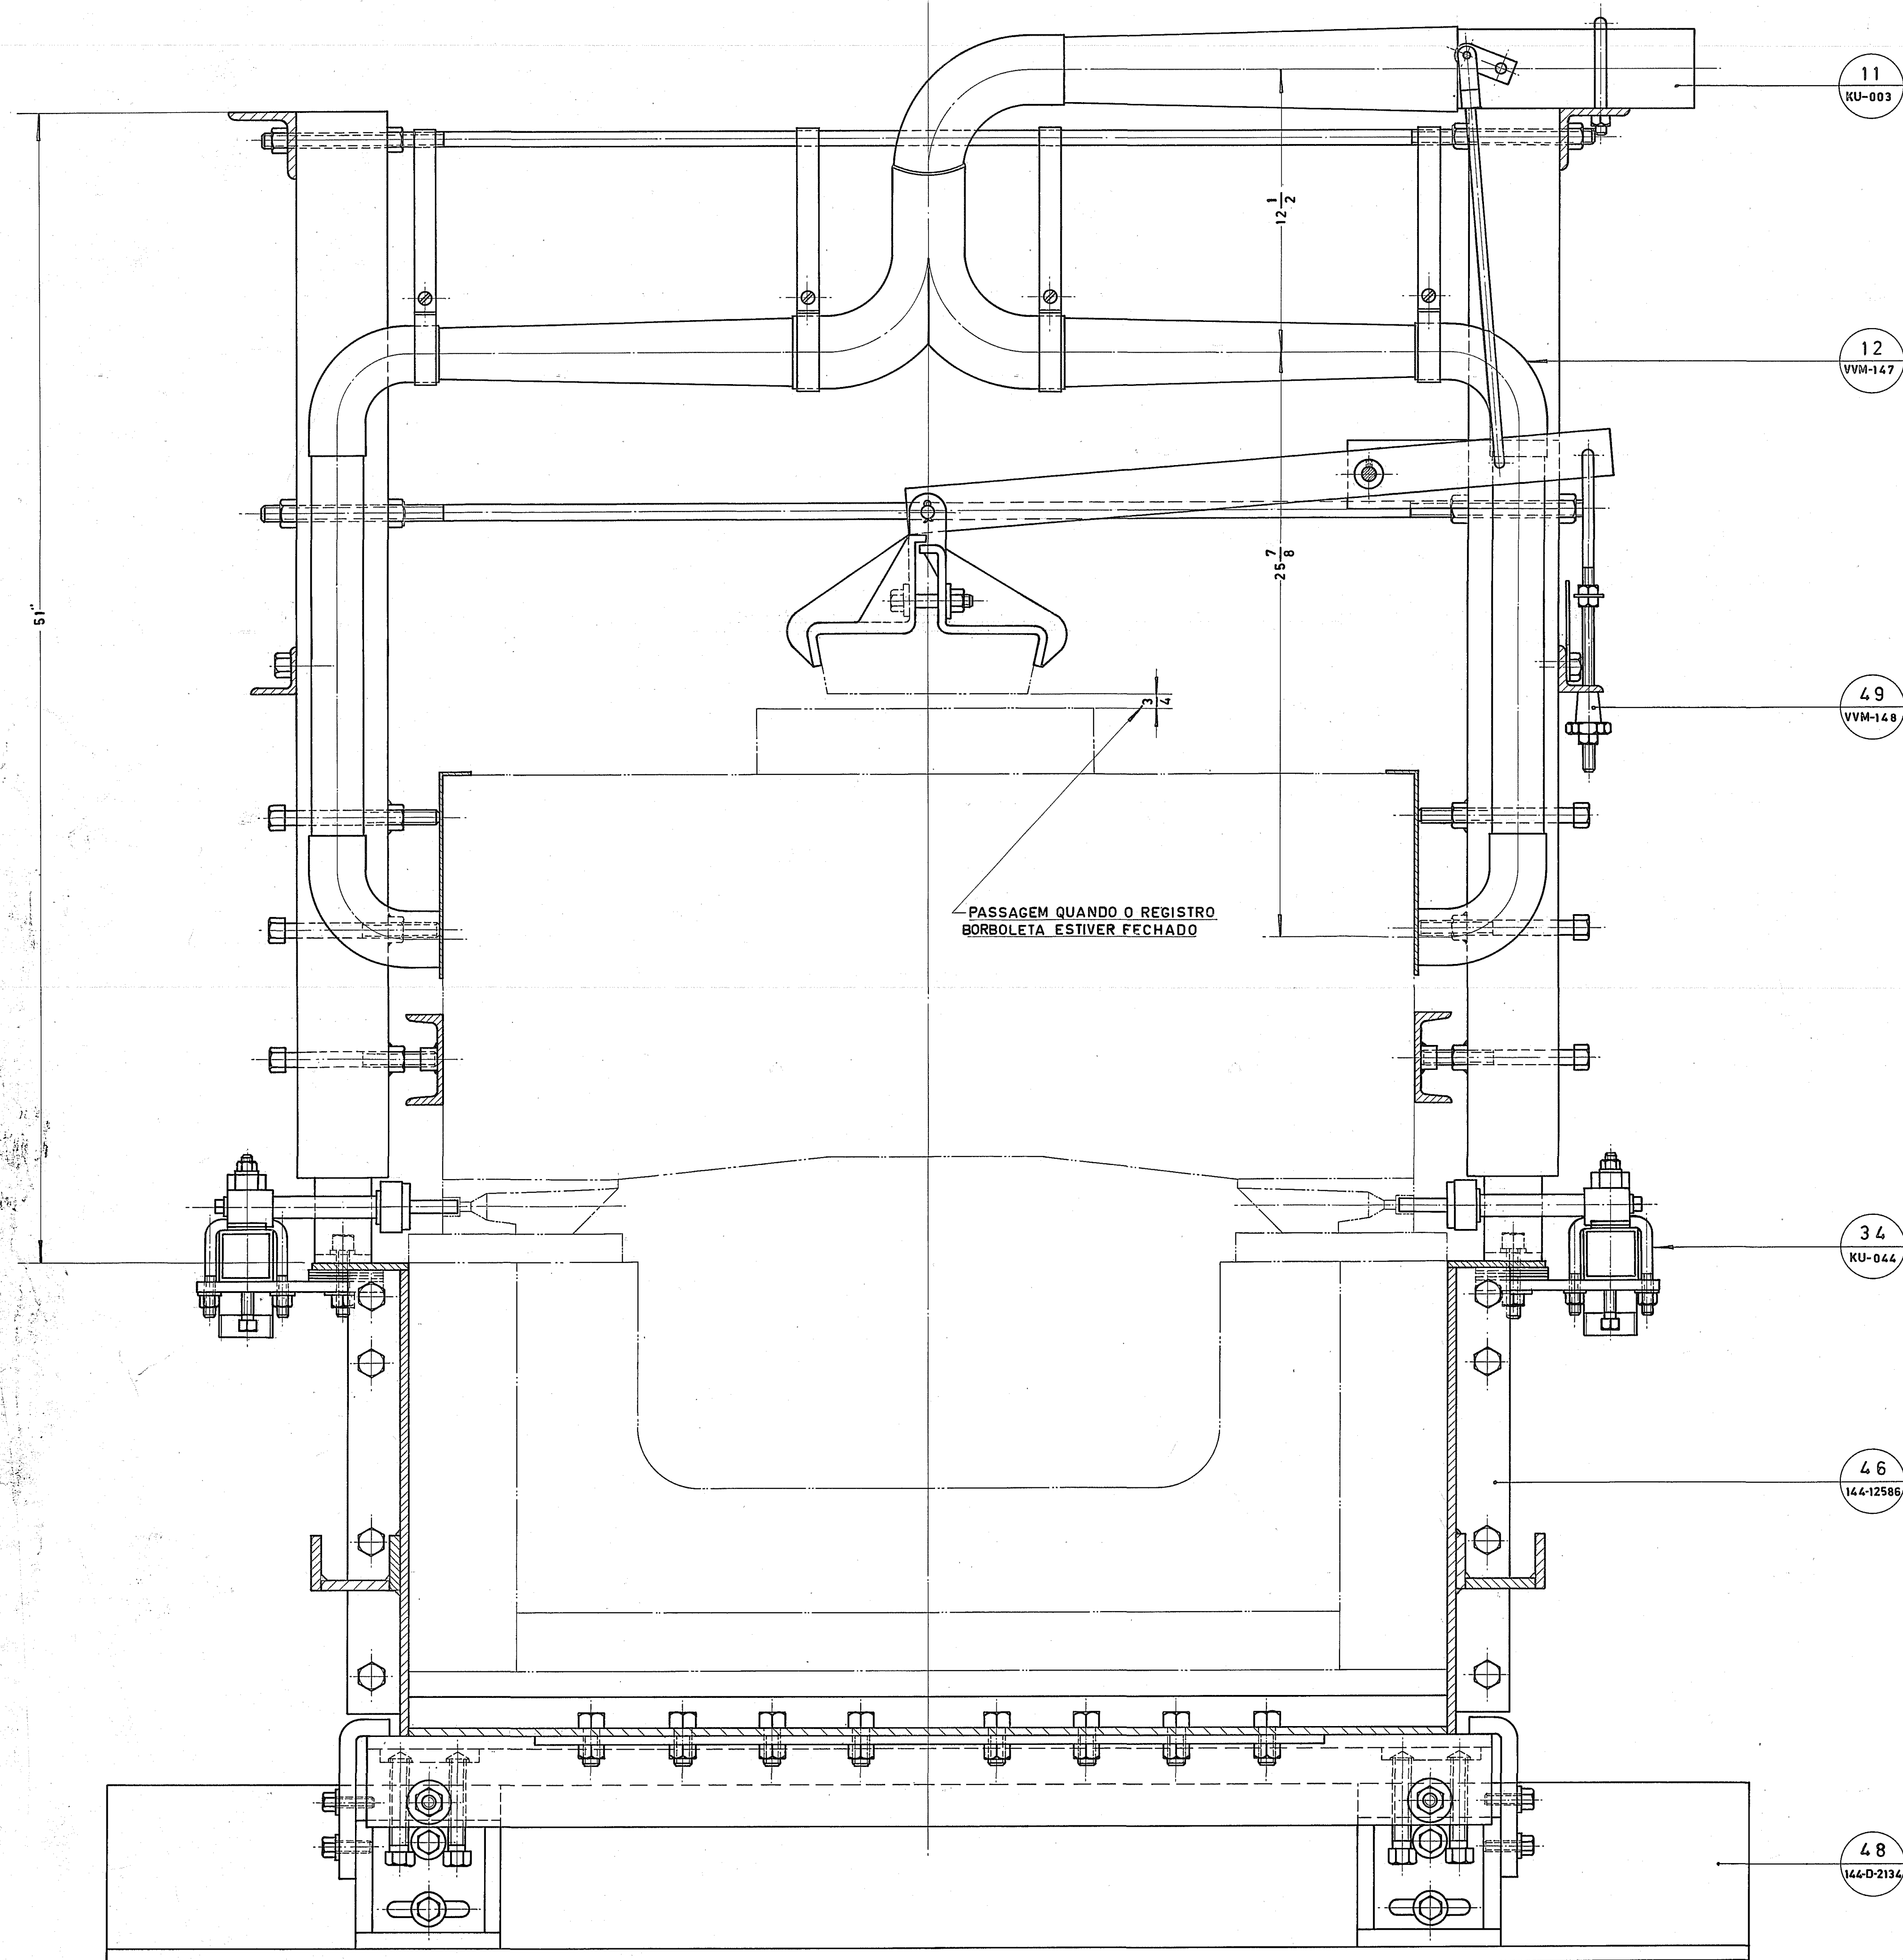

FOLHA 2 DE 2 F

Sec.	VIDROS VITON LTDA.	Data 10-4-79
Pag.		Dês. 24
Mat.		Escala Cop.
Conjunto	FEEDER KW 26-18' 7 1/2"	1/4 Verificação
Nome da Peça	CANAL DO FEEDER	Subst.
Tratam. Térmico	CONJ. GERAL (CORTE A-A E B-B)	Nº da VVM-146
		Peça
		Nº do Desenho