


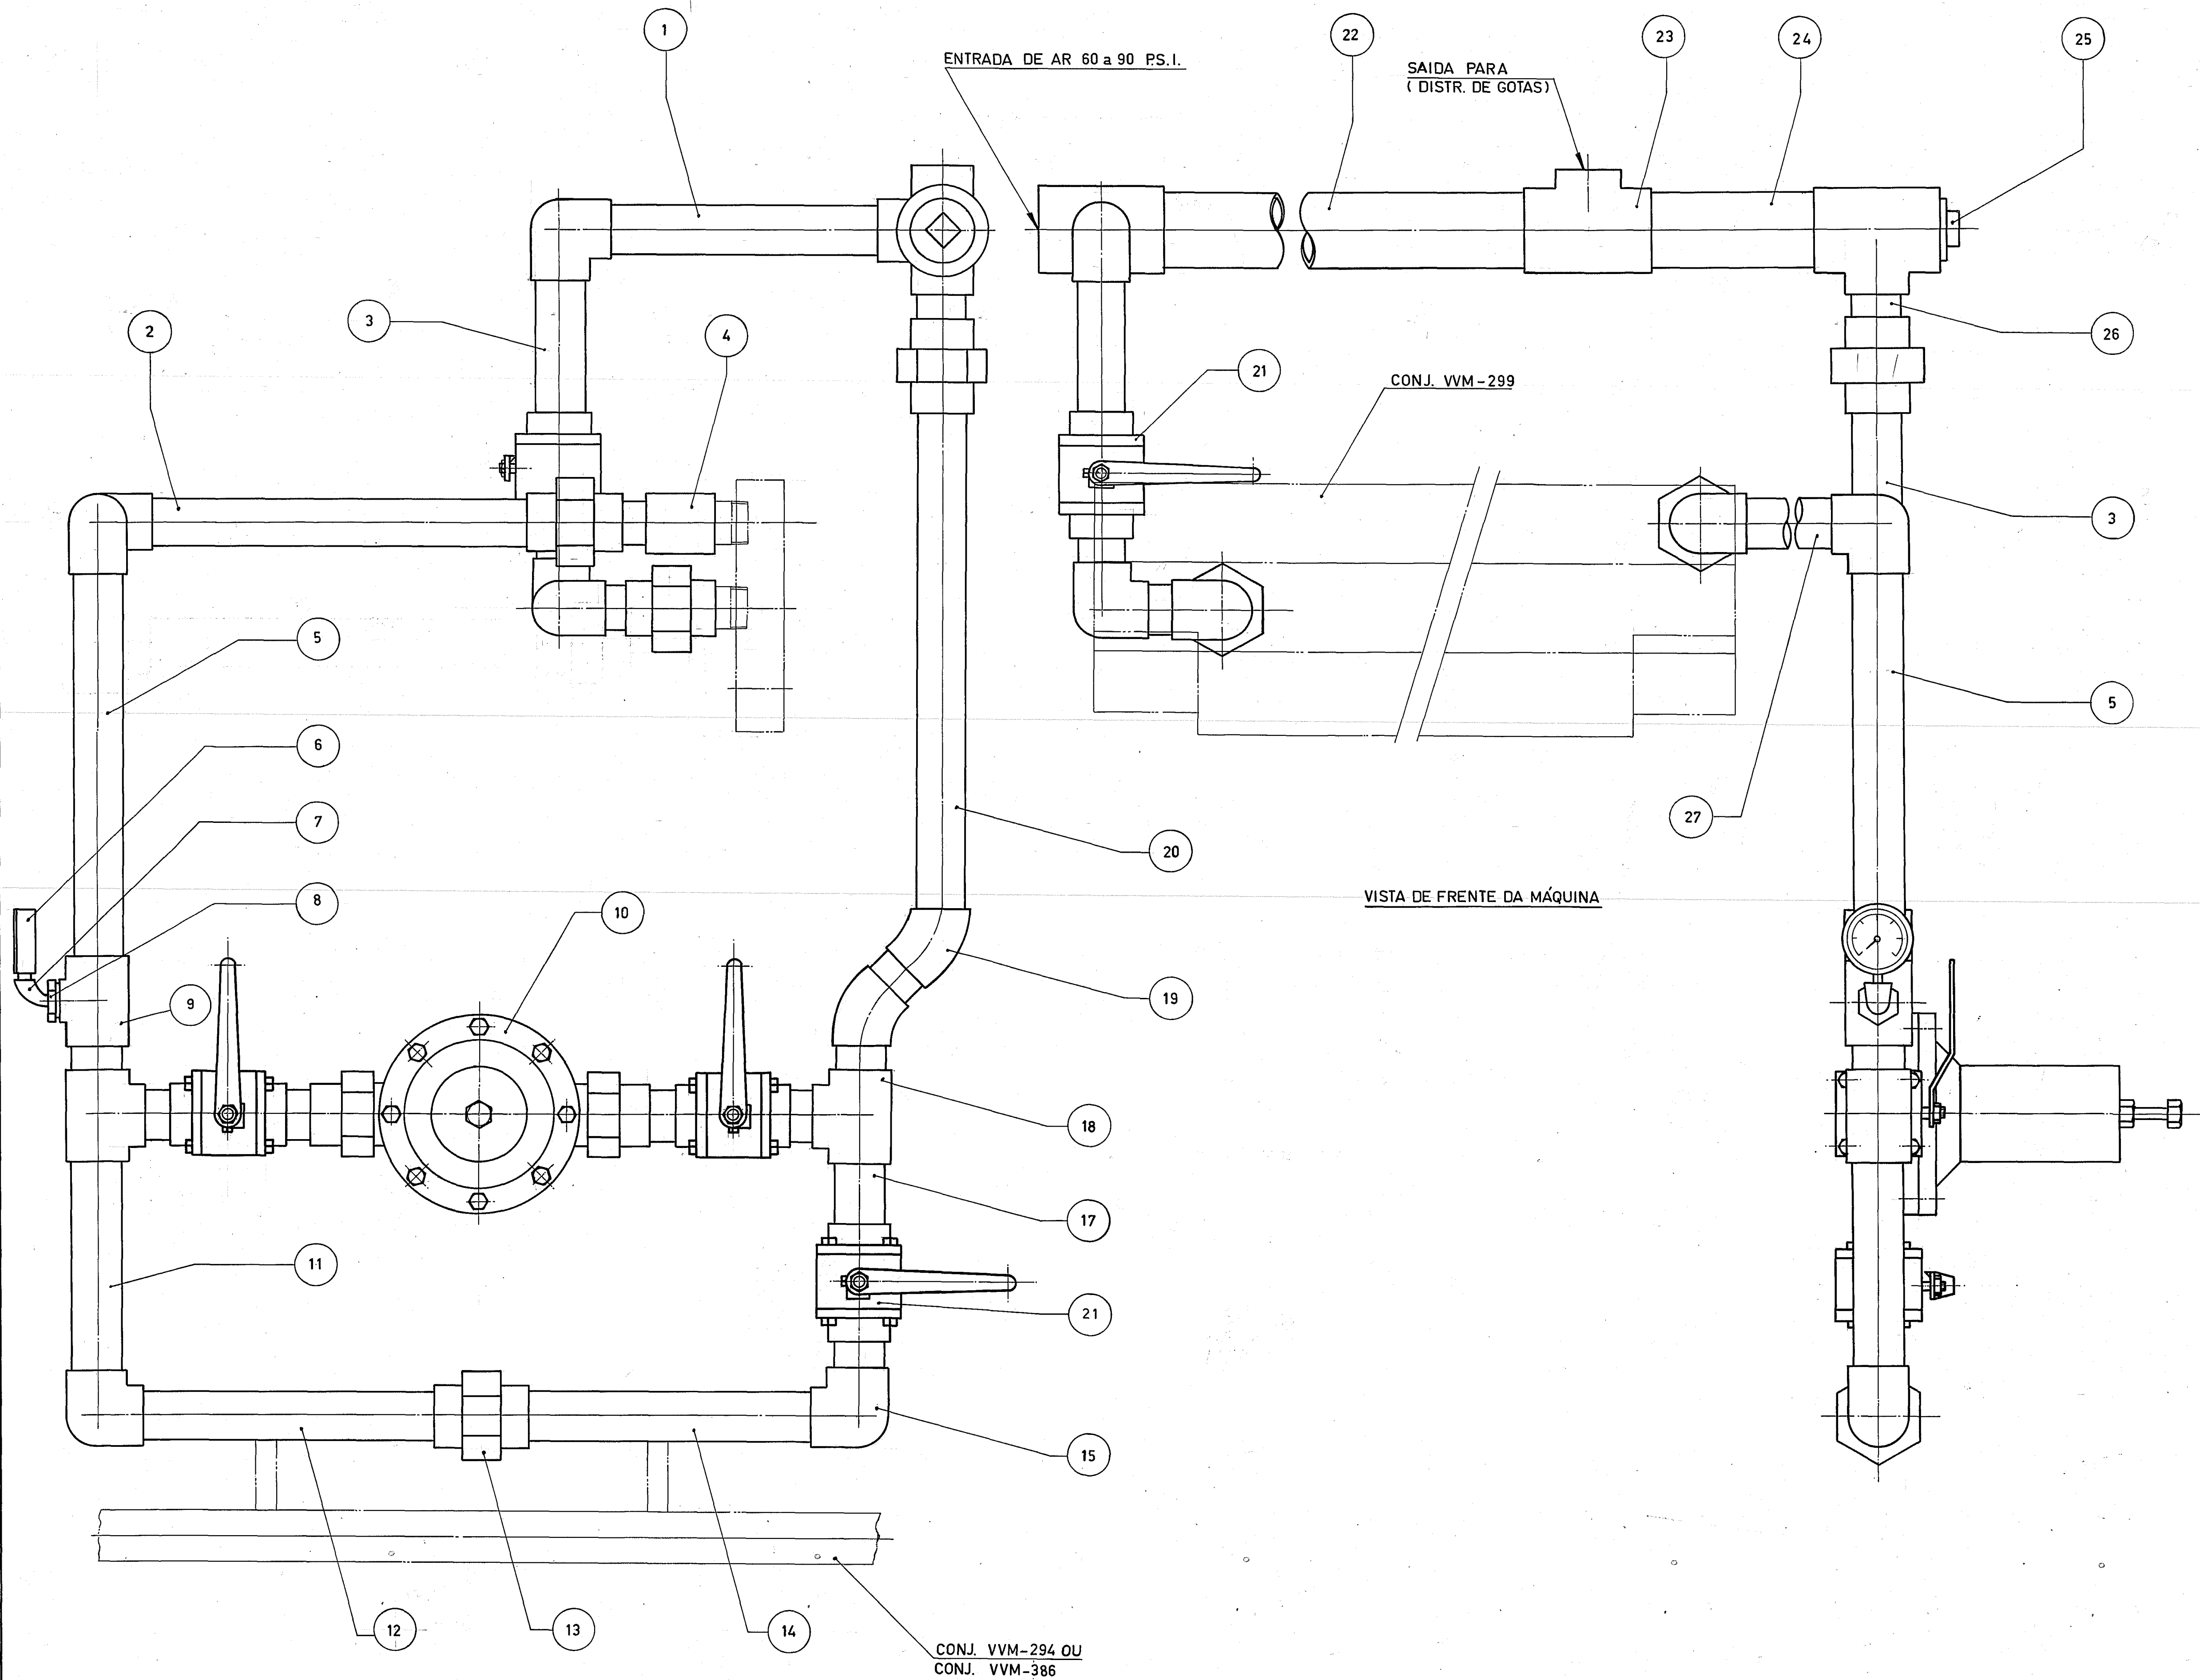

NOTA
VÁLVULA DE REGULAGEM DE PRESSÃO
MARCA I.V.C. TAG. 205-A-2
MOD. R.P. 10 2", MOLA 25 a 75 P.S.I.

1	27	CANO Ø 2 NPT x 18 1/2	COMERCIAL	F. GALV.	
13	26	NIPLE Ø 2 NPT x 2 1/2	COMERCIAL	F. GALV.	
1	25	PLUG Ø 3 NPT	COMERCIAL	F. GALV.	
1	24	NIPLE Ø 3 NPT x 9 1/2	COMERCIAL	F. GALV.	
3	23	TEE DE RED. Ø 3 NPT x 2 NPT	COMERCIAL	F. GALV.	
1	22	CANO Ø 3 NPT x 169	COMERCIAL	F. GALV.	
4	21	VALVULA ESFÉRICA Ø 2 NPT	COMERCIAL	—	WORCESTER REF. 446 T
1	20	CANO Ø 2 NPT x 24 1/4	COMERCIAL	F. GALV.	
2	19	COTOVELO 45º Ø 2 NPT	COMERCIAL	F. GALV.	
2	18	TEE Ø 2 NPT	COMERCIAL	F. GALV.	
1	17	NIPLE Ø 2 NPT x 4 1/2	COMERCIAL	F. GALV.	
	16				
7	15	COTOVELO 90º x 2 NPT	COMERCIAL	F. GALV.	
1	14	CANO Ø 2 NPT x 14 1/2	COMERCIAL	F. GALV.	
6	13	UNIÃO DE Ø 2 NPT	COMERCIAL	F. GALV.	
1	12	CANO Ø 2 NPT x 15"	COMERCIAL	F. CALV.	
1	11	CANO Ø 2 NPT x 11 1/2	COMERCIAL	F. GALV.	
1	10	VALVULA DE REG. DE PRESSAO Ø 2 NPT	COMERCIAL	—	VIDE ANOT.
1	9	TEE DE Ø 2 NPT x 3/4 NPT	COMERCIAL	F. GALV.	
1	8	BUCHA DE RED. Ø 3/4 NPT x 1/4 NPT	COMERCIAL	F. GALV.	
1	7	COTOVELO 90º TIPO CACHIMBO Ø 1/4 NPT	COMERCIAL	F. GALV.	
1	6	MANÔMETRO DE 0 a 60 lbs/pl ²	COMERCIAL	—	FMB Ø 1/4 NPT
1	5	CANO Ø 2 NPT x 19 1/2	COMERCIAL	F. GALV.	
1	4	LUVA Ø 2 NPT	COMERCIAL	F. GALV.	
1	3	NIPLE Ø 2 NPT x 7 1/2	COMERCIAL	F. GALV.	
1	2	CANO Ø 2 NPT x 25 1/2	COMERCIAL	F. GALV.	
1	1	CANO Ø 2 NPT x 13 1/2	COMERCIAL	F. GALV.	
QNT.	POS.	DENOMINAÇÃO	PEÇA Nº	MATERIAL	OBS.
1	GR Nº	VIDROS VITON LT.			<i>Assinatura</i> 07-08-85
	DESCRIÇÃO DO GRUPO	MNT: MAQ. I.S. 8 SEÇÕES ENCANAMENTO GERAL ENCANAMENTO DE AR PARA ASSENTAMENTO DO INJETOR		VVM-295	
	DATA	ESCALA 1/4"	07-30		