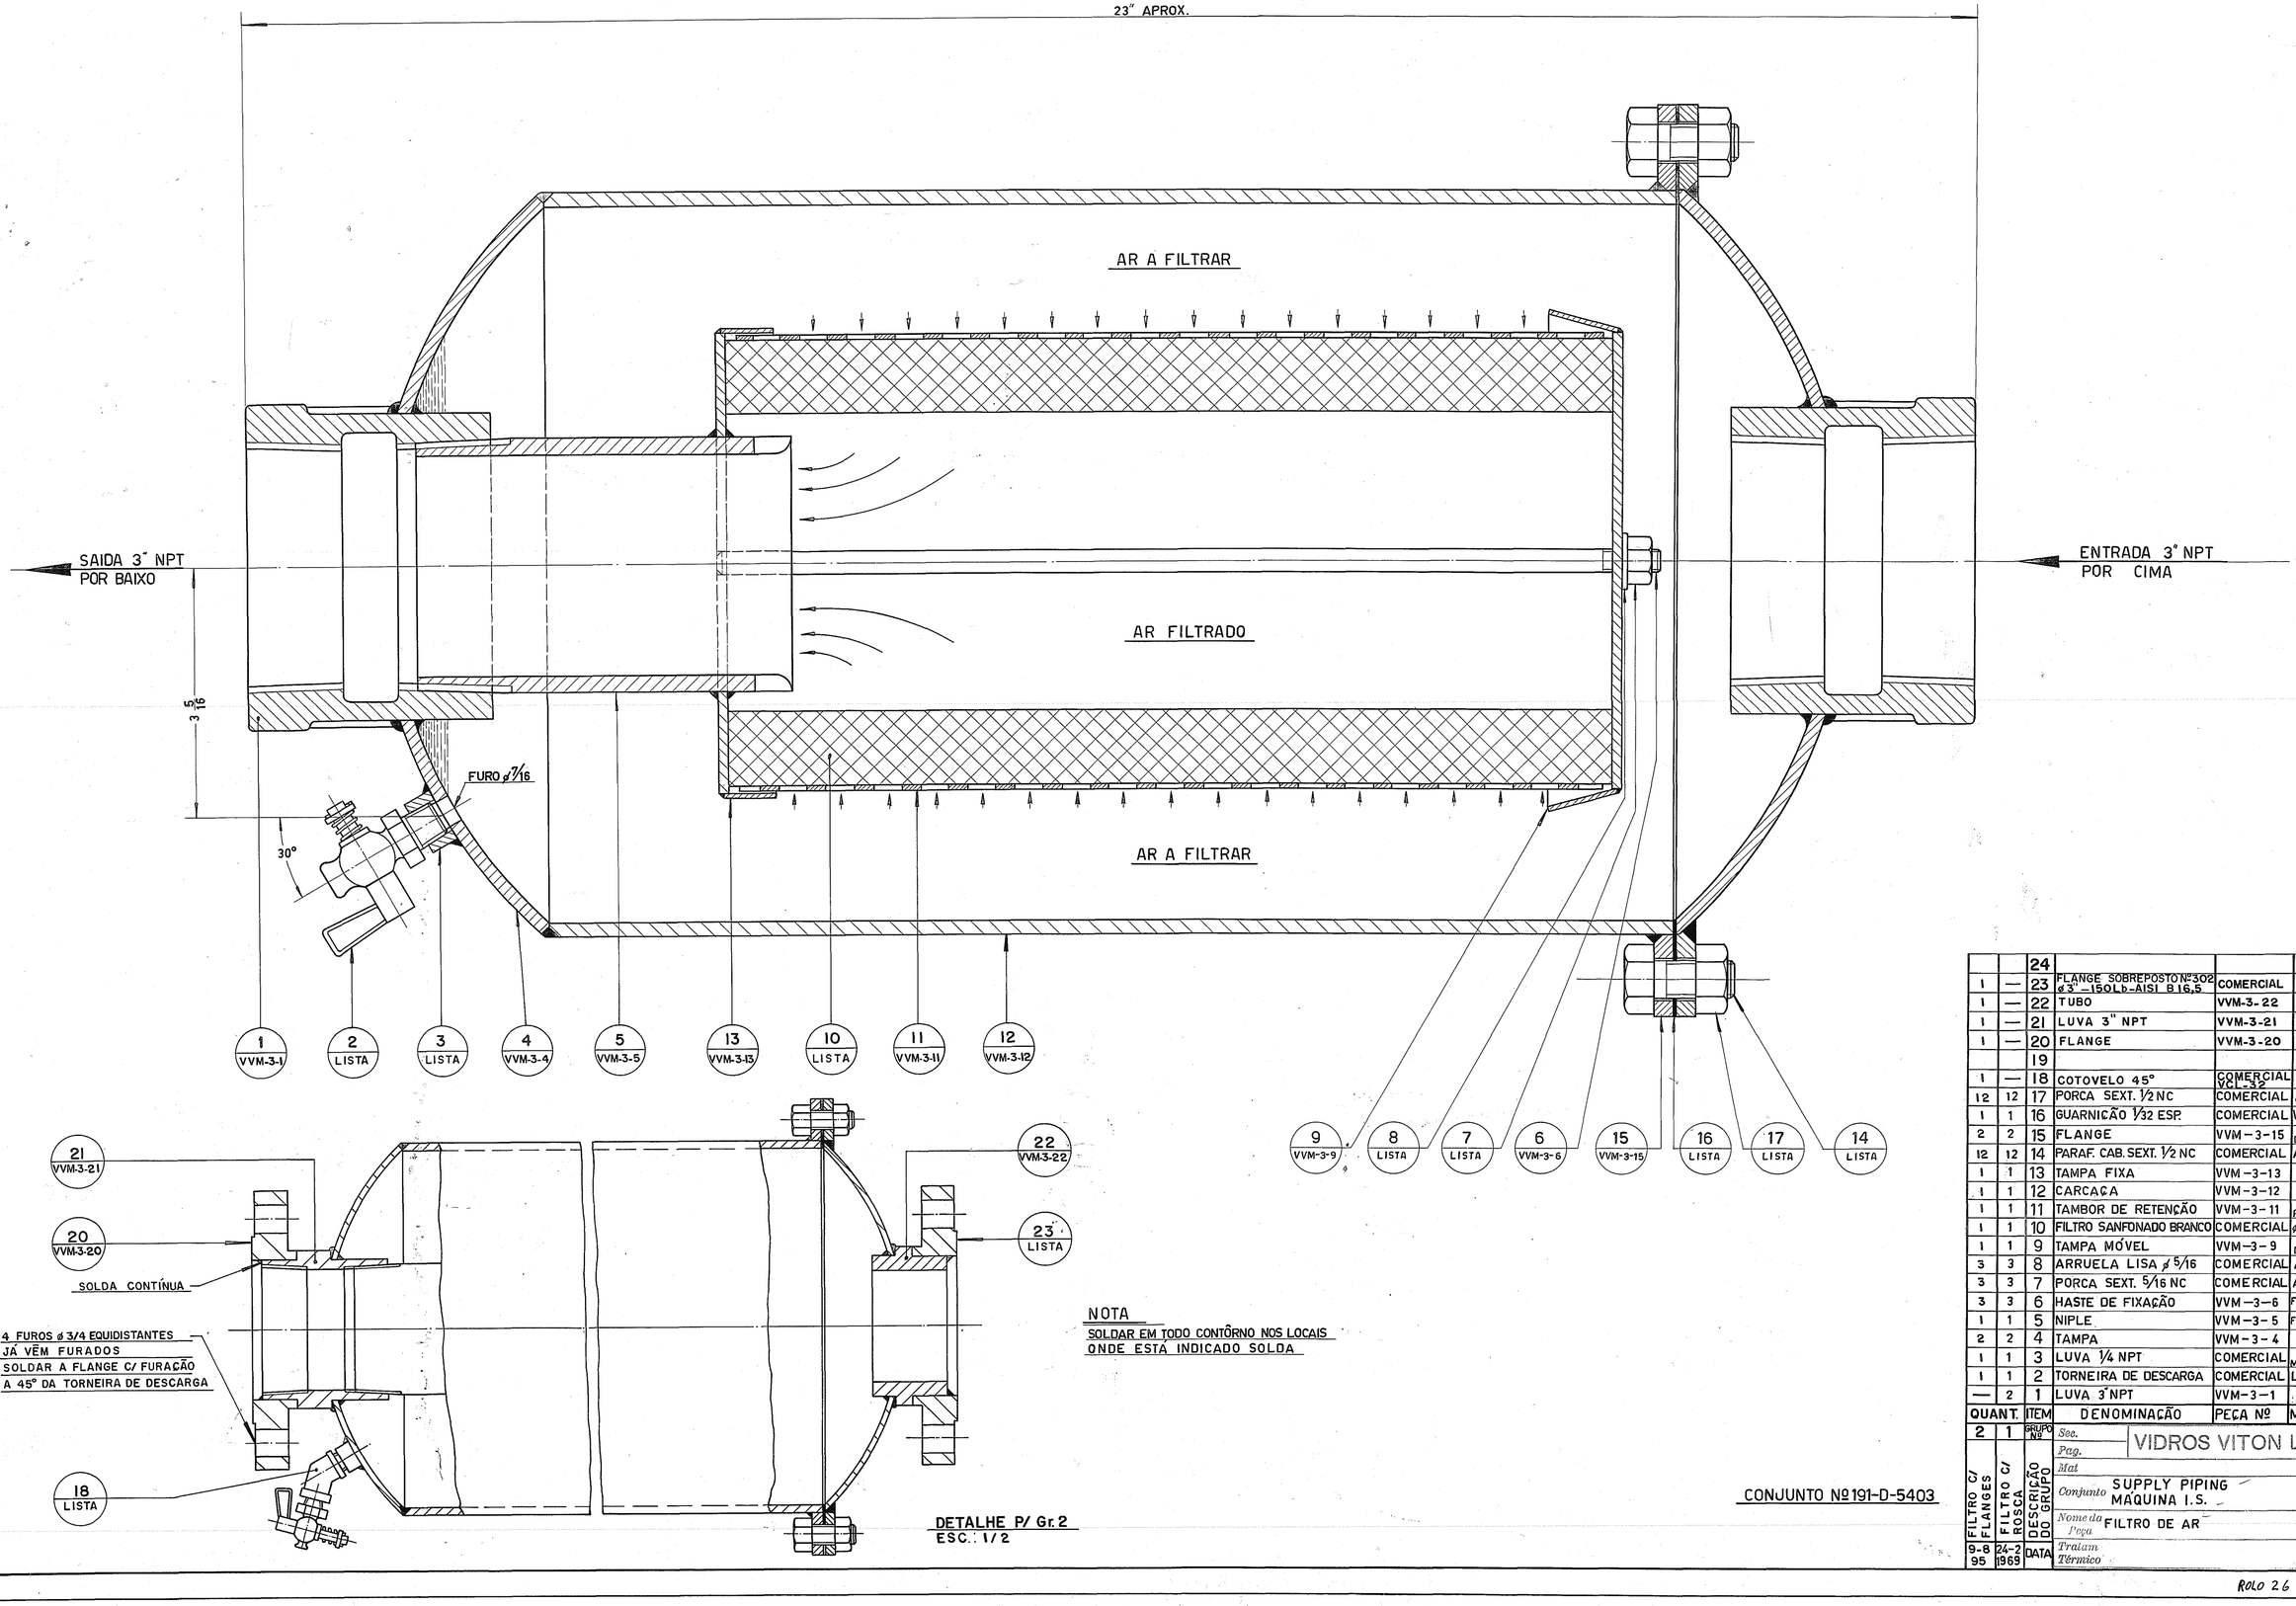

NOTA
SOLDAR EM TODO CONTÔRNO NOS LOCAIS
ONDE ESTÁ INDICADO SOLDA

DETALHE P/ Gr. 2
ESC.: 1/2

		24				
1	—	23	FLANGE SOBREPOSTO Nº302 ø 3" – 150Lb-AISI B 16,5	COMERCIAL	AÇO	
1	—	22	TUBO	VVM-3-22	〃	
1	—	21	LUVA 3" NPT	VVM-3-21	〃	
1	—	20	FLANGE	VVM-3-20	〃	
		19				
1	—	18	COTOVELO 45°	COMERCIAL VCL-32	LATÃO	ø 1/4 NPT
12	12	17	PORCA SEXT. 1/2 NC	COMERCIAL	AÇO	
1	1	16	GUARNIÇÃO 1/32 ESP.	COMERCIAL	VELUMOIDE	
2	2	15	FLANGE	VVM-3-15	CHAPA DE FERRO	
12	12	14	PARAF. CAB. SEXT. 1/2 NC	COMERCIAL	AÇO	1/2 NC x 1"
1	1	13	TAMPA FIXA	VVM-3-13	CHAPA DE FERRO	
1	1	12	CARCAÇA	VVM-3-12	CHAPA DE FERRO	
1	1	11	TAMBOR DE RETENÇÃO	VVM-3-11	CHAPA PERFORADA	
1	1	10	FILTRO SANFONADO BRANCO	COMERCIAL	ø 150 x 300 m/m	MARPIC Nº30-15-9 FS
1	1	9	TAMPA MÓVEL	VVM-3-9	CHAPA DE FERRO	
3	3	8	ARRUELA LISA ø 5/16	COMERCIAL	AÇO	
3	3	7	PORCA SEXT. 5/16 NC	COMERCIAL	AÇO	
3	3	6	HASTE DE FIXAÇÃO	VVM-3-6	FERRO TREF.	
1	1	5	NIPLE	VVM-3-5	FERRO PRETO	
2	2	4	TAMPA	VVM-3-4	CHAPA DE FERRO	
1	1	3	LUVA 1/4 NPT	COMERCIAL	FERRO MALEÁVEL	CORTAR NA METADE
1	1	2	TORNEIRA DE DESCARGA	COMERCIAL	LATÃO	1/4 NPT
—	2	1	LUVA 3" NPT	VVM-3-1	AÇO	
QUANT.		ITEM	DENOMINAÇÃO	PEÇA Nº	MATERIAL	OBS.

CONJUNTO Nº 191-D-5403

2	1	GRUPO Nº	Sec.	VIDROS VITON LTDA.	Data 24-2-69
			Pag.		Des.
FILTRO C/ FLANGES	FILTRO C/ ROSCA	DESCRIÇÃO DO GRUPO	Mat		Escala 1:1 / Cop. / Ver.
			Conjunto SUPPLY PIPING MAQUINA I.S.		Subst.
			Nome da Peça FILTRO DE AR		Nº da Peça VVM-3
9-8 95	24-2 1969	DATA	Tratam. Térmico		Nº do Desenho

ROLO 26 FÔLHA 1