
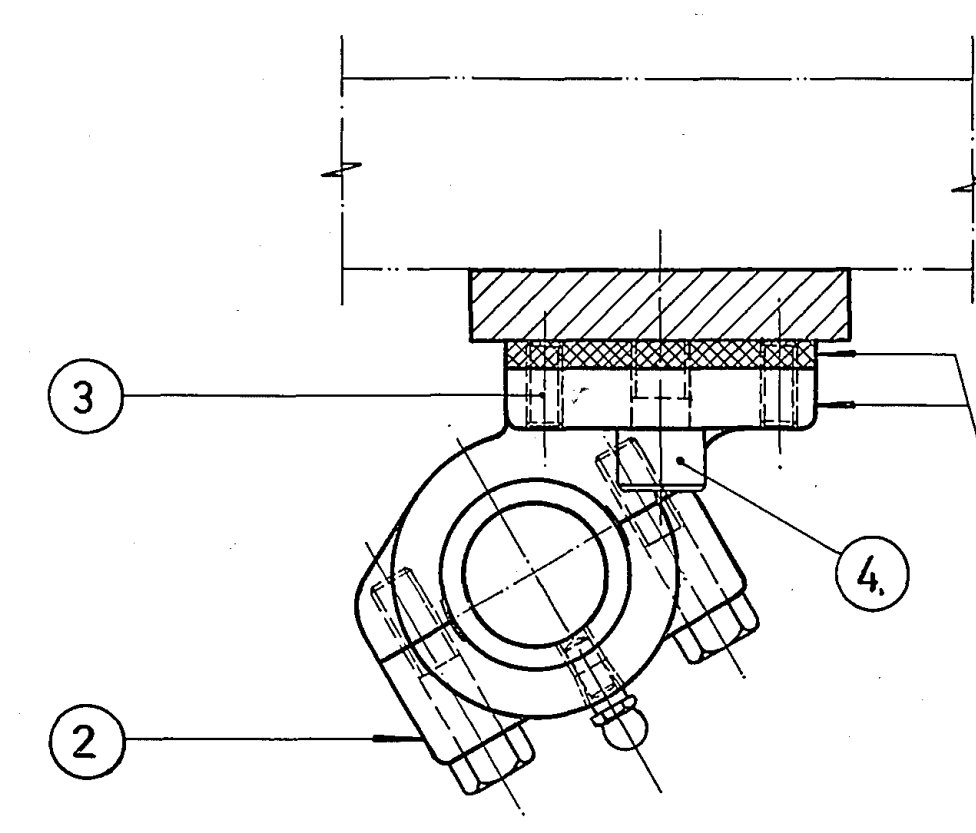
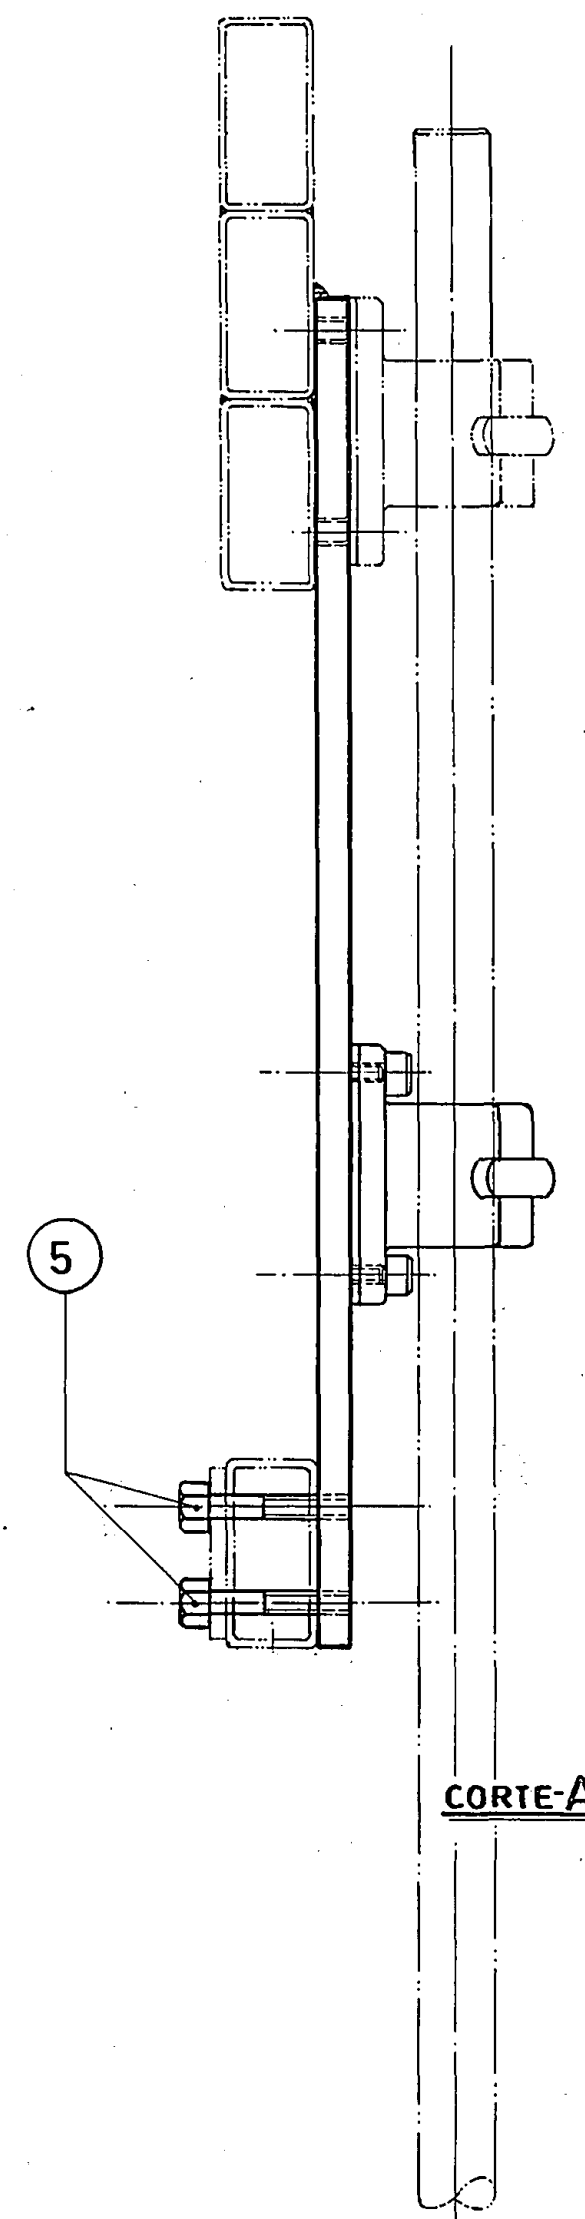


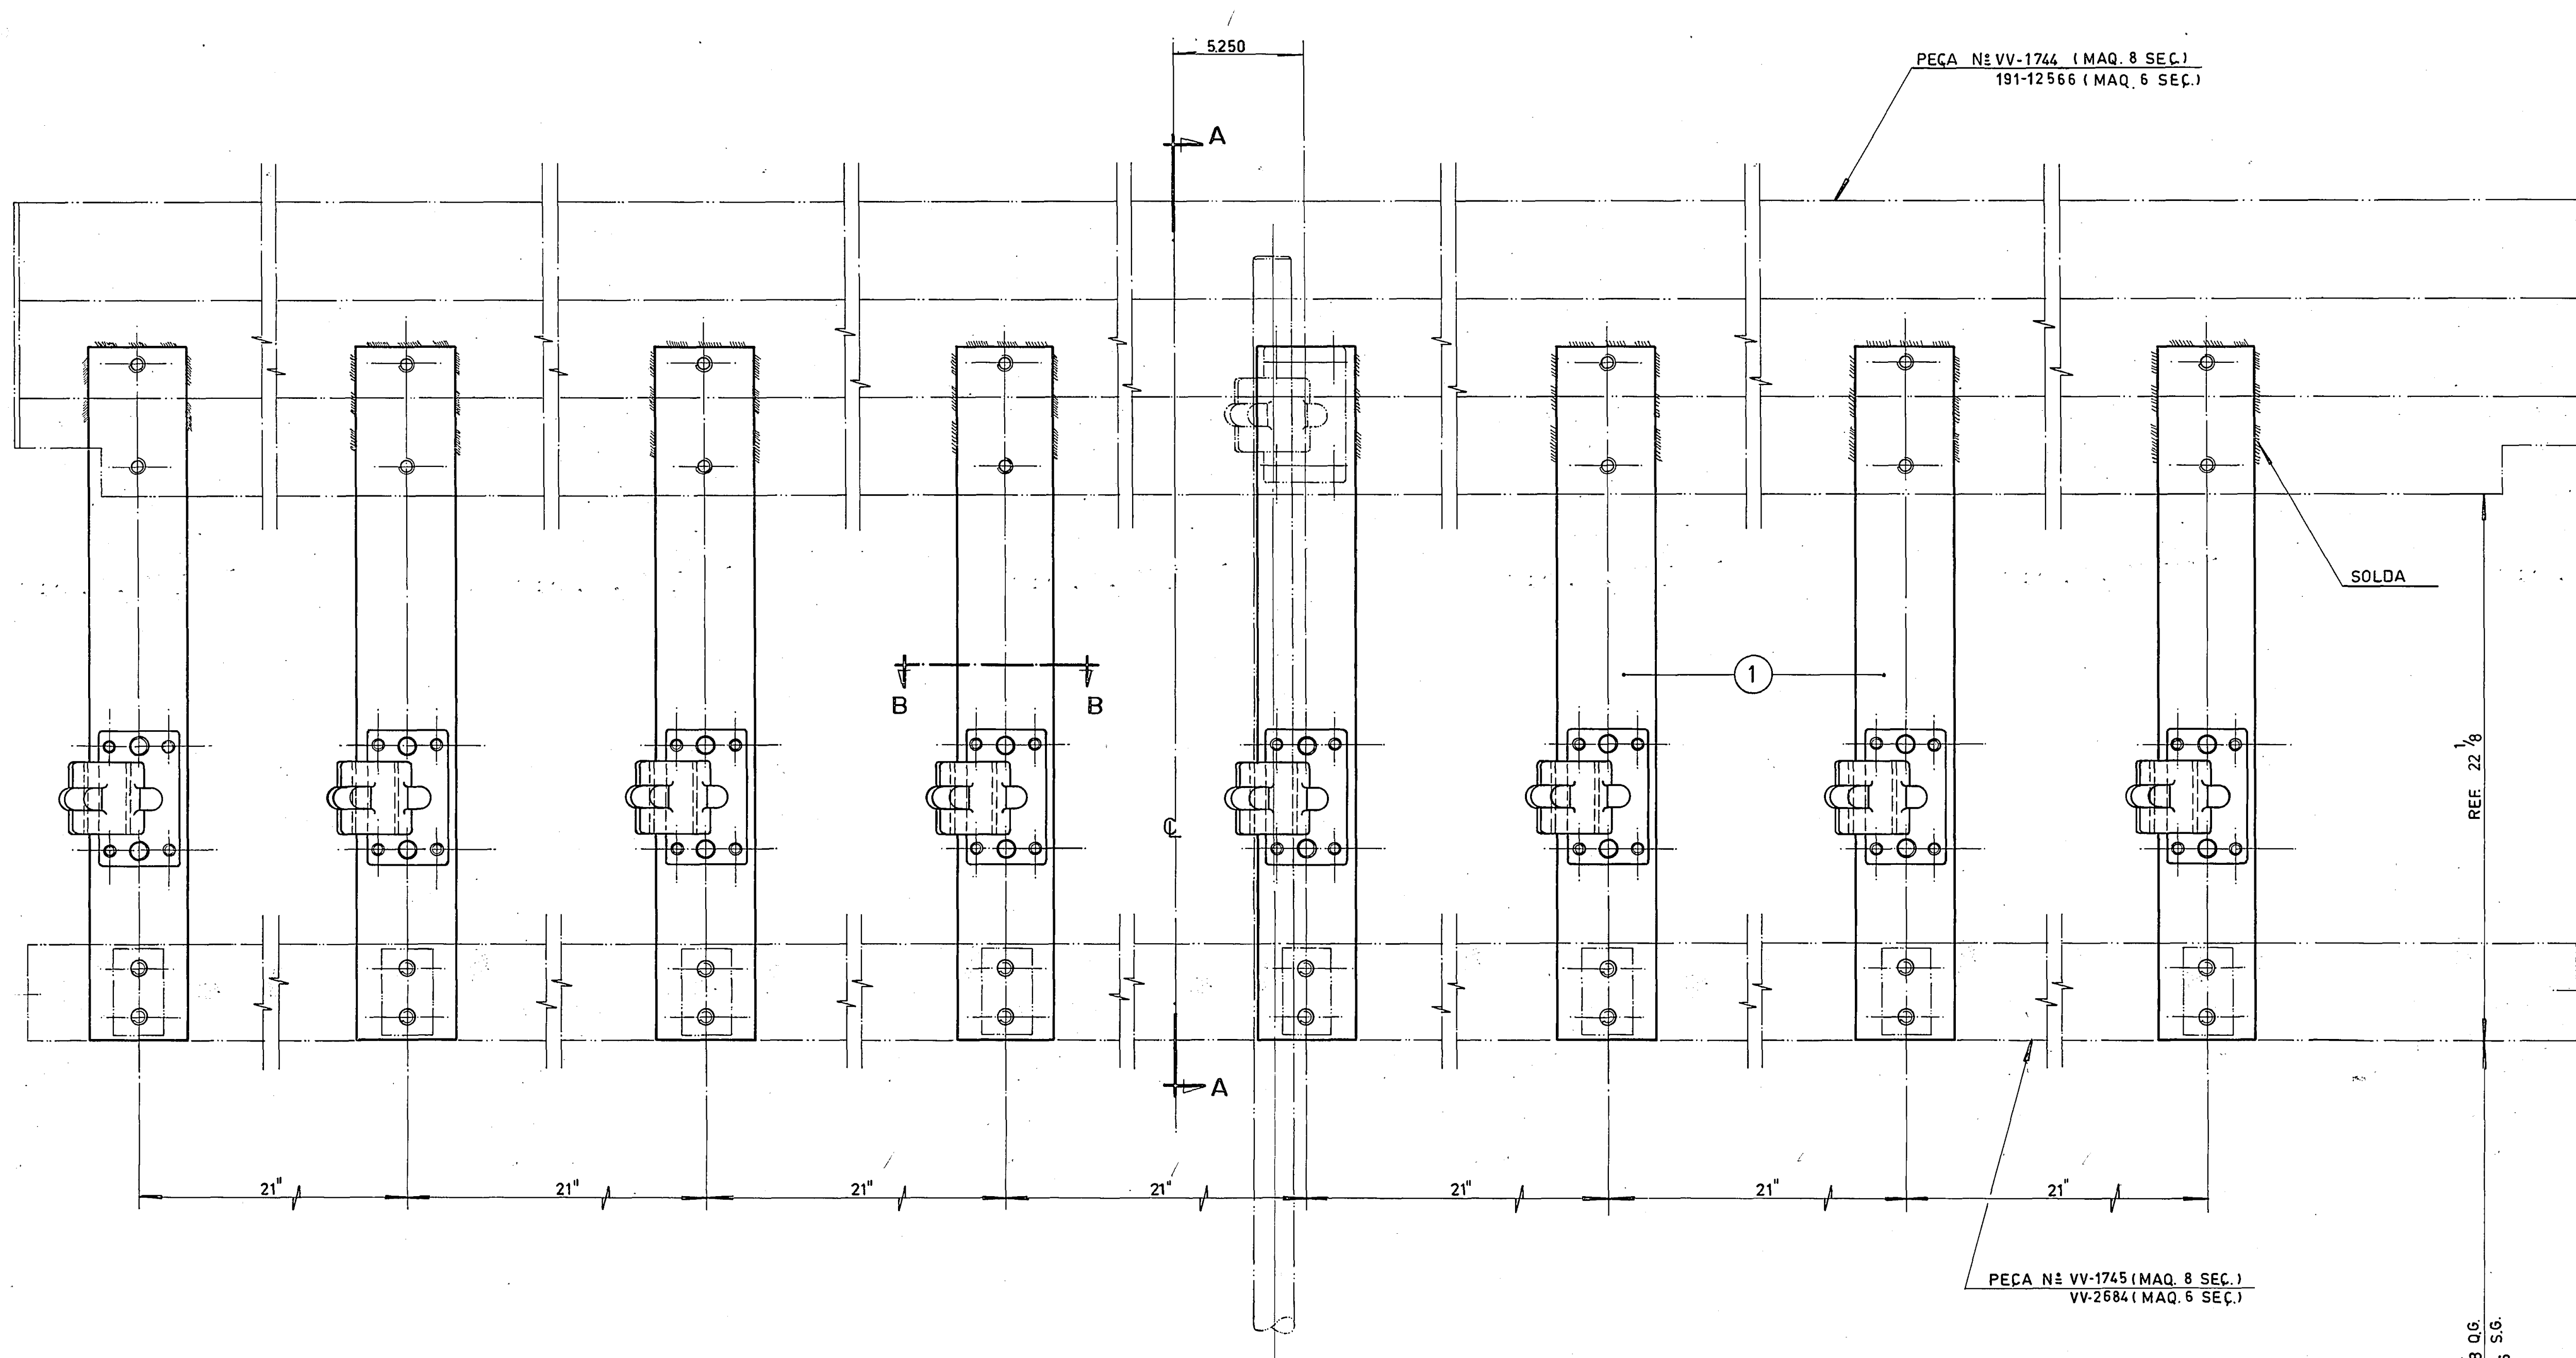

NOTA
 APÓS COLOCADOS OS PARAF. POS. ③ E ④
 REAJUSTA-LOS COLOCANDO O MANCAL
 PERFEITAMENTE EM LINHA COM O EIXO DO PISTÃO.
 TIRAR TODO ATRITO OU ESFORÇO ENTRE A BUCHA
 E O EIXO E ENCHER O ESPAÇO ENTRE A PLACA
 E O MANCAL COM METAL PATENTE.

NOTA
 USADO SOMENTE NA MAQ.
 Nº VV-102 (CHINA)

16	12	5	PARAF. CAB. SEXTAVADA	COMERCIAL	ACO	1/2" NC x 3 1/2"
16	12	4	PARAF. ALLEN C/ CAB.	COMERCIAL	ACO	5/8" NC x 2"
32	24	3	PARAF. ALLEN S/ CAB.	COMERCIAL	ACO	5/8" NC x 1 1/2"
8	6	2	BEARING BRACKET	191-F-5625	VIDESUB-CON.	
8	6	1	BRACKET (DOUBLE O.B. BEARING)	7490-1823	ACO	3/4" x 4" x 28 3/16"
QUANT.	POS.	GRP. Nº	DENOMINAÇÃO	PEÇA Nº	MAT.	OBS.
2	1		VIDROS VITON LTDA.			
MAQ. IS. 8 SEC.	MAQ. IS. 6 SEC.	DESCR. DO GRUPO	MAQ. IS. 6 SEC. & MAQ. IS. 8 SEC.			
			SUPPORTO DO MANCAL SUP. DO BAFFLE - Q.G. & S.G.			
21-04-87						