


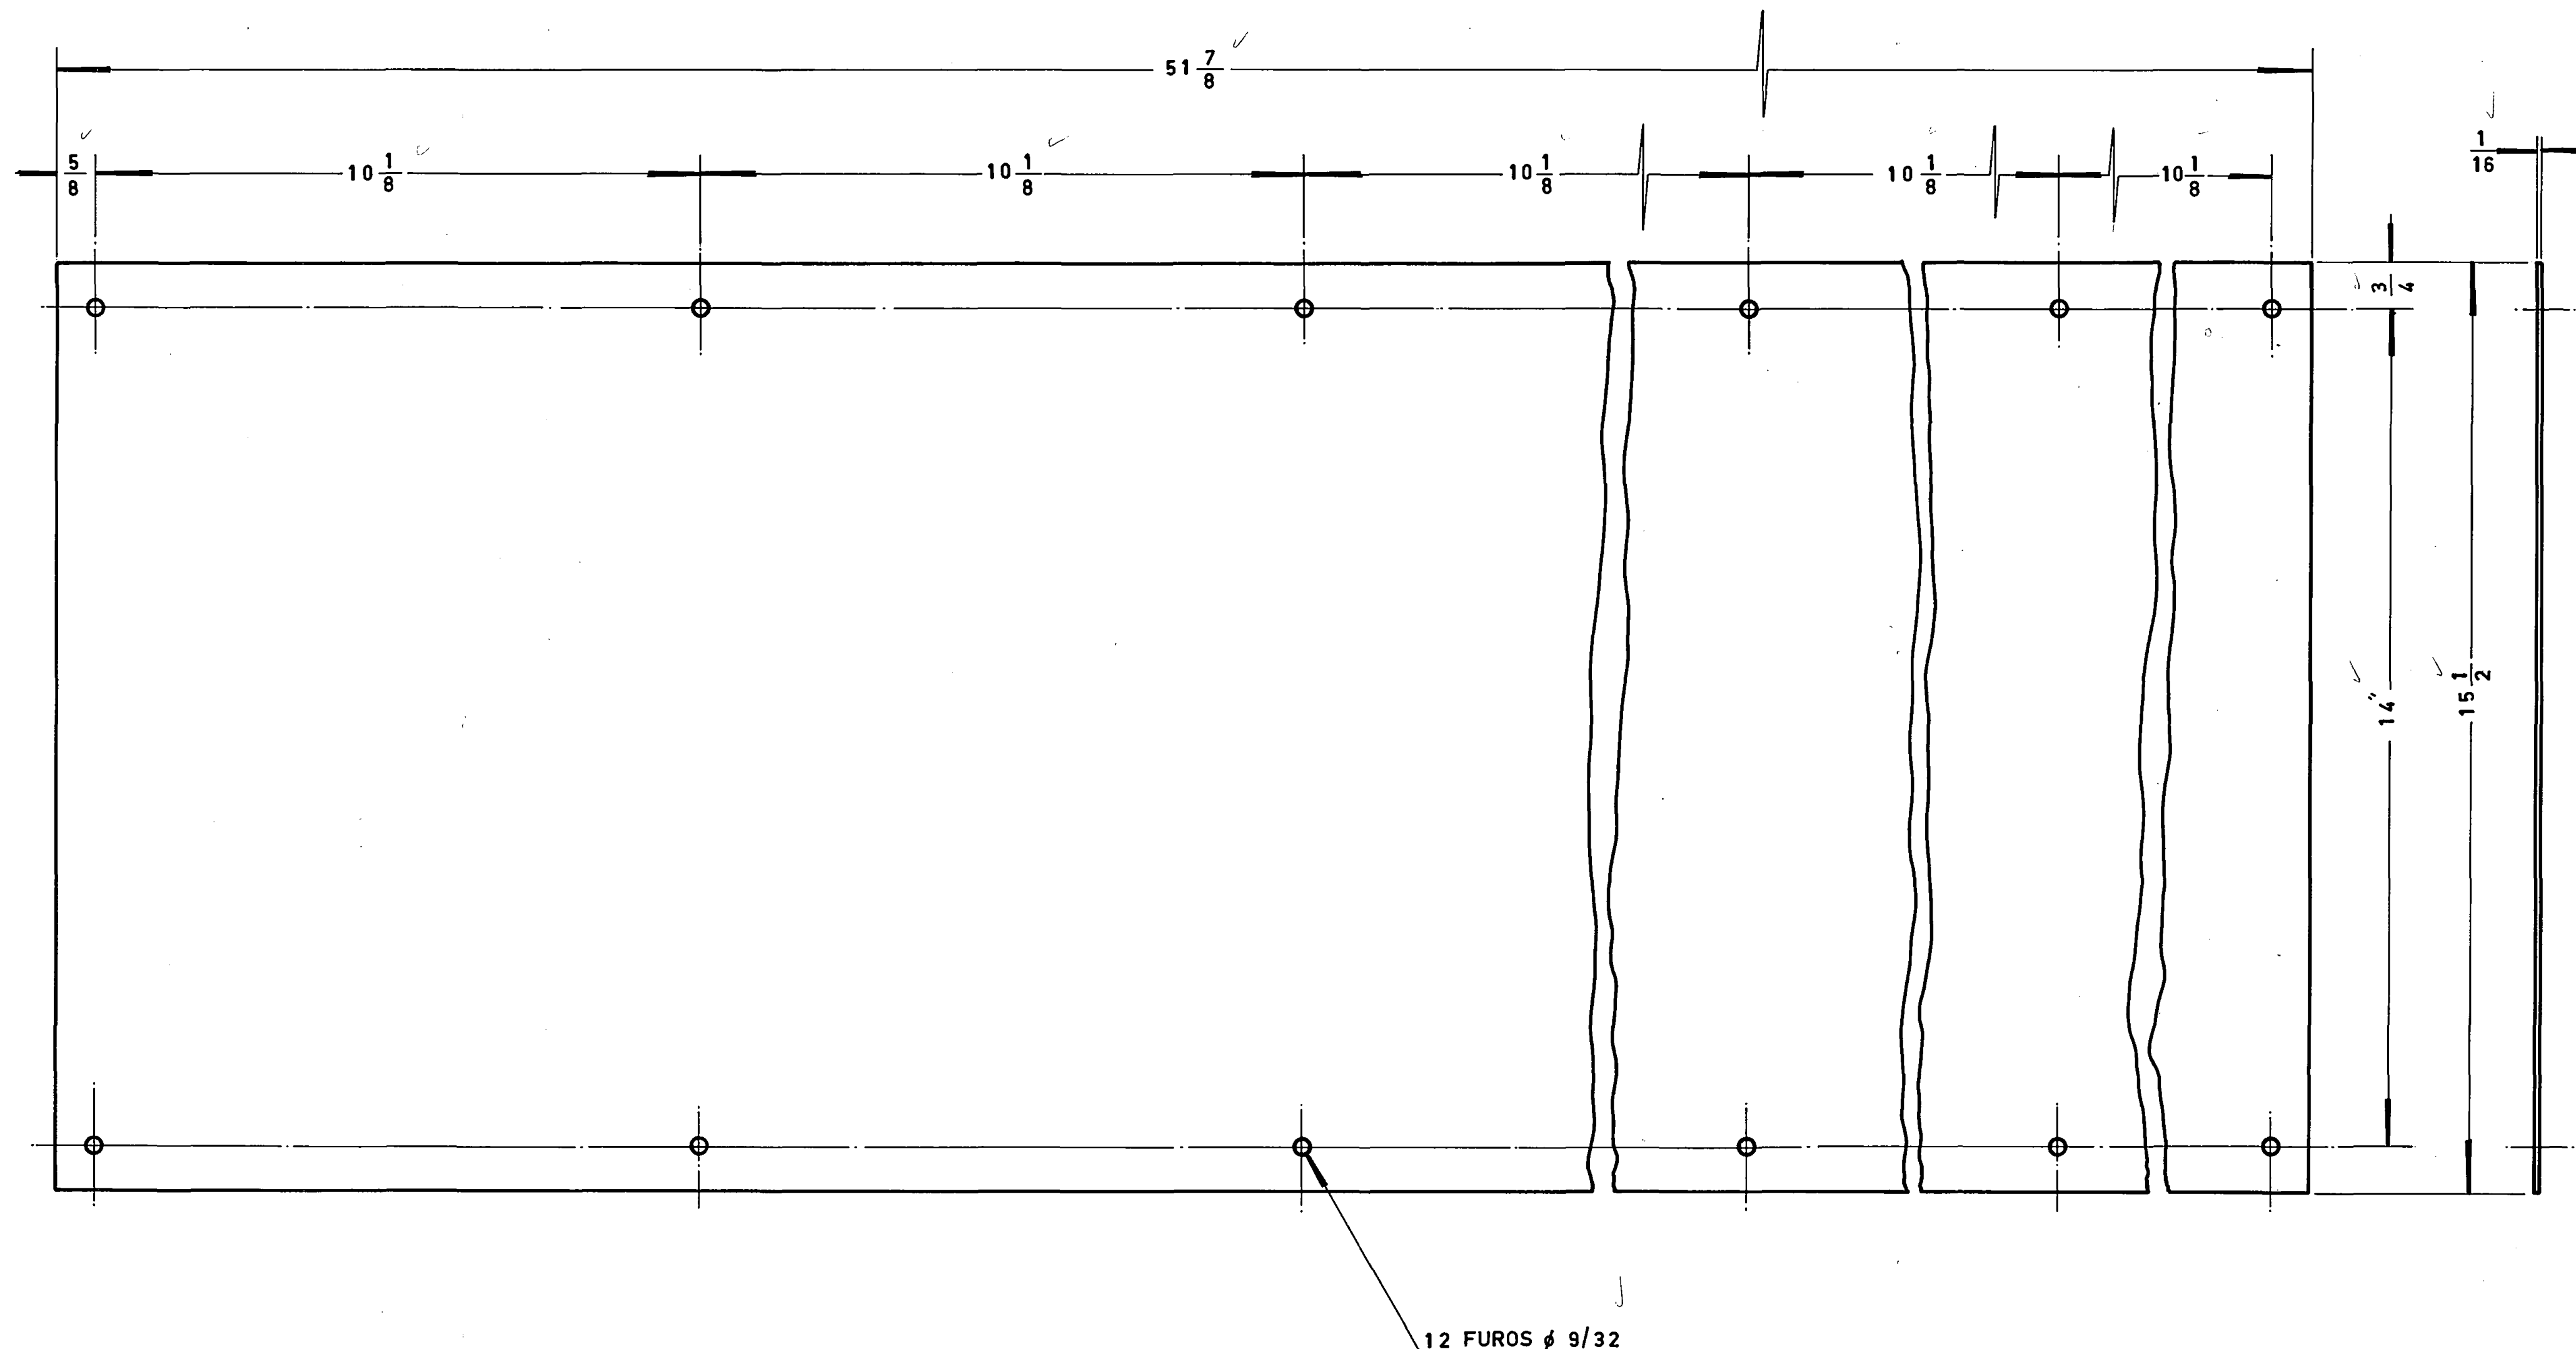

DATA: 12-05-89	VIDROS VITON LIT	
TOLERANCIAS STANDARD PARA SUPERFICIES USINADAS SEM TOLERANCIA INDICADA	MAT. CHAPA DE AÇO 1/16	
DECIMAL ± 0.05 "	NOME PAINEL DE CONTROLE DE AR DO CONJ. (LADO ESQ. E DIR. DA MÁQ.)	N. DA VVM-413
FRAÇÃO DE 0" ATÉ 5" $\pm 1/64$ DE 5" ATÉ 24" $\pm 1/32$ ACIMA DE 24" $\pm 1/16$	NOME DA PEÇA TAMPA LATERAL (SUPER.)	N. DA VVM-413-7
	TRAT.	
	TERM.	
	ESQ. 1/2	