


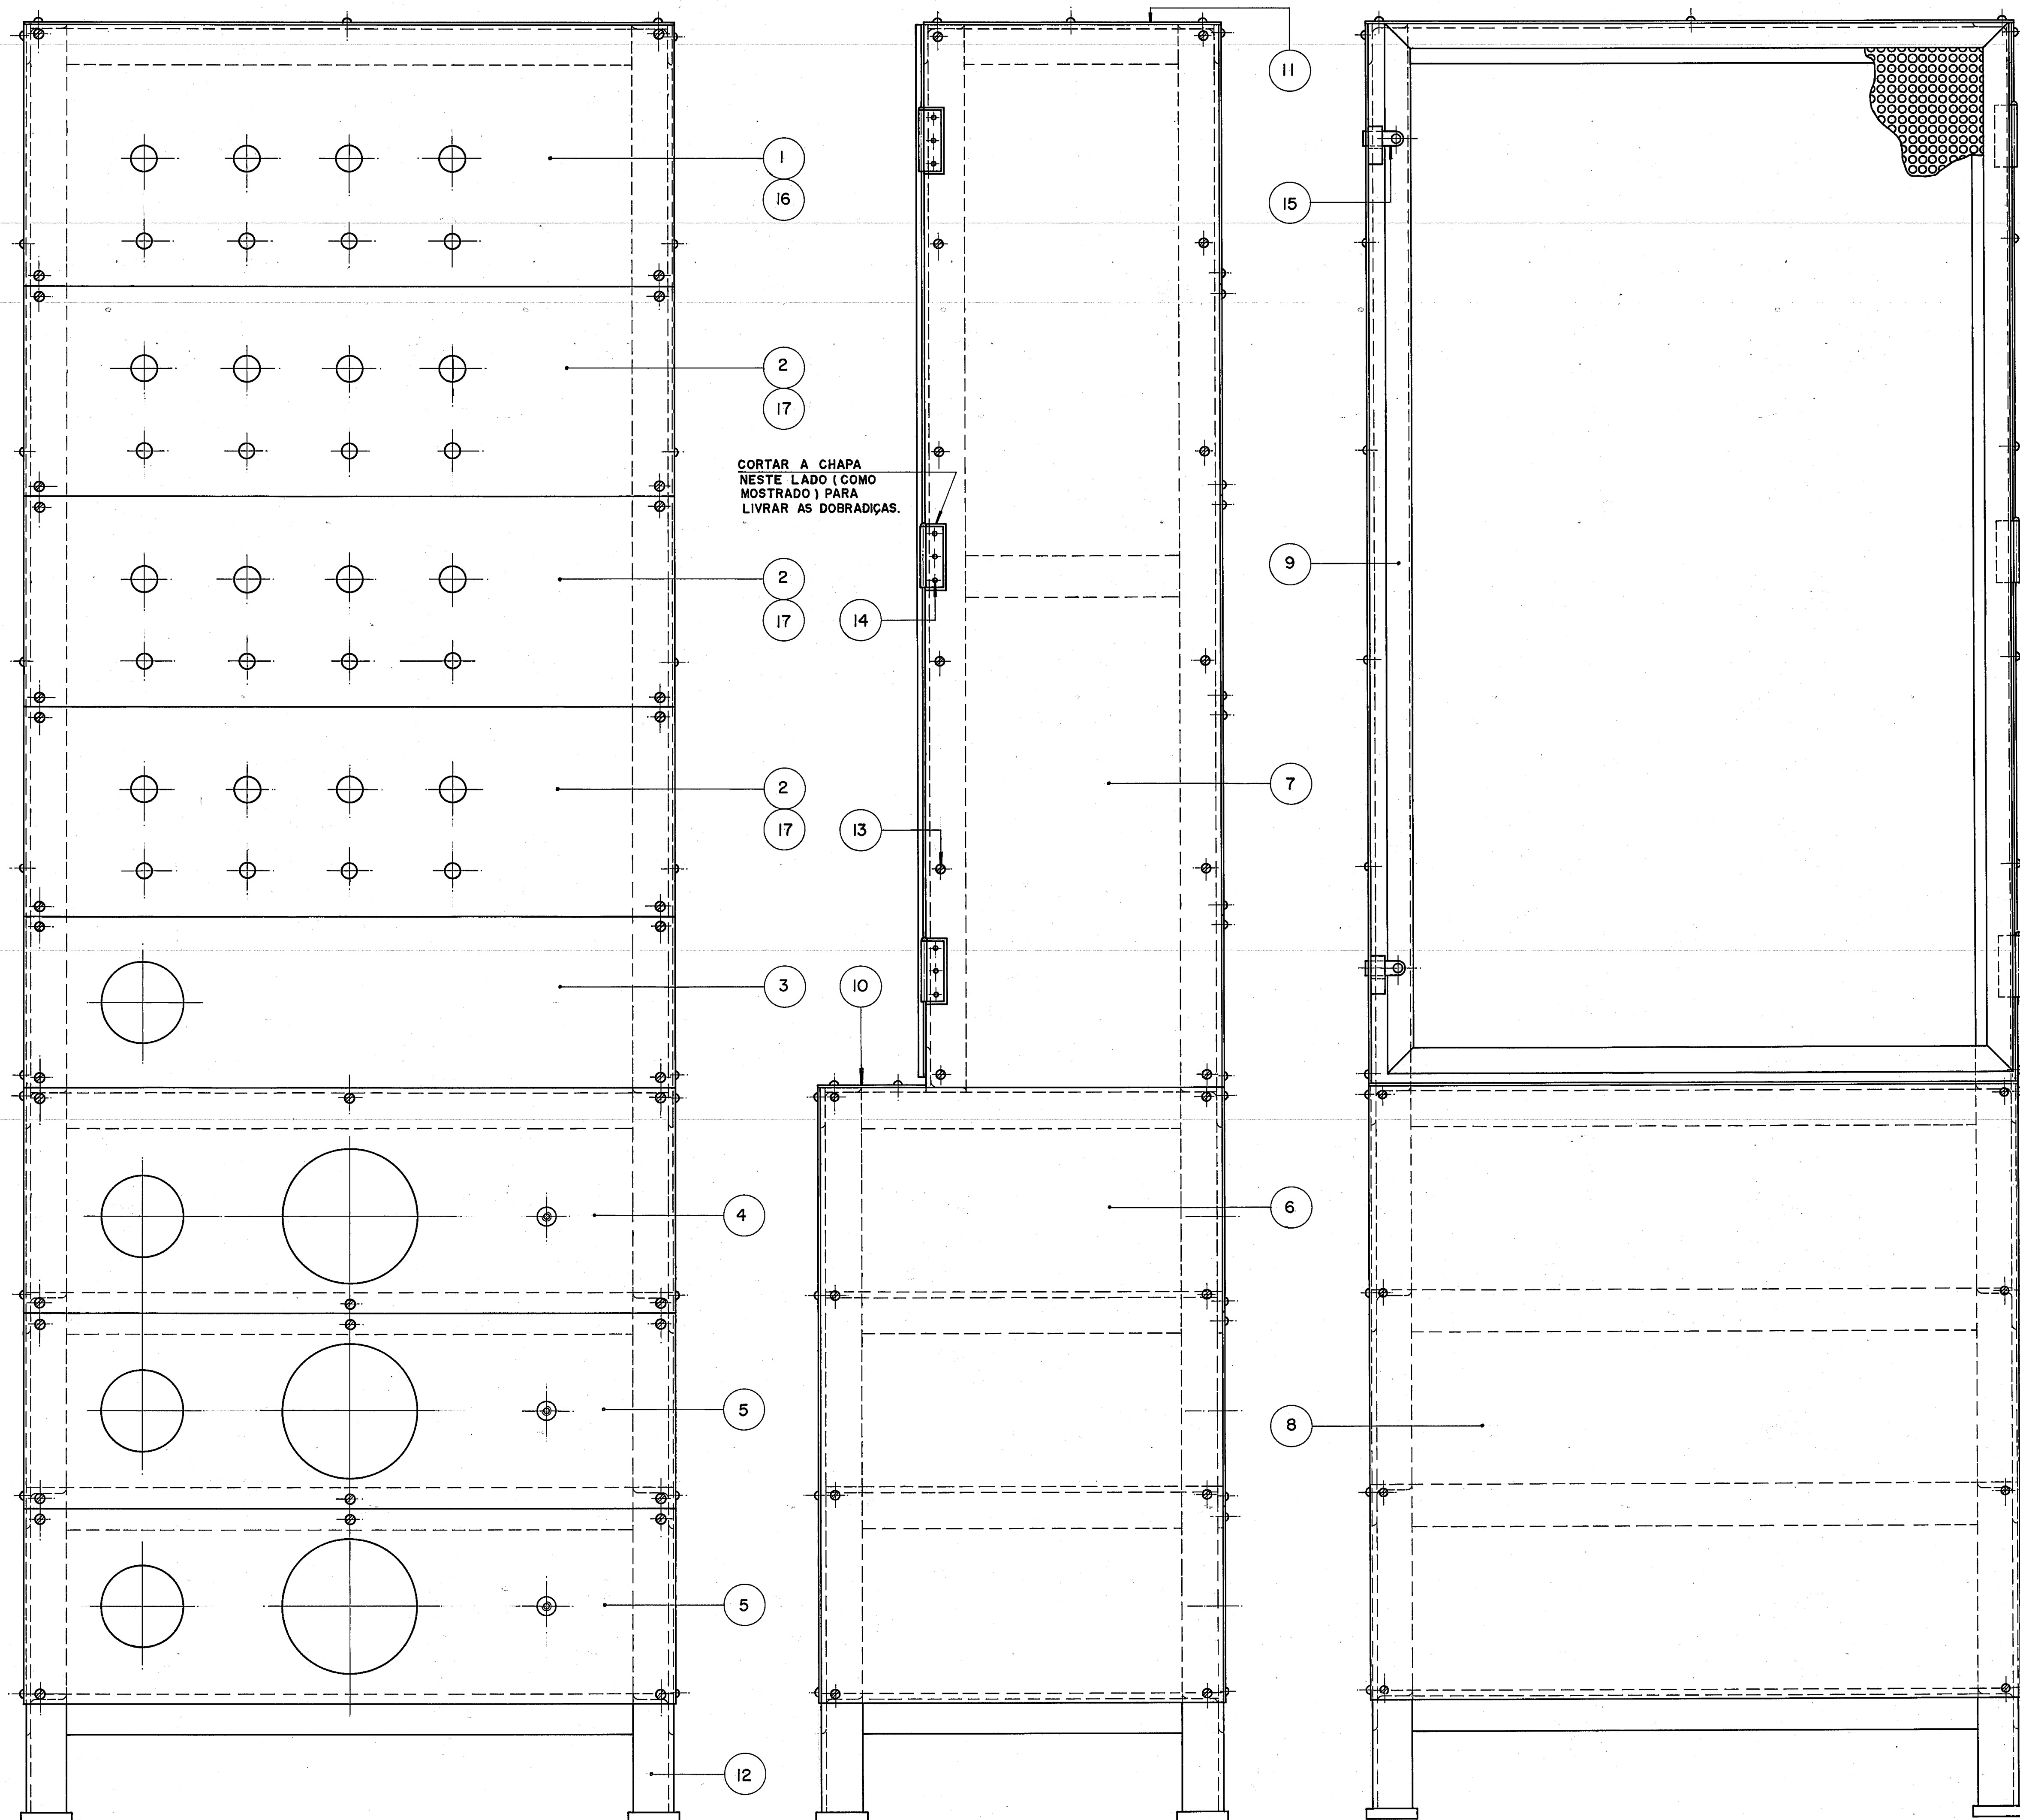

OBS.:
POS. 10 e 11- EXECUTAR NA MONT.
CONFORME NECES.

VIDE
OBS.

3	—	17	TAMPA FRONTAL	VVM-413-17	CHAPA AÇO	
1	—	16	TAMPA FRONTAL SUP.	VVM-413-16	CHAPA AÇO	
2	2	15	TRINCO E FÊCHO	COMERCIAL	AÇO	CONF NECES.
9	9	14	PARAF. CAB. CHATA	COMERCIAL	AÇO	Nº 8 NCx3/8
94	94	13	PARAF. CAB. REDONDA	COMERCIAL	AÇO	1/4 NCx3/8
1	1	12	ESTRUTURA	VVM-413-12	AÇO	
1	1	11	TAMPA DO TÔPO	VVM-413-11	CHAPA AÇO	
1	1	10	TAMPA	VVM-413-10	CHAPA AÇO	
1	1	9	PORTINHOLA	VVM-413-9	AÇO	
1	1	8	TAMPA TRASEIRA	VVM-413-8	CHAPA AÇO	
2	2	7	TAMPA LATERAL SUP.	VVM-413-7	CHAPA AÇO	
2	2	6	TAMPA LATERAL INF.	VVM-413-6	CHAPA AÇO	
2	2	5	TAMPA FRONTAL	VVM-413-5	CHAPA AÇO	
1	1	4	TAMPA FRONTAL	VVM-413-4	CHAPA AÇO	
1	1	3	TAMPA FRONTAL	VVM-413-3	CHAPA AÇO	
—	3	2	TAMPA FRONTAL	VVM-413-2	CHAPA AÇO	
—	1	1	TAMPA FRONTAL SUP.	VVM-413-1	CHAPA AÇO	
QUANT.	POS.	DENOMINAÇÃO	PEÇA Nº	MATERIAL	OBS.	
2	1	GR. Nº	VIDROS VITON LTDA.		DES. VER. <i>Leandro</i>	
PARA MAQ. I.S. & SEC.	PARA MAQ. I.S. & SEC.	DESCR. DO GRUPO	M.T.	DATA	20-06-89	
			PAINEL DE CONTROLE DE AR (LADO ESQUERDO DA MAQ.)		VVM-414	
			PAINEL (ESQUERDO)		VVM-413	
			TRAT. TERM.	ESCALA 1/4	N.º DO DES.	