
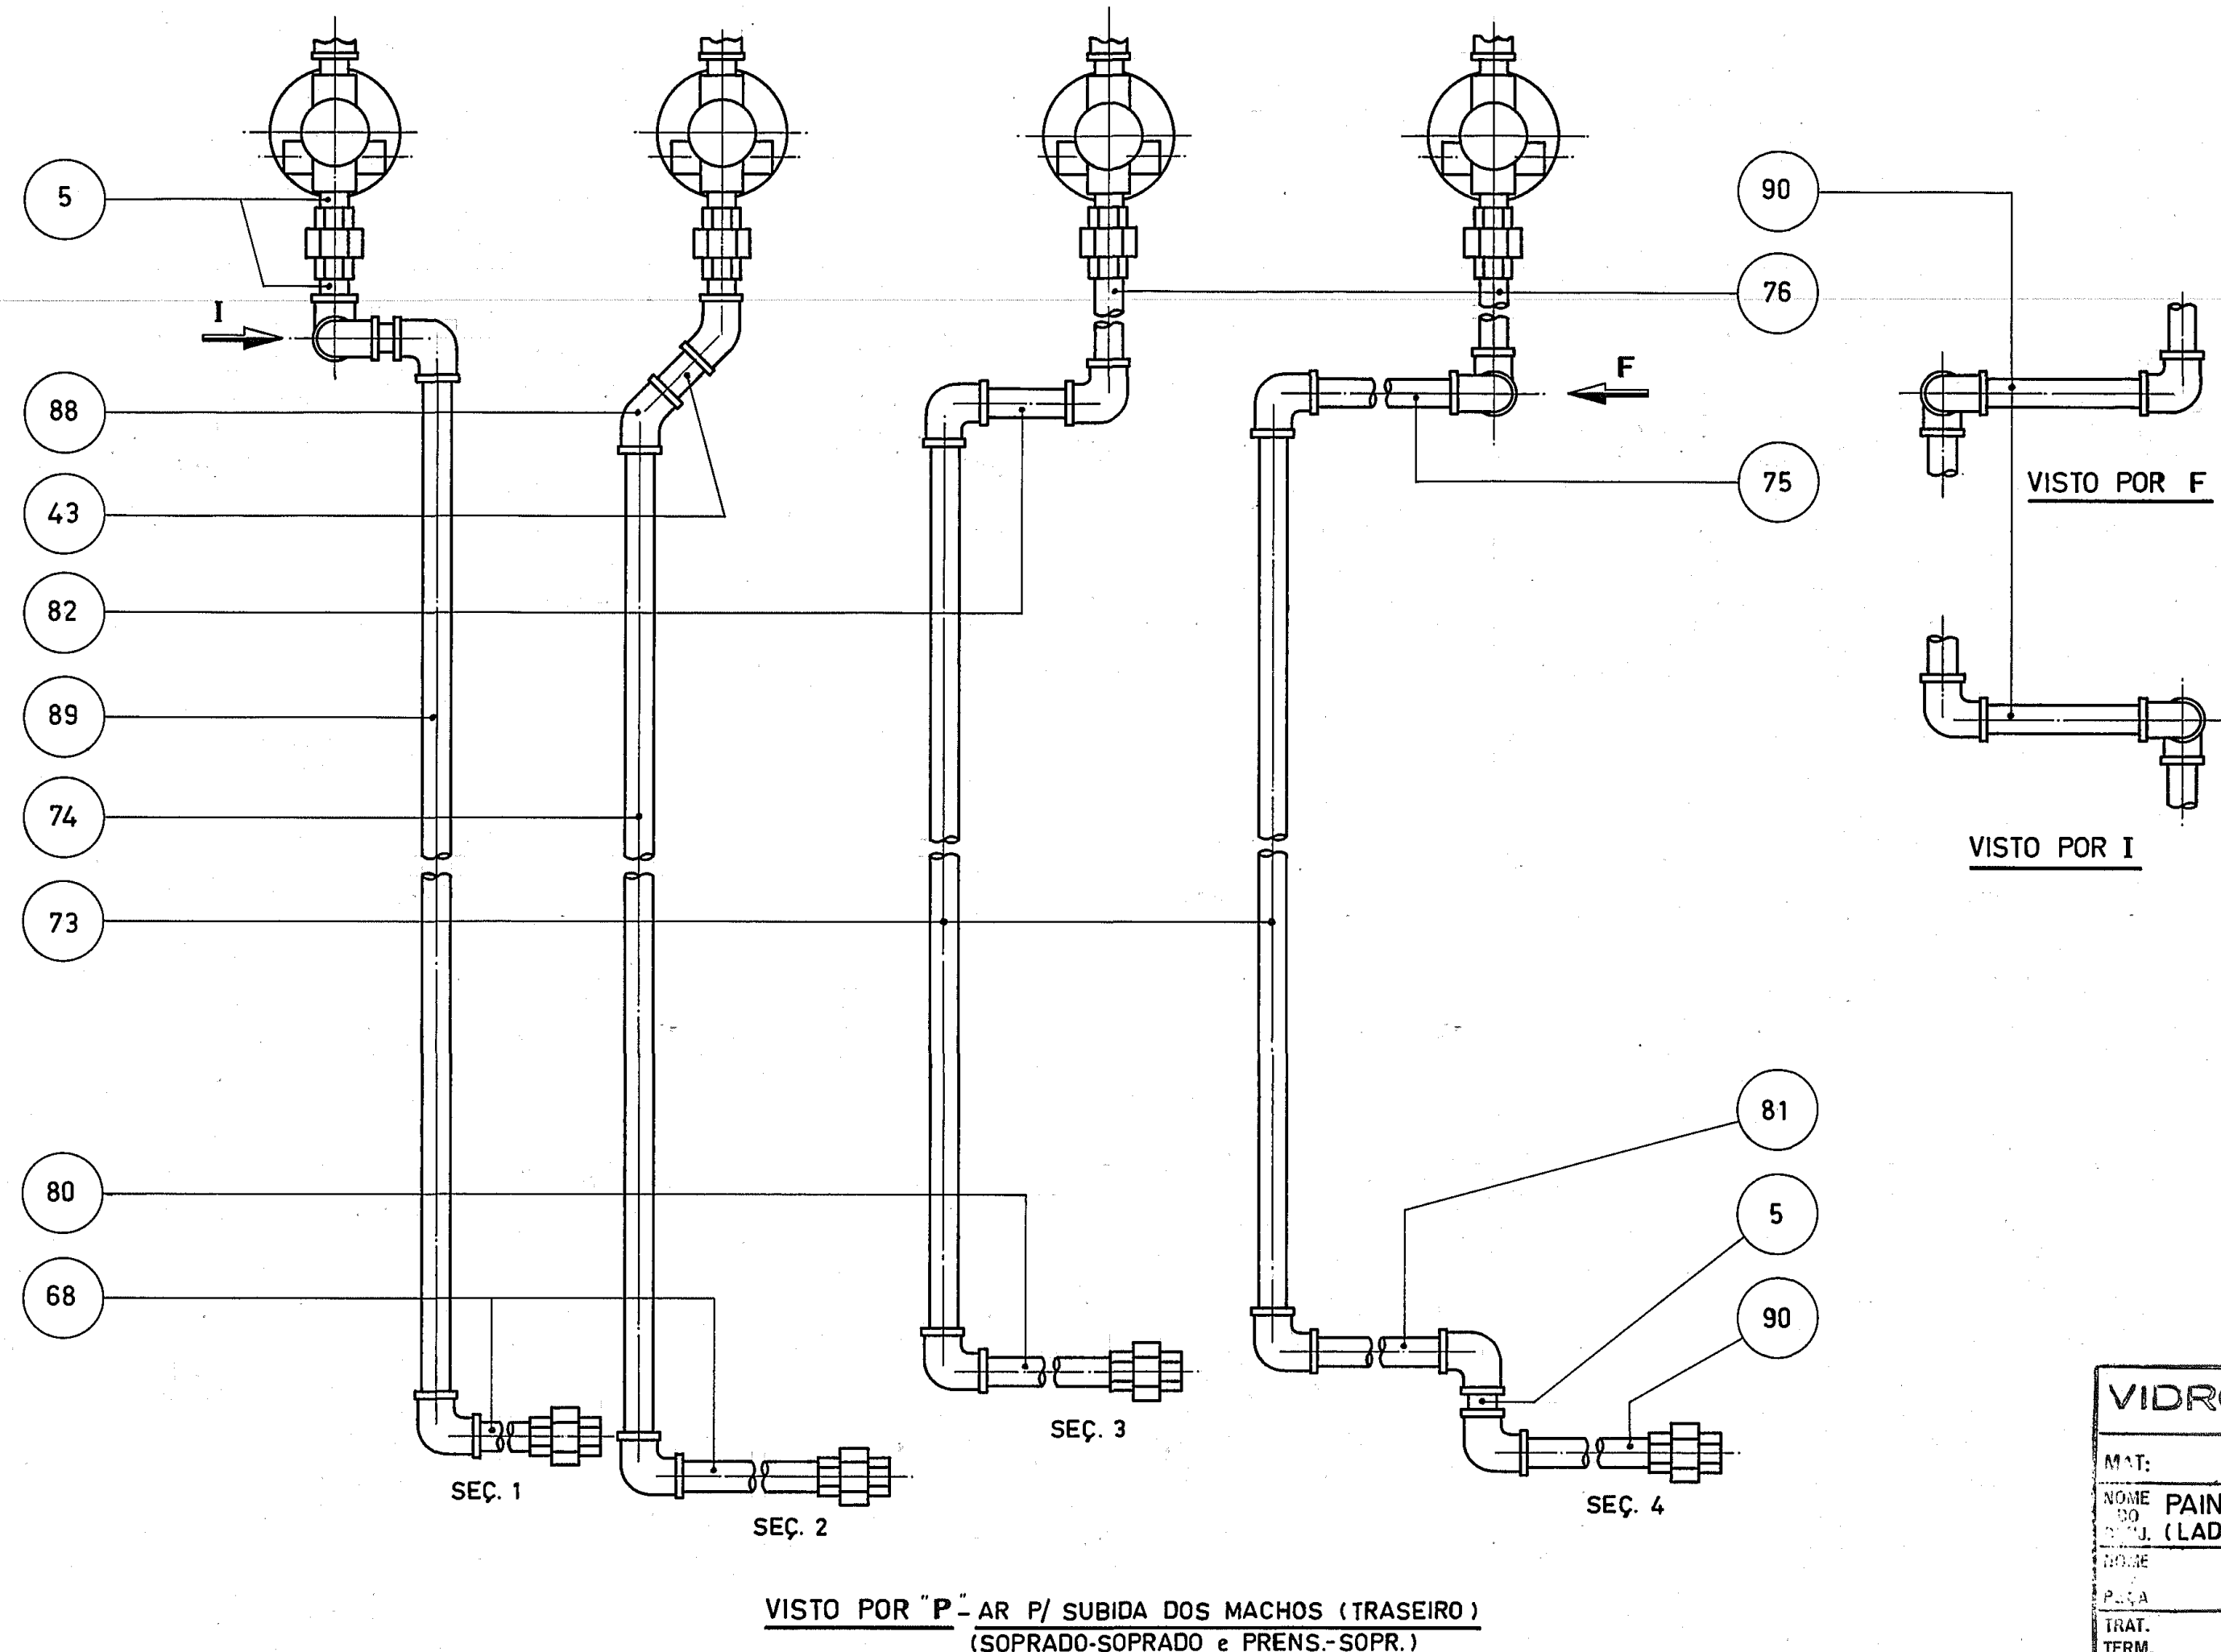
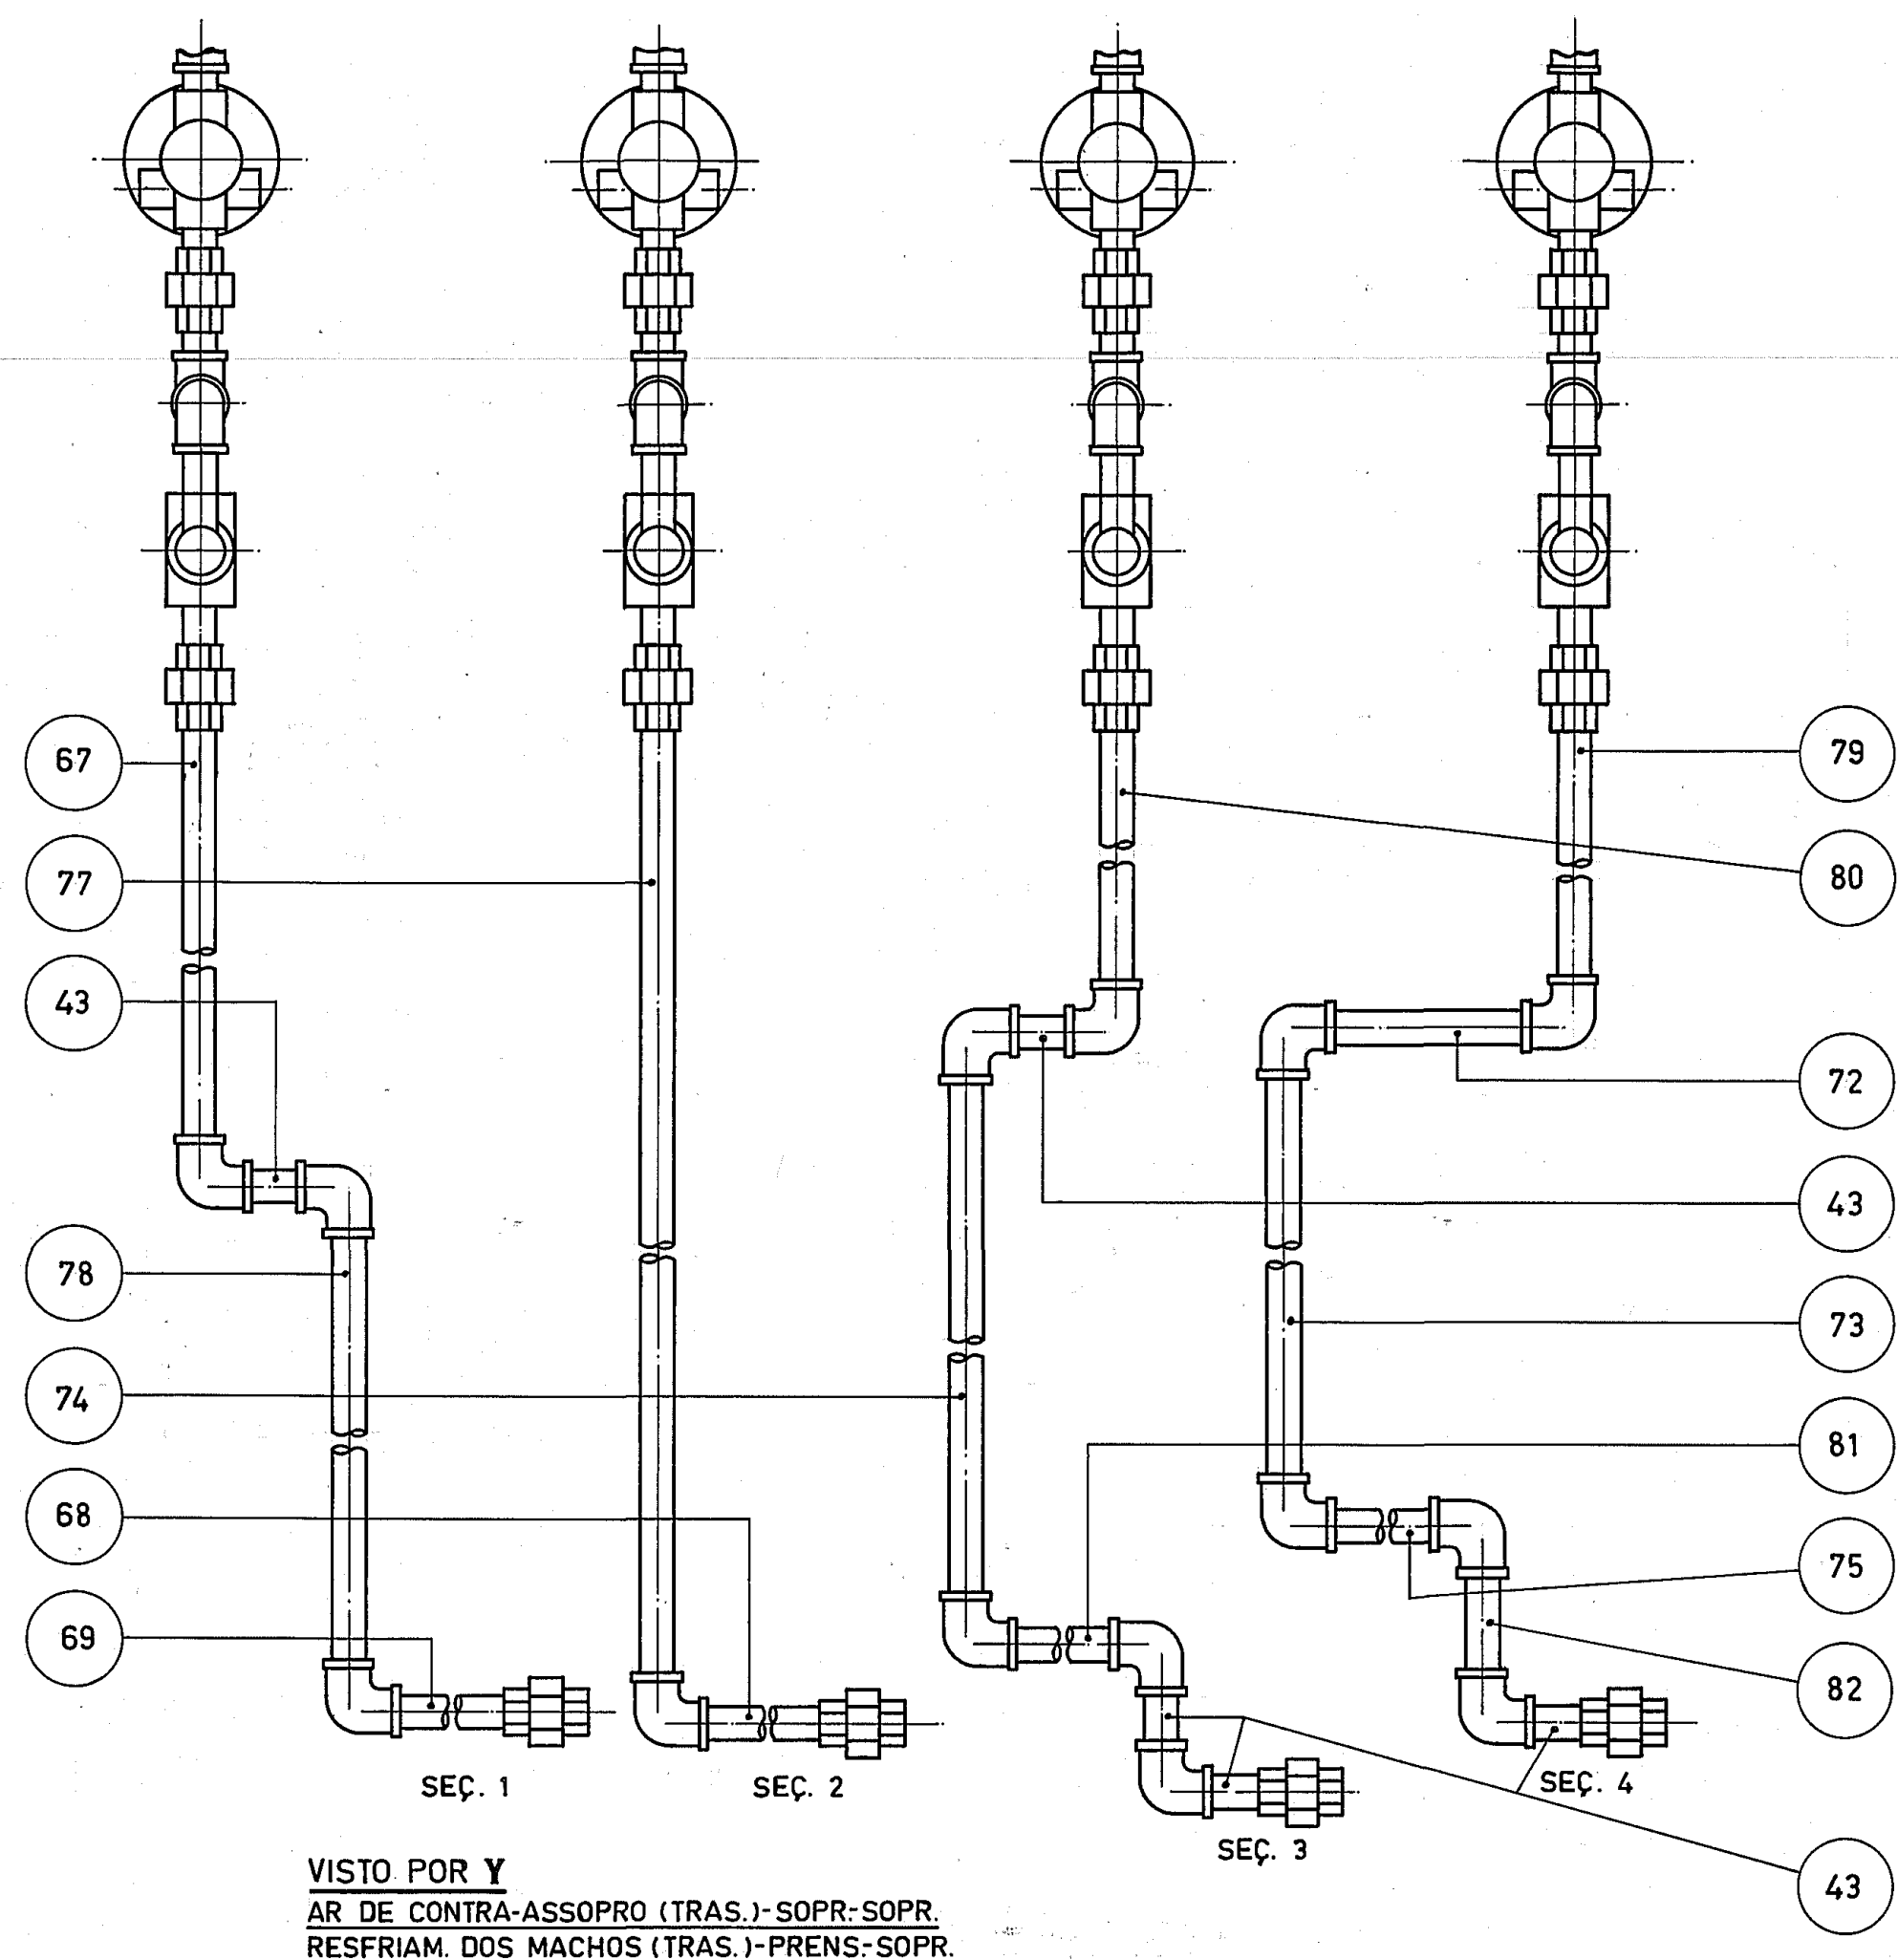
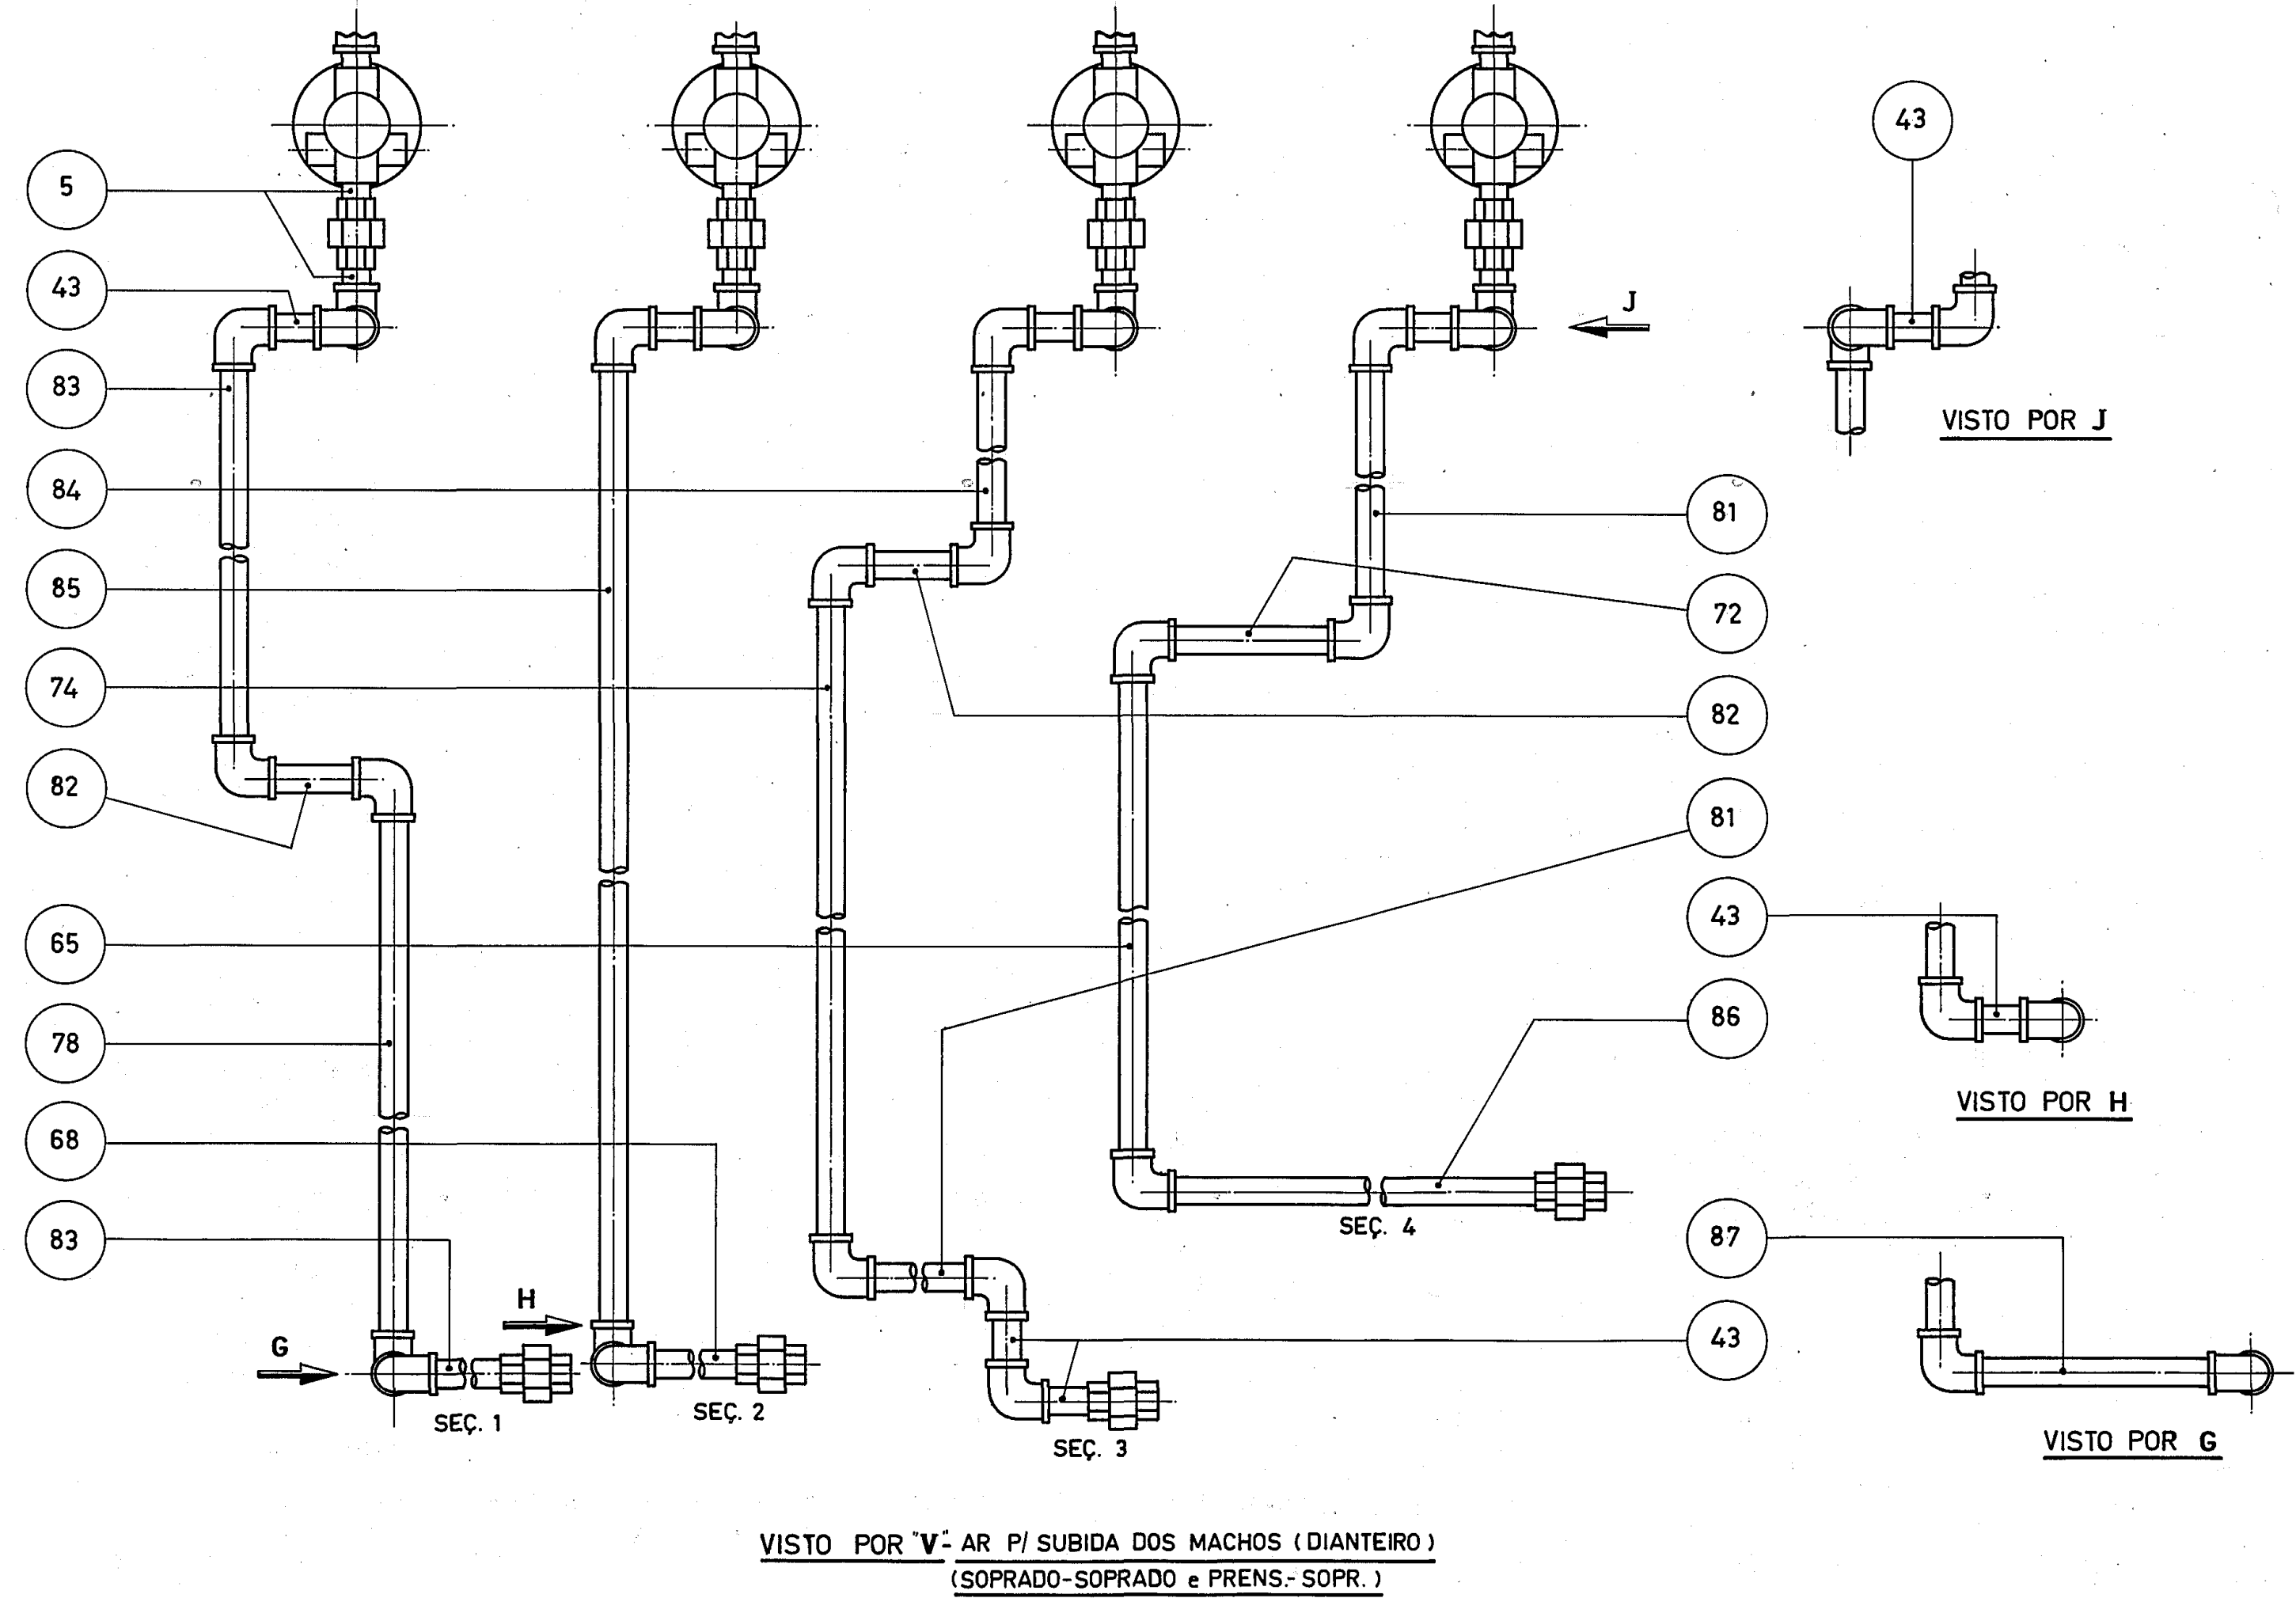


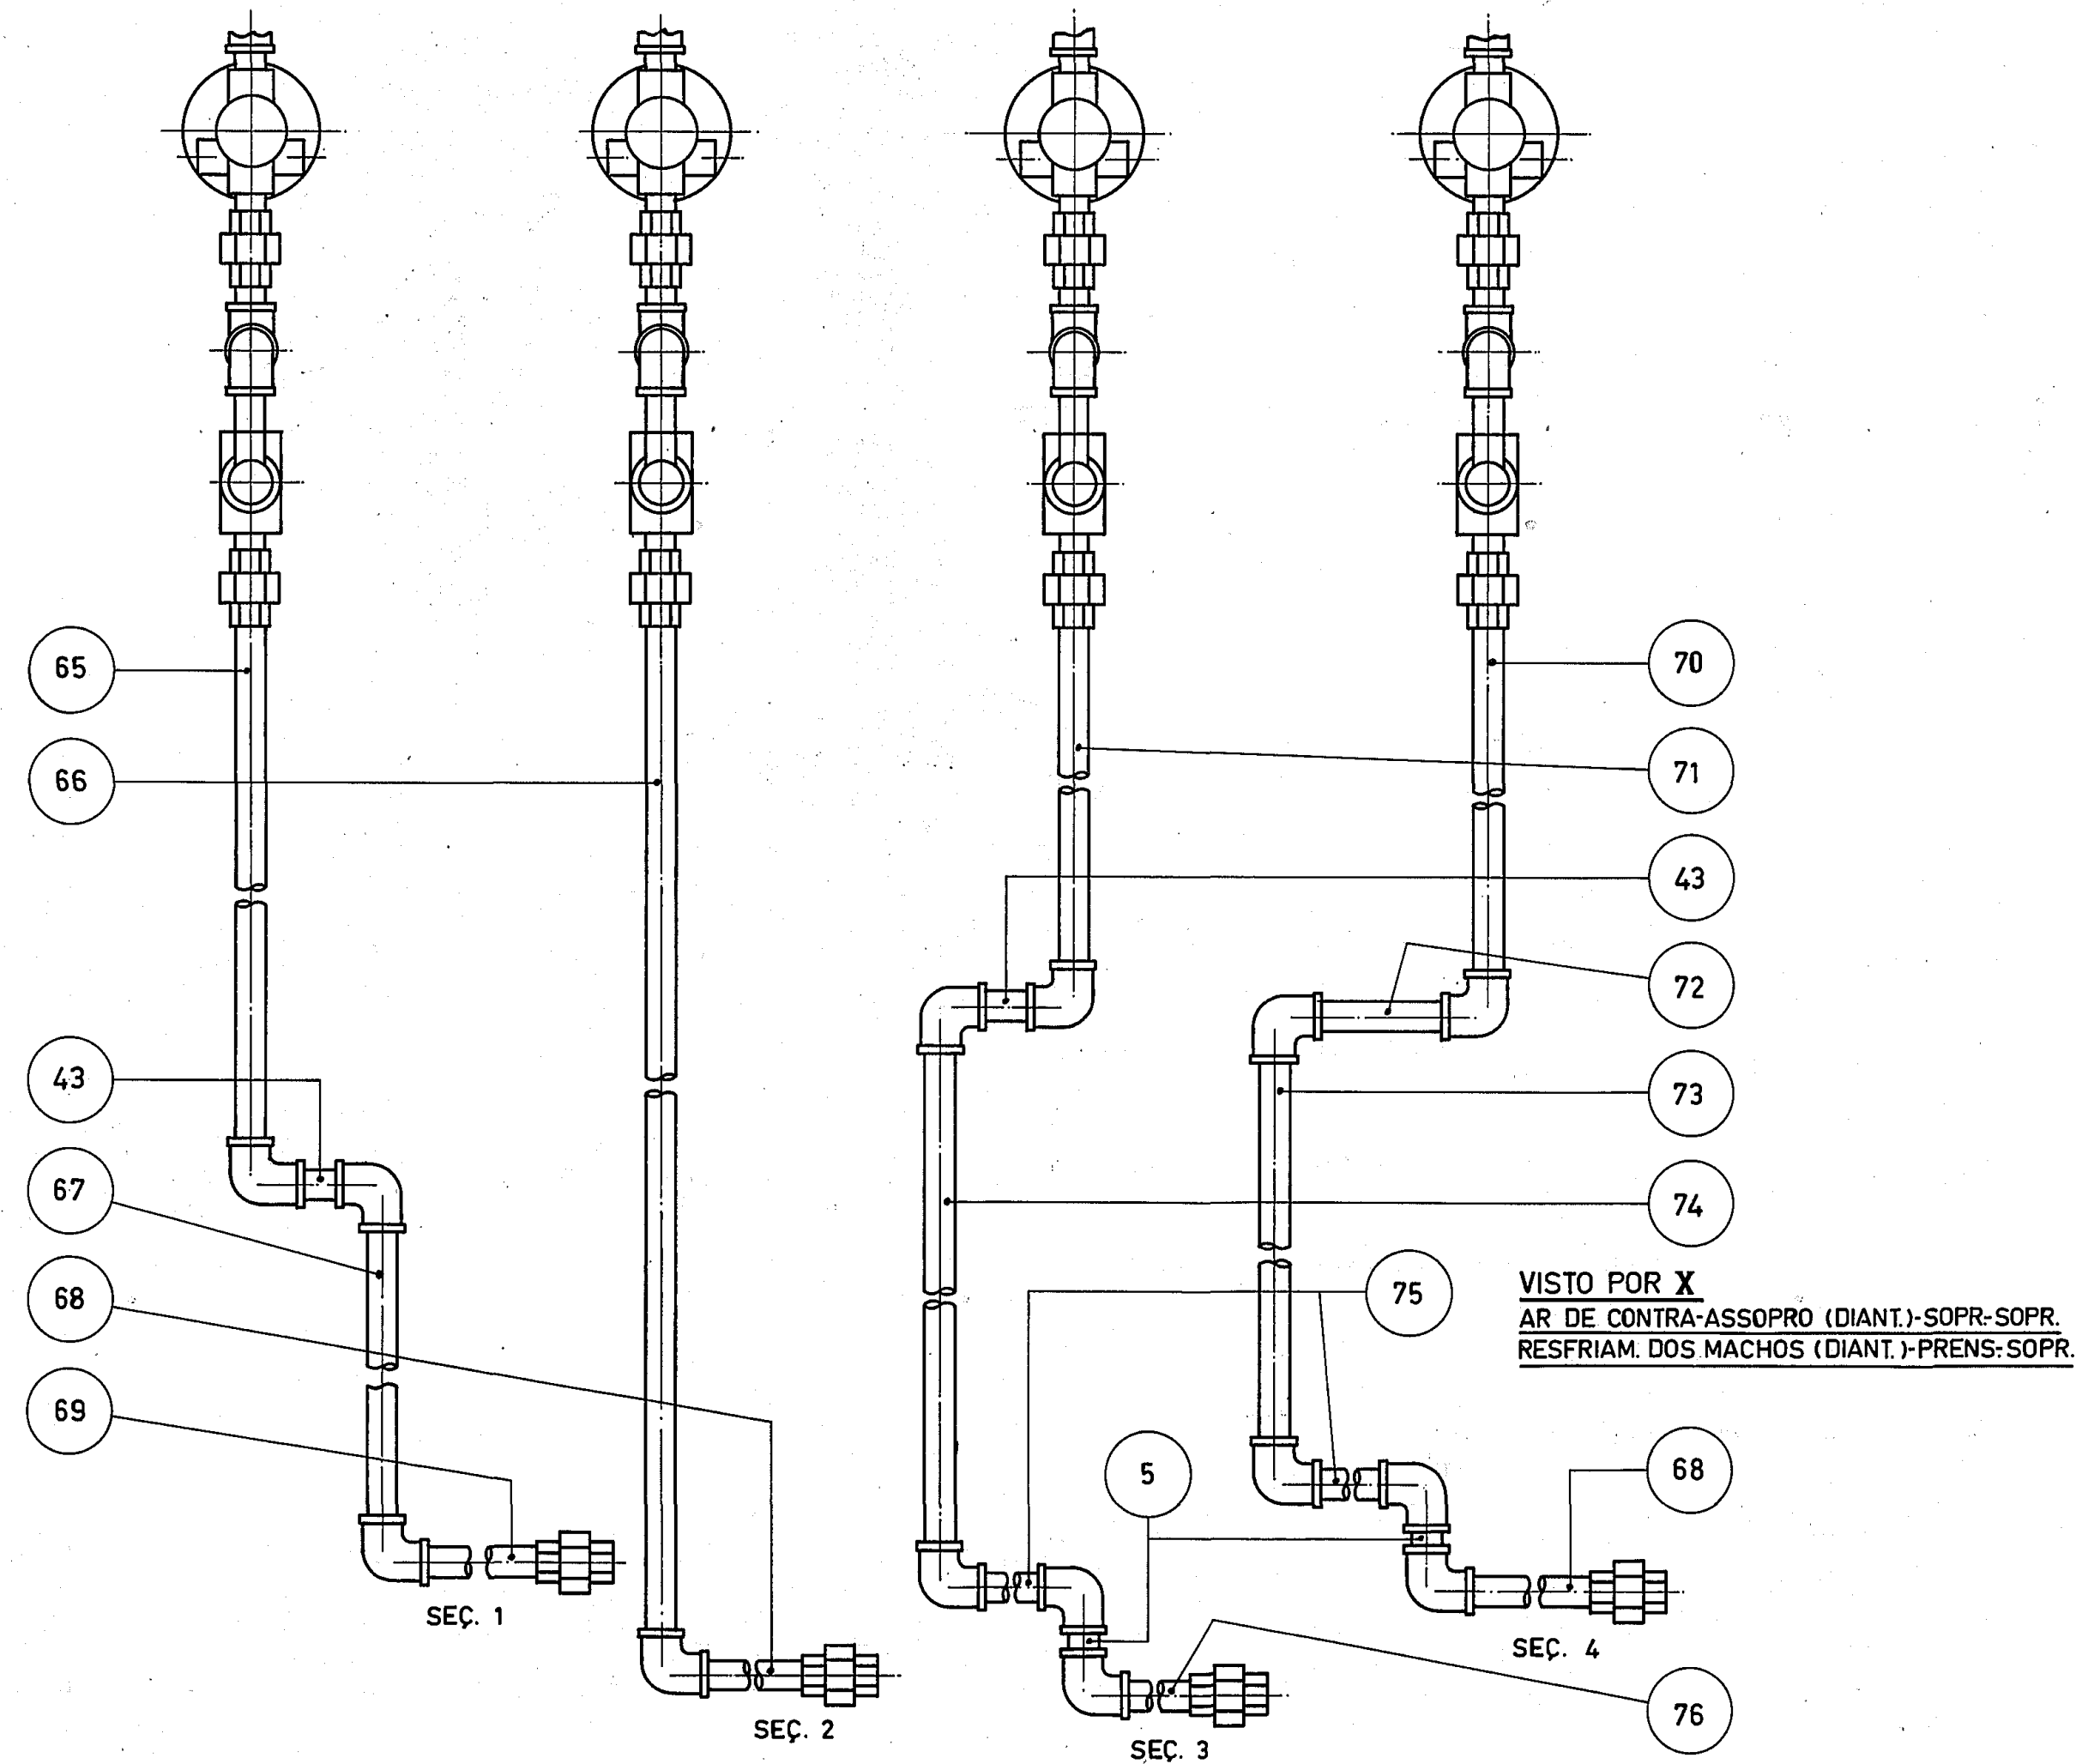

OBS: A TUBULAÇÃO MOSTRADA É
PARA MÁQUINA 8 SEÇÕES. PARA
MÁQ. 6 SEÇÕES, SUBTRAIR OS
ITENS DA SEÇÃO 4.

FOLHA 2 DE 2 FOLHAS.

VIDROS VITON LTDA.		DES. <i>[assinatura]</i>
MAT:	VER.	DATA 17-08-89
NOME DO PROJ.	QTD.	VVM-414
DATA DE PROJ.	N. DA PEÇA	
TRAT. TERM.	ESCALA	N.º DO DES.