
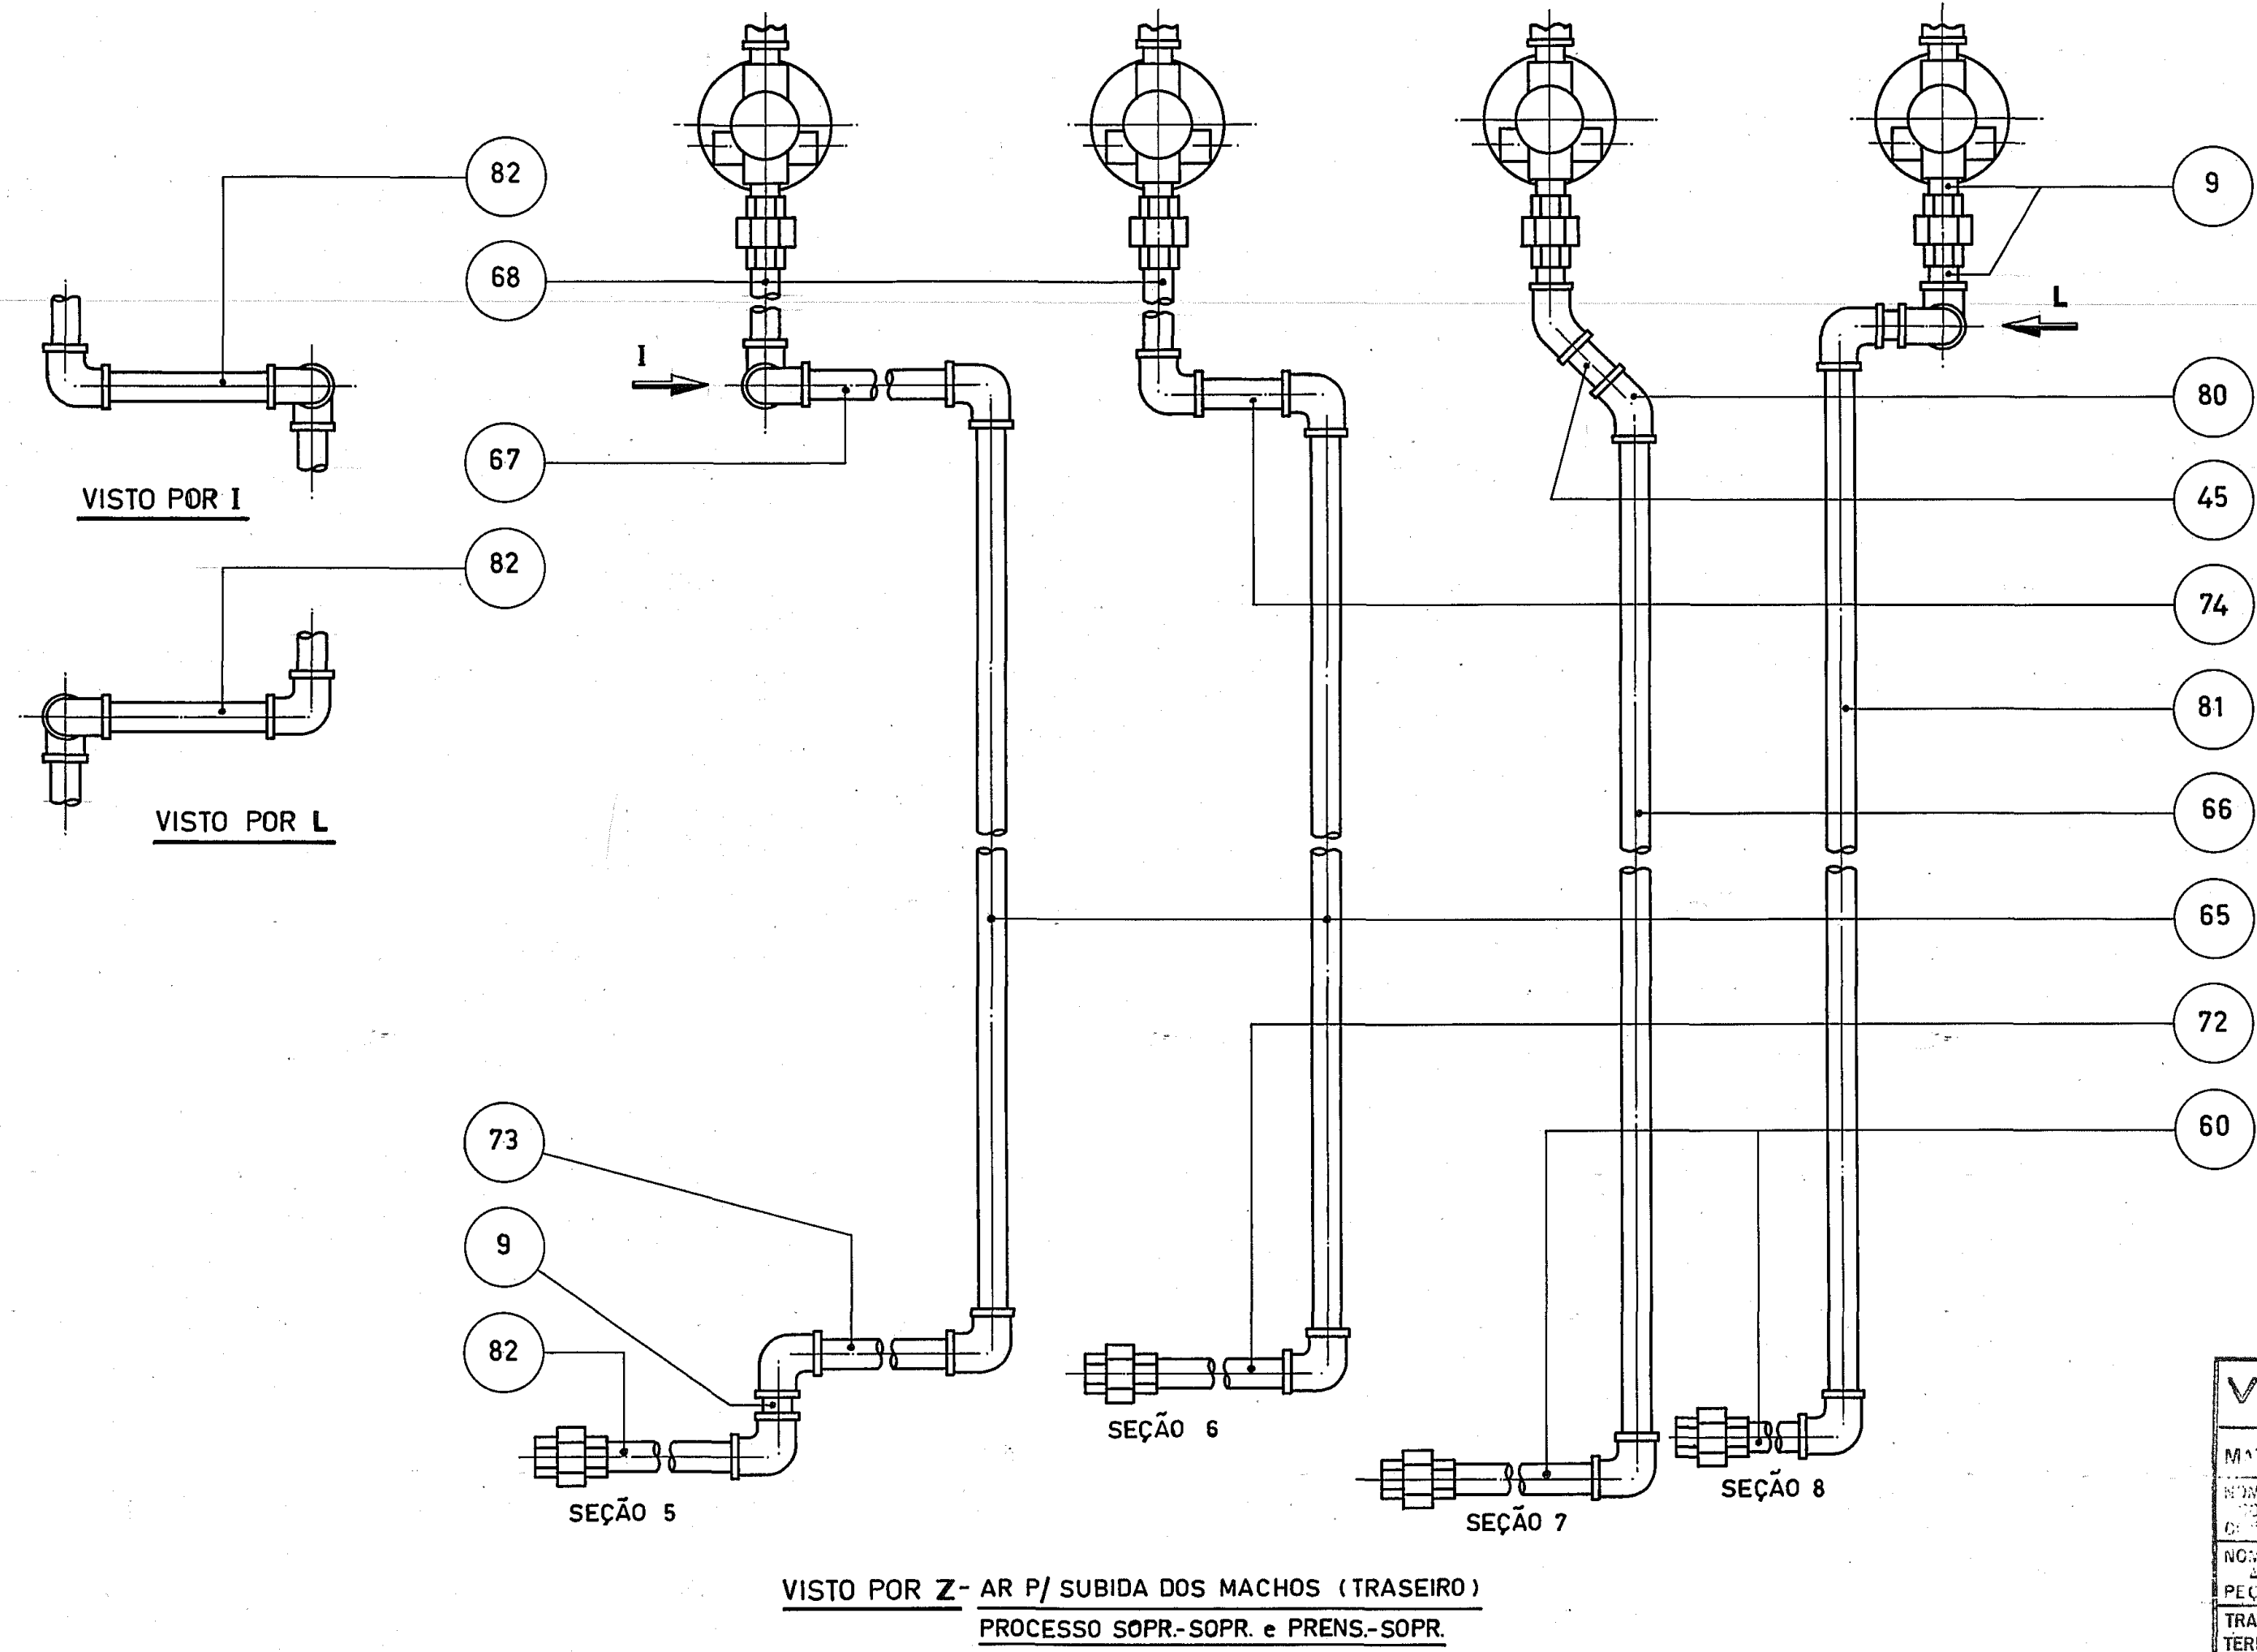
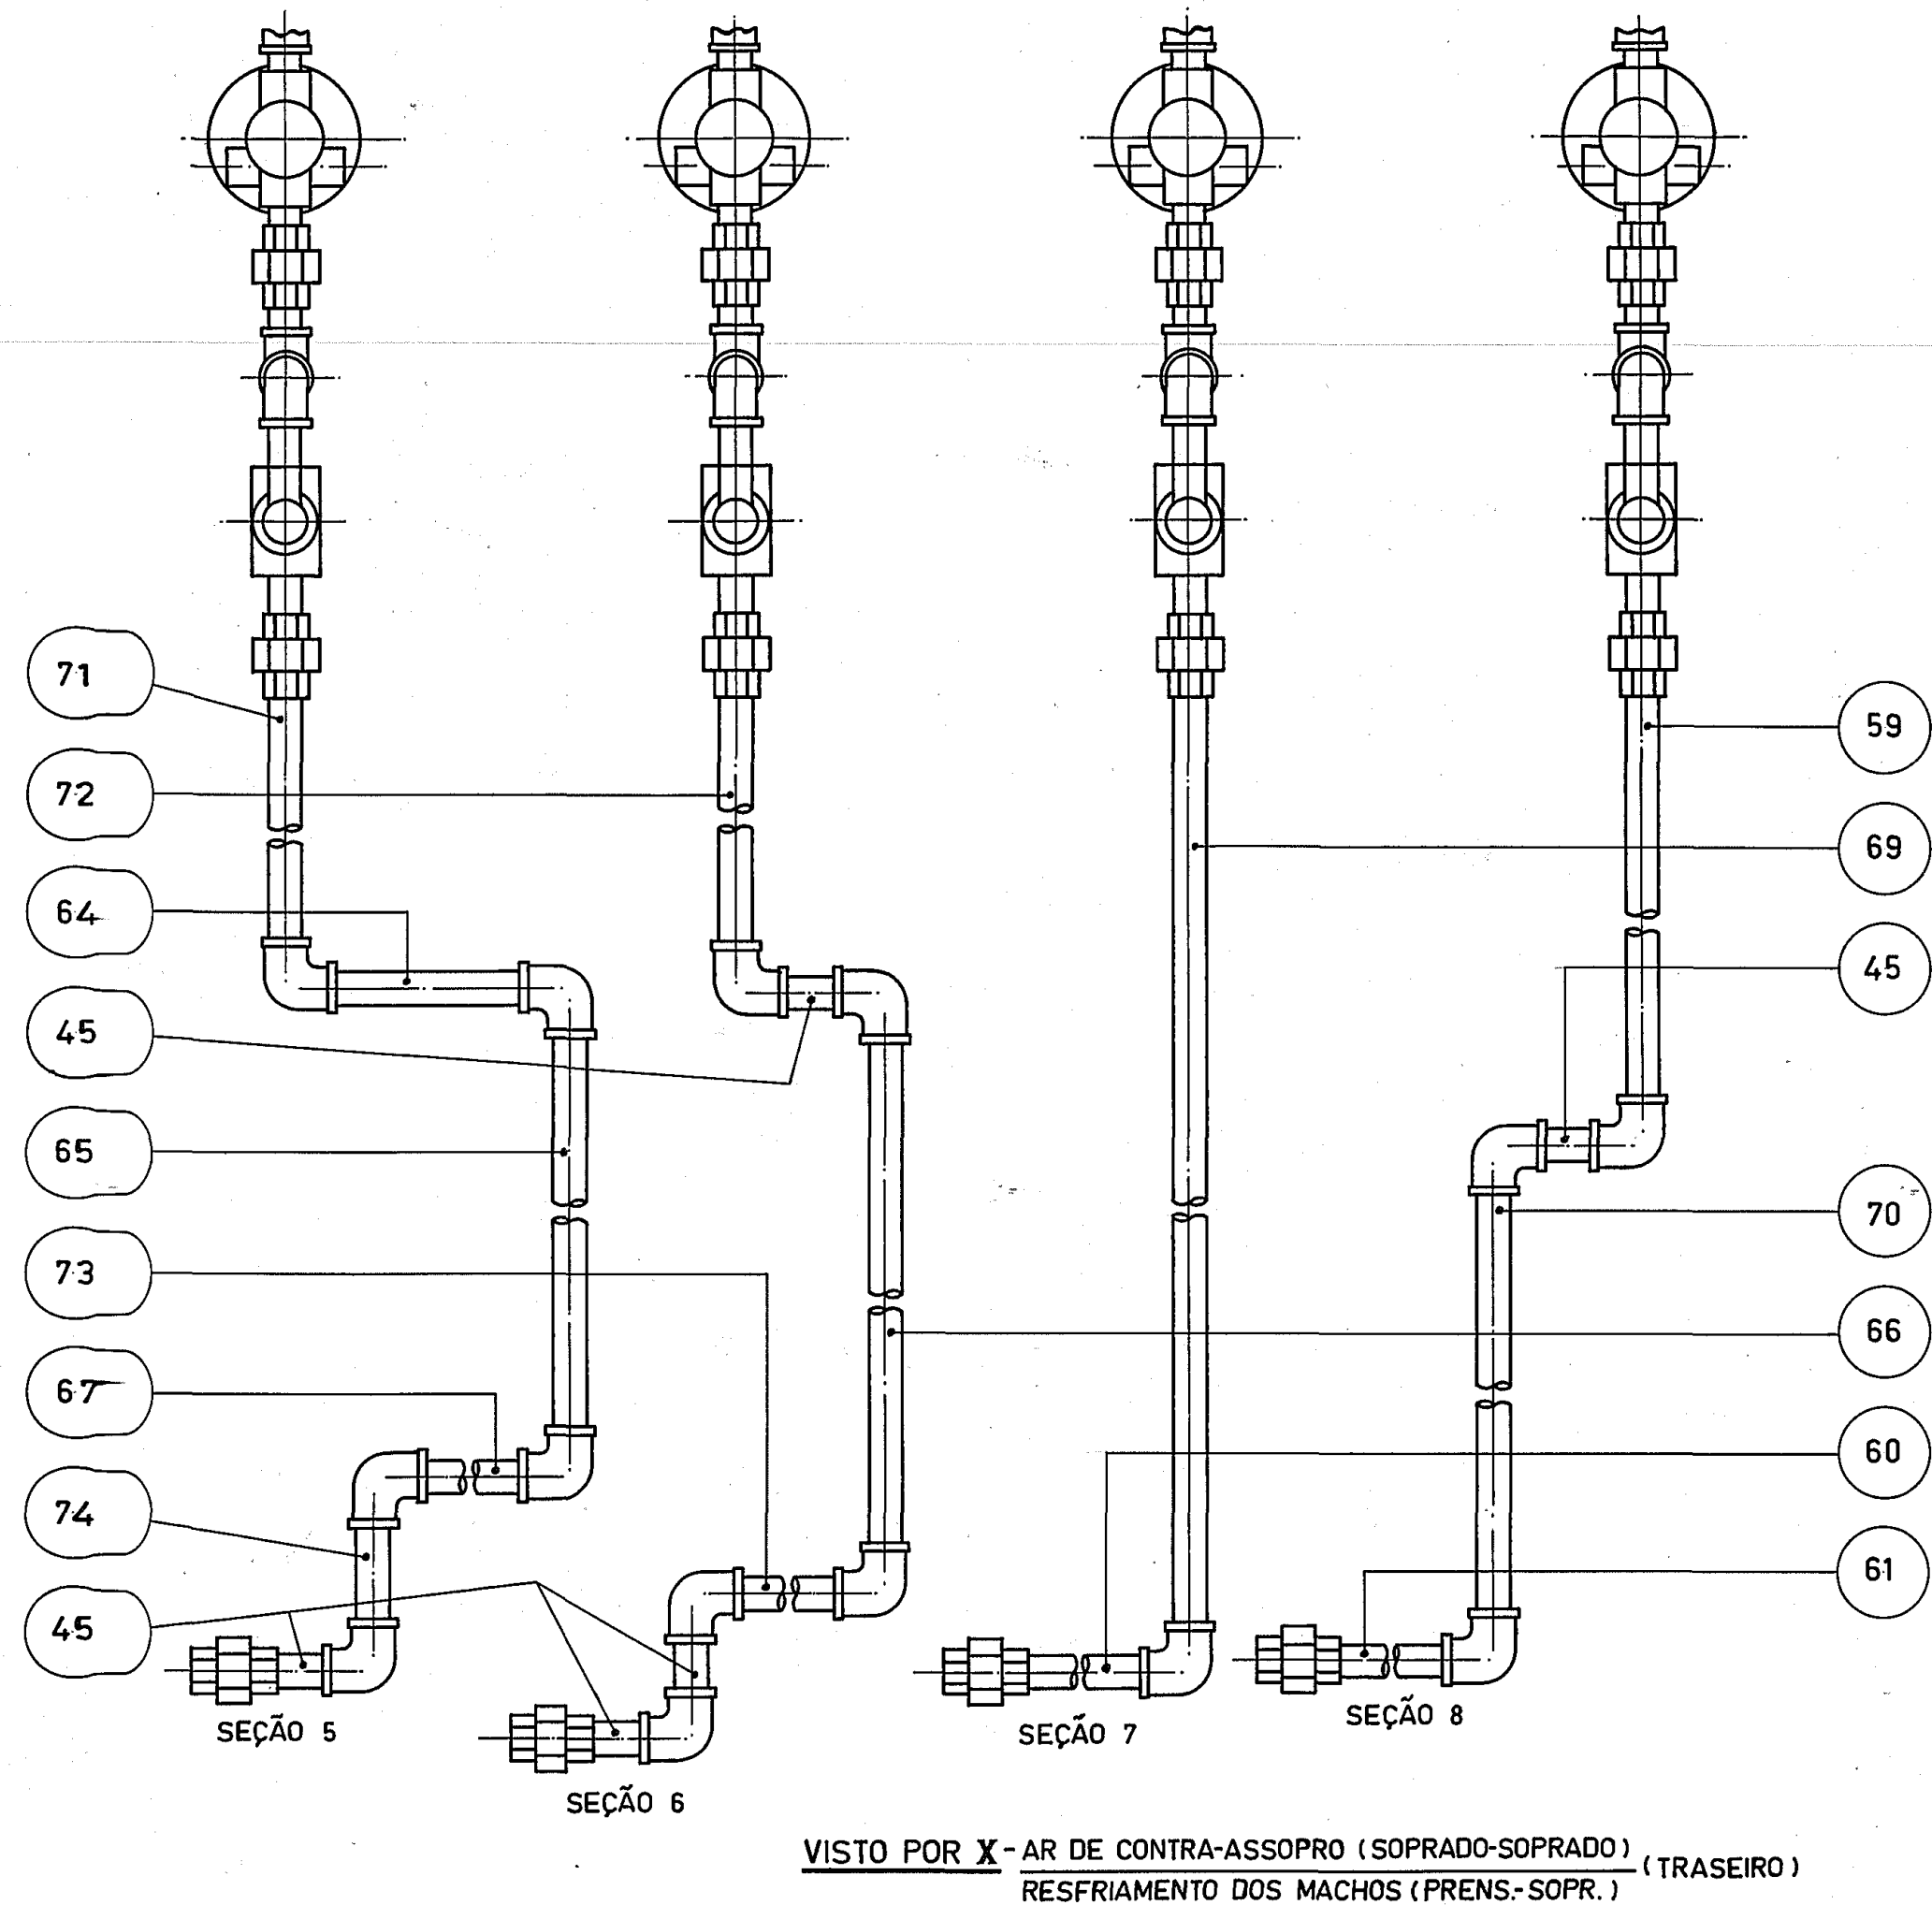
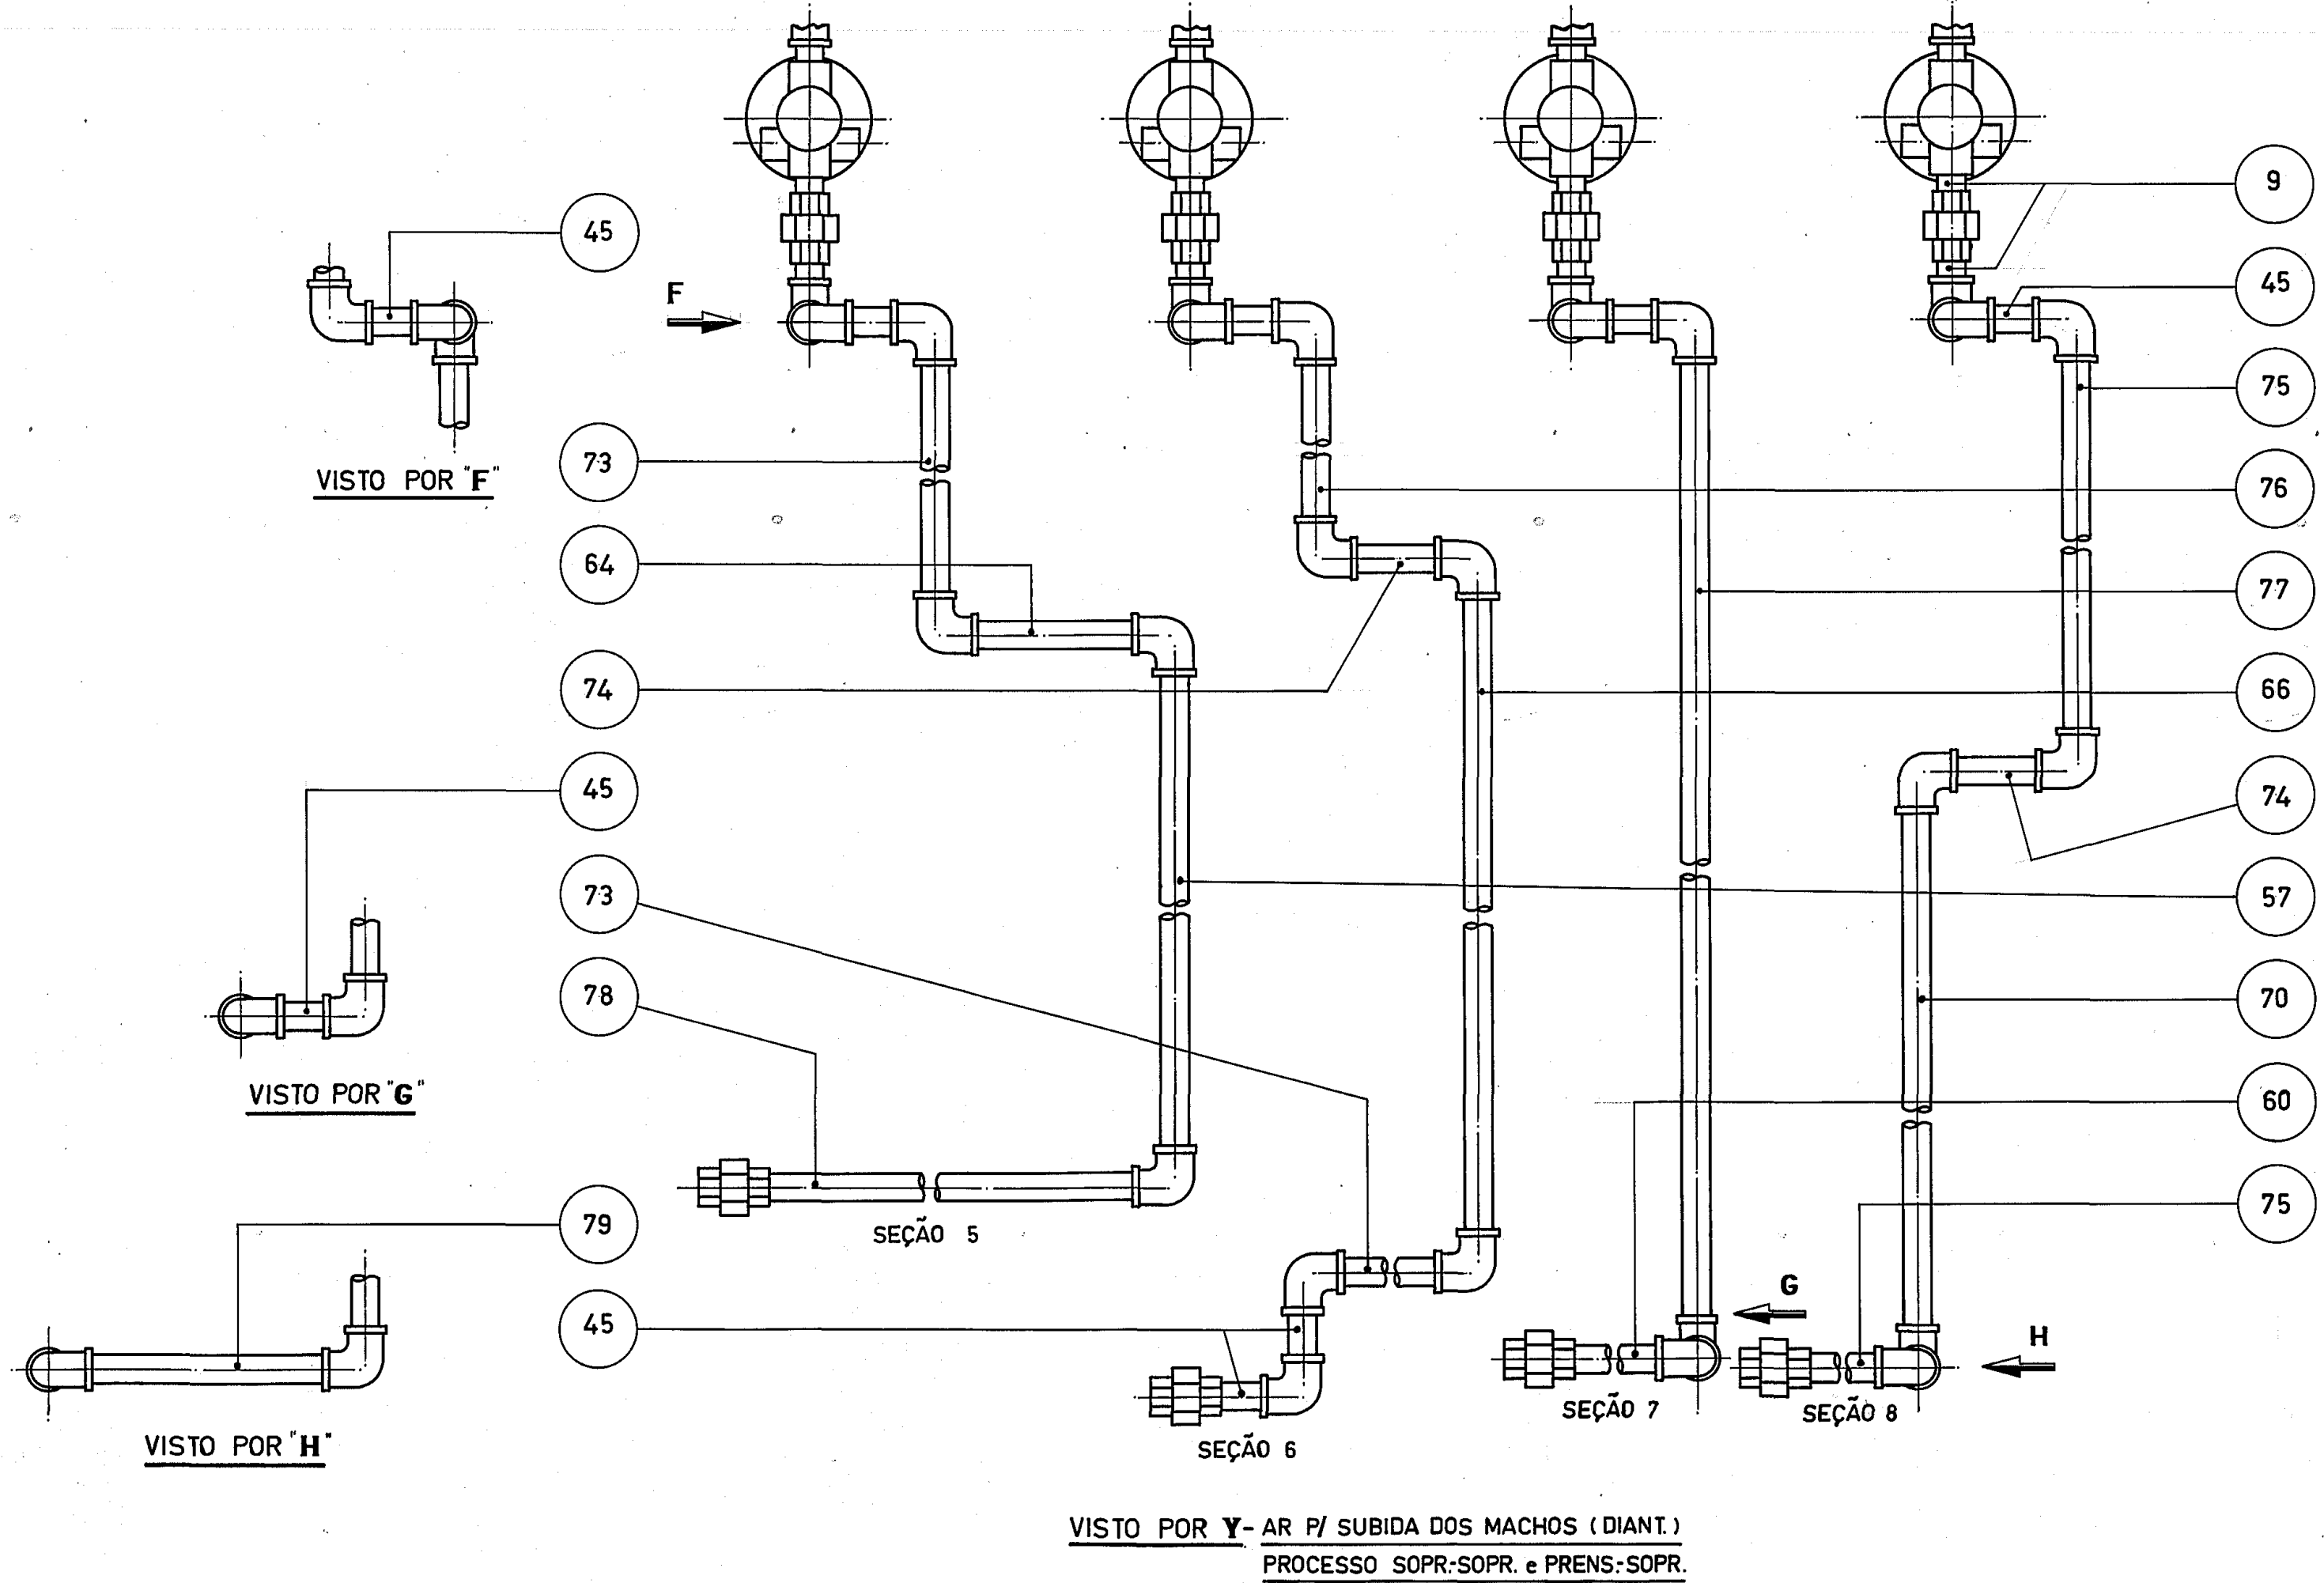


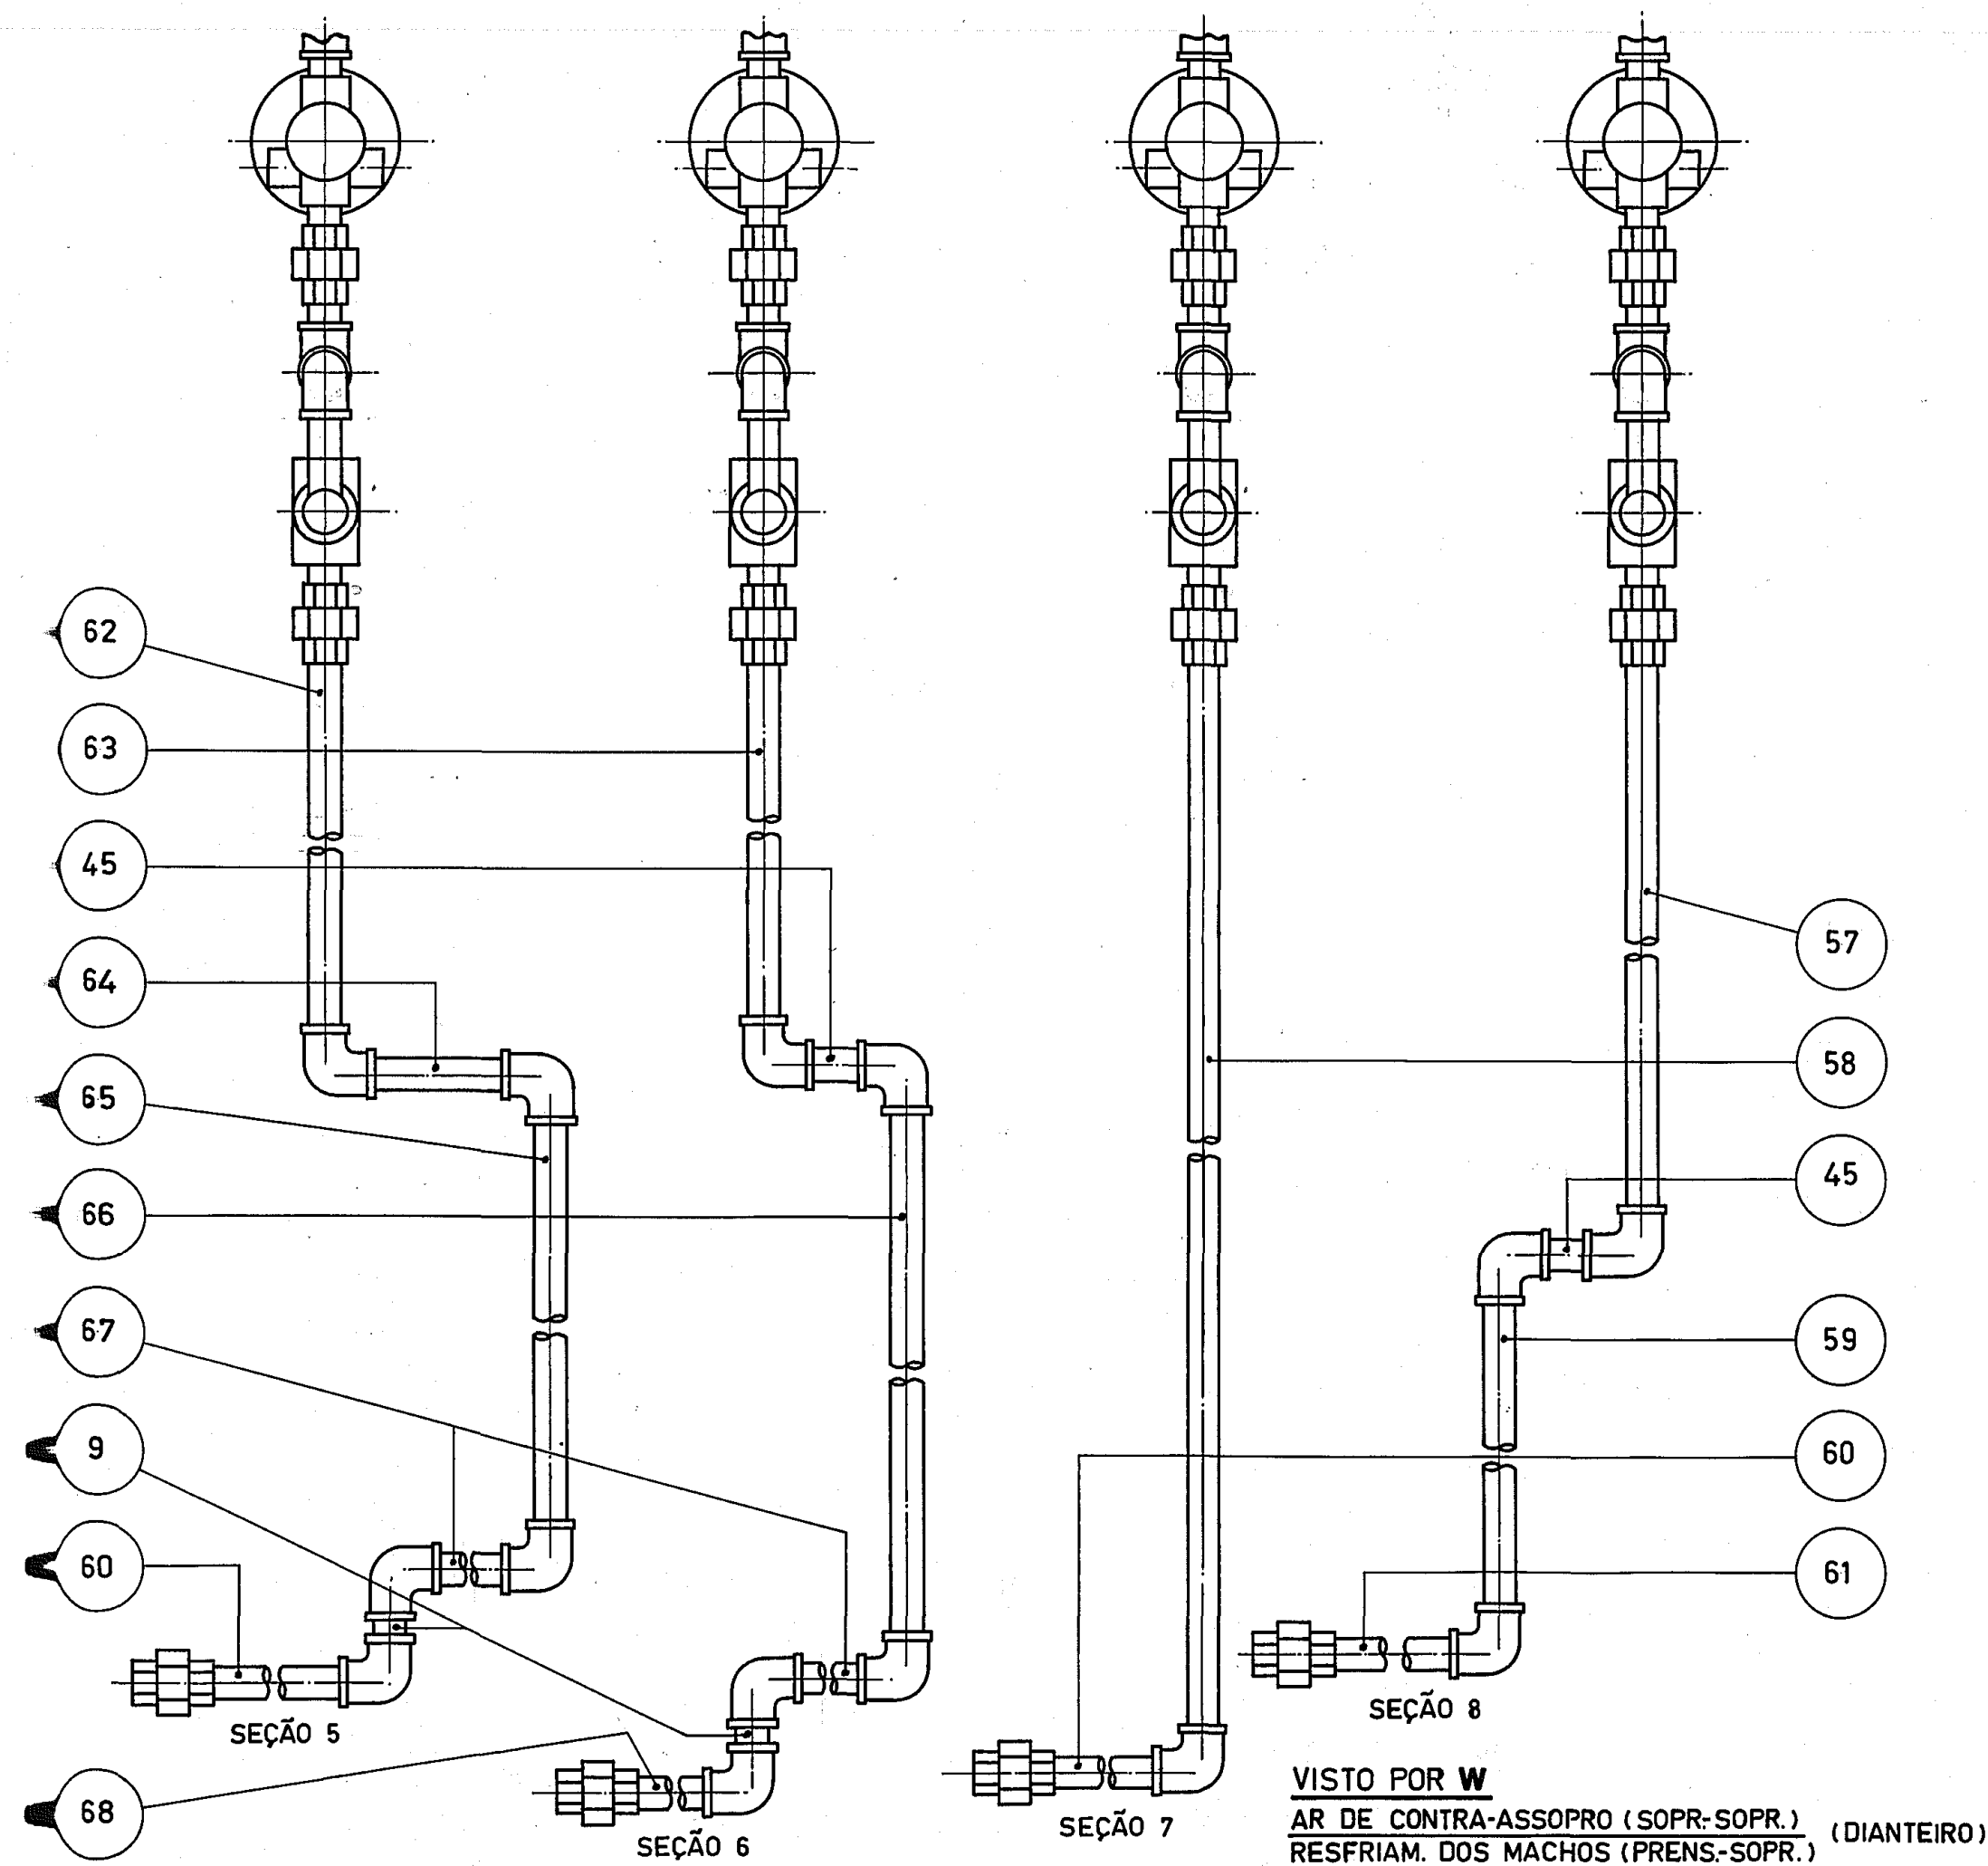

OBS: A TUBULAÇÃO MOSTRADA É P/ MÁQ. DE 8 SEÇÕES. PARA MÁQ. DE 6 SEÇÕES, SUBTRAIR OS ITENS DA SEÇÃO 5.

FOLHA 2 DE 2 FOLHAS.

VIDROS VITON LTDA.		DES. <i>João Carlos</i>
MAT.	Nº DO PROJ.	DATA 12-09-89
NOME PAINEL DE CONTROLE DE AR (LADO DIREITO DA MÁQUINA)	Nº DO PROJ. VVM-417	
WOMEN	N. DA PEÇA	
PEÇA	N.º DO DES.	
TRAT.	ESCALA	
TERM.		