


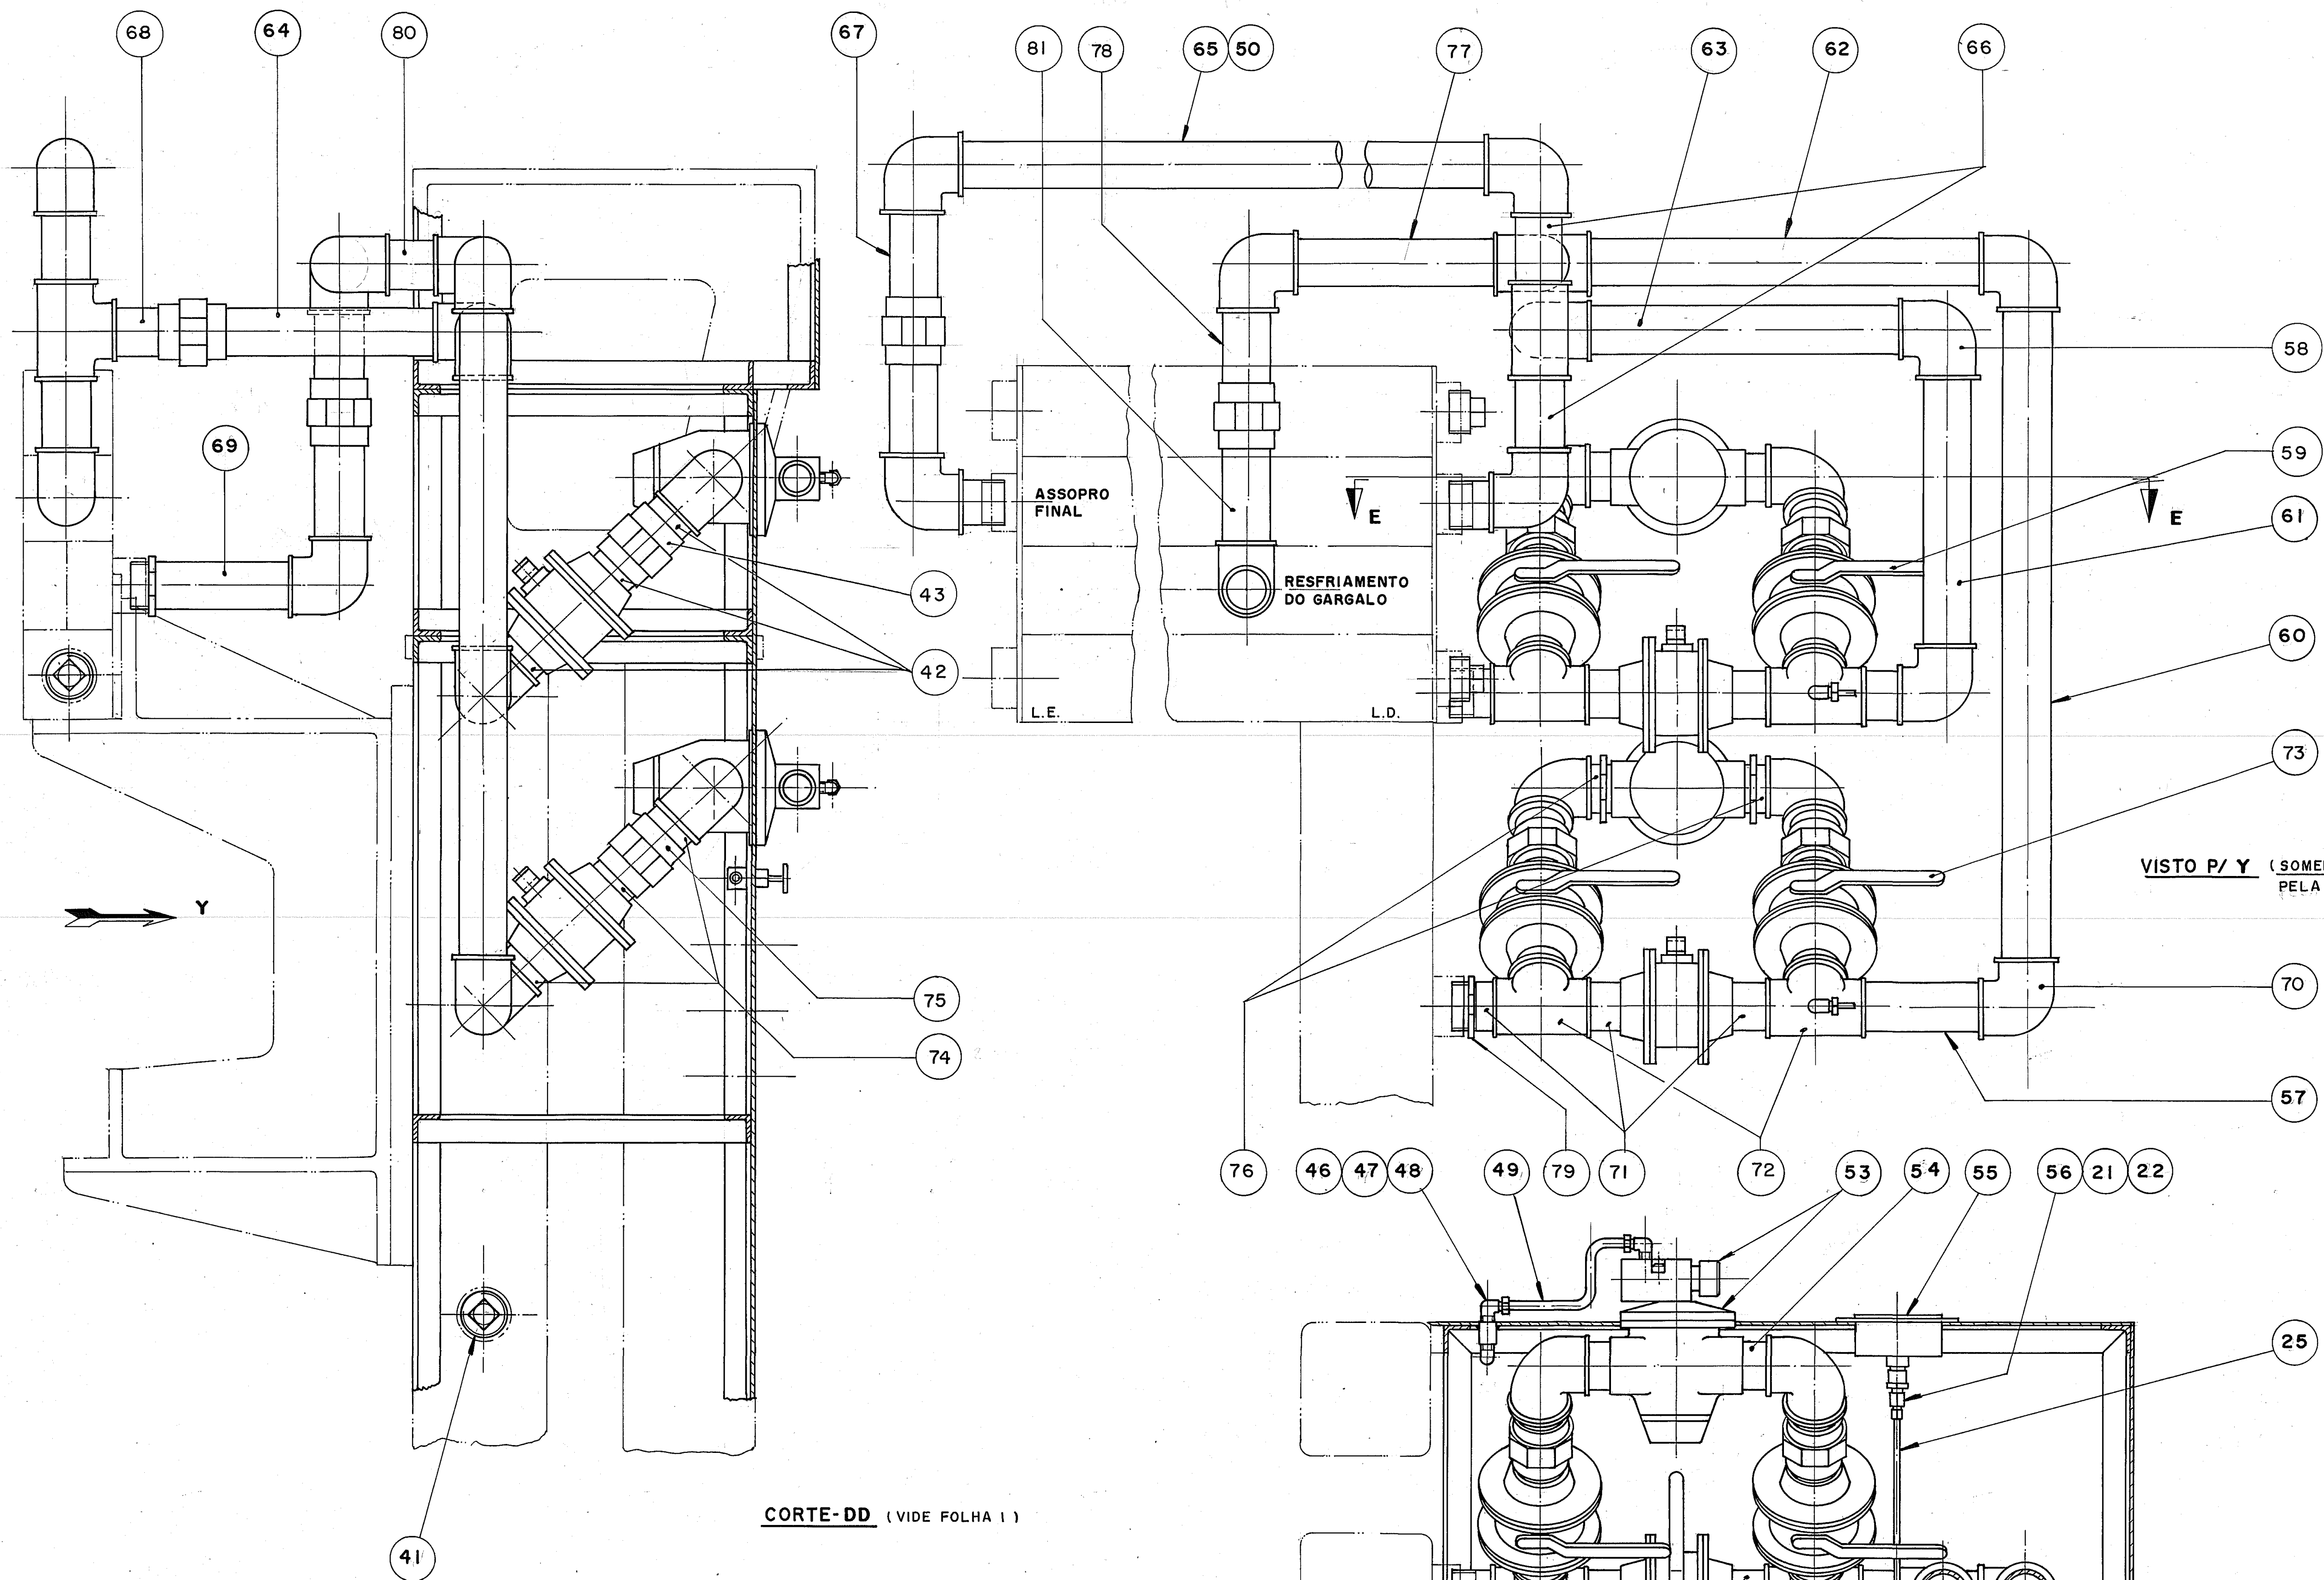

FOLHA 2 DE 2 FOLHAS

VIDROS VITON LTDA.		VER.	
MAT.		DATA	03-08-93
NOME DO PROJETO	MAQ. I.S. 6 & 8 SEÇÕES C/ COLUMNA MANIFOLD	PROJ.	
NOME DA PEÇA	PAINEL DE CONTROLE P/MAQ C/ DIST. G. E MOT. SINC. (L.D.)	M. DA	VVM-548
TRAT.		ESCALA	1/4
TERM.		M. DO DES.	