


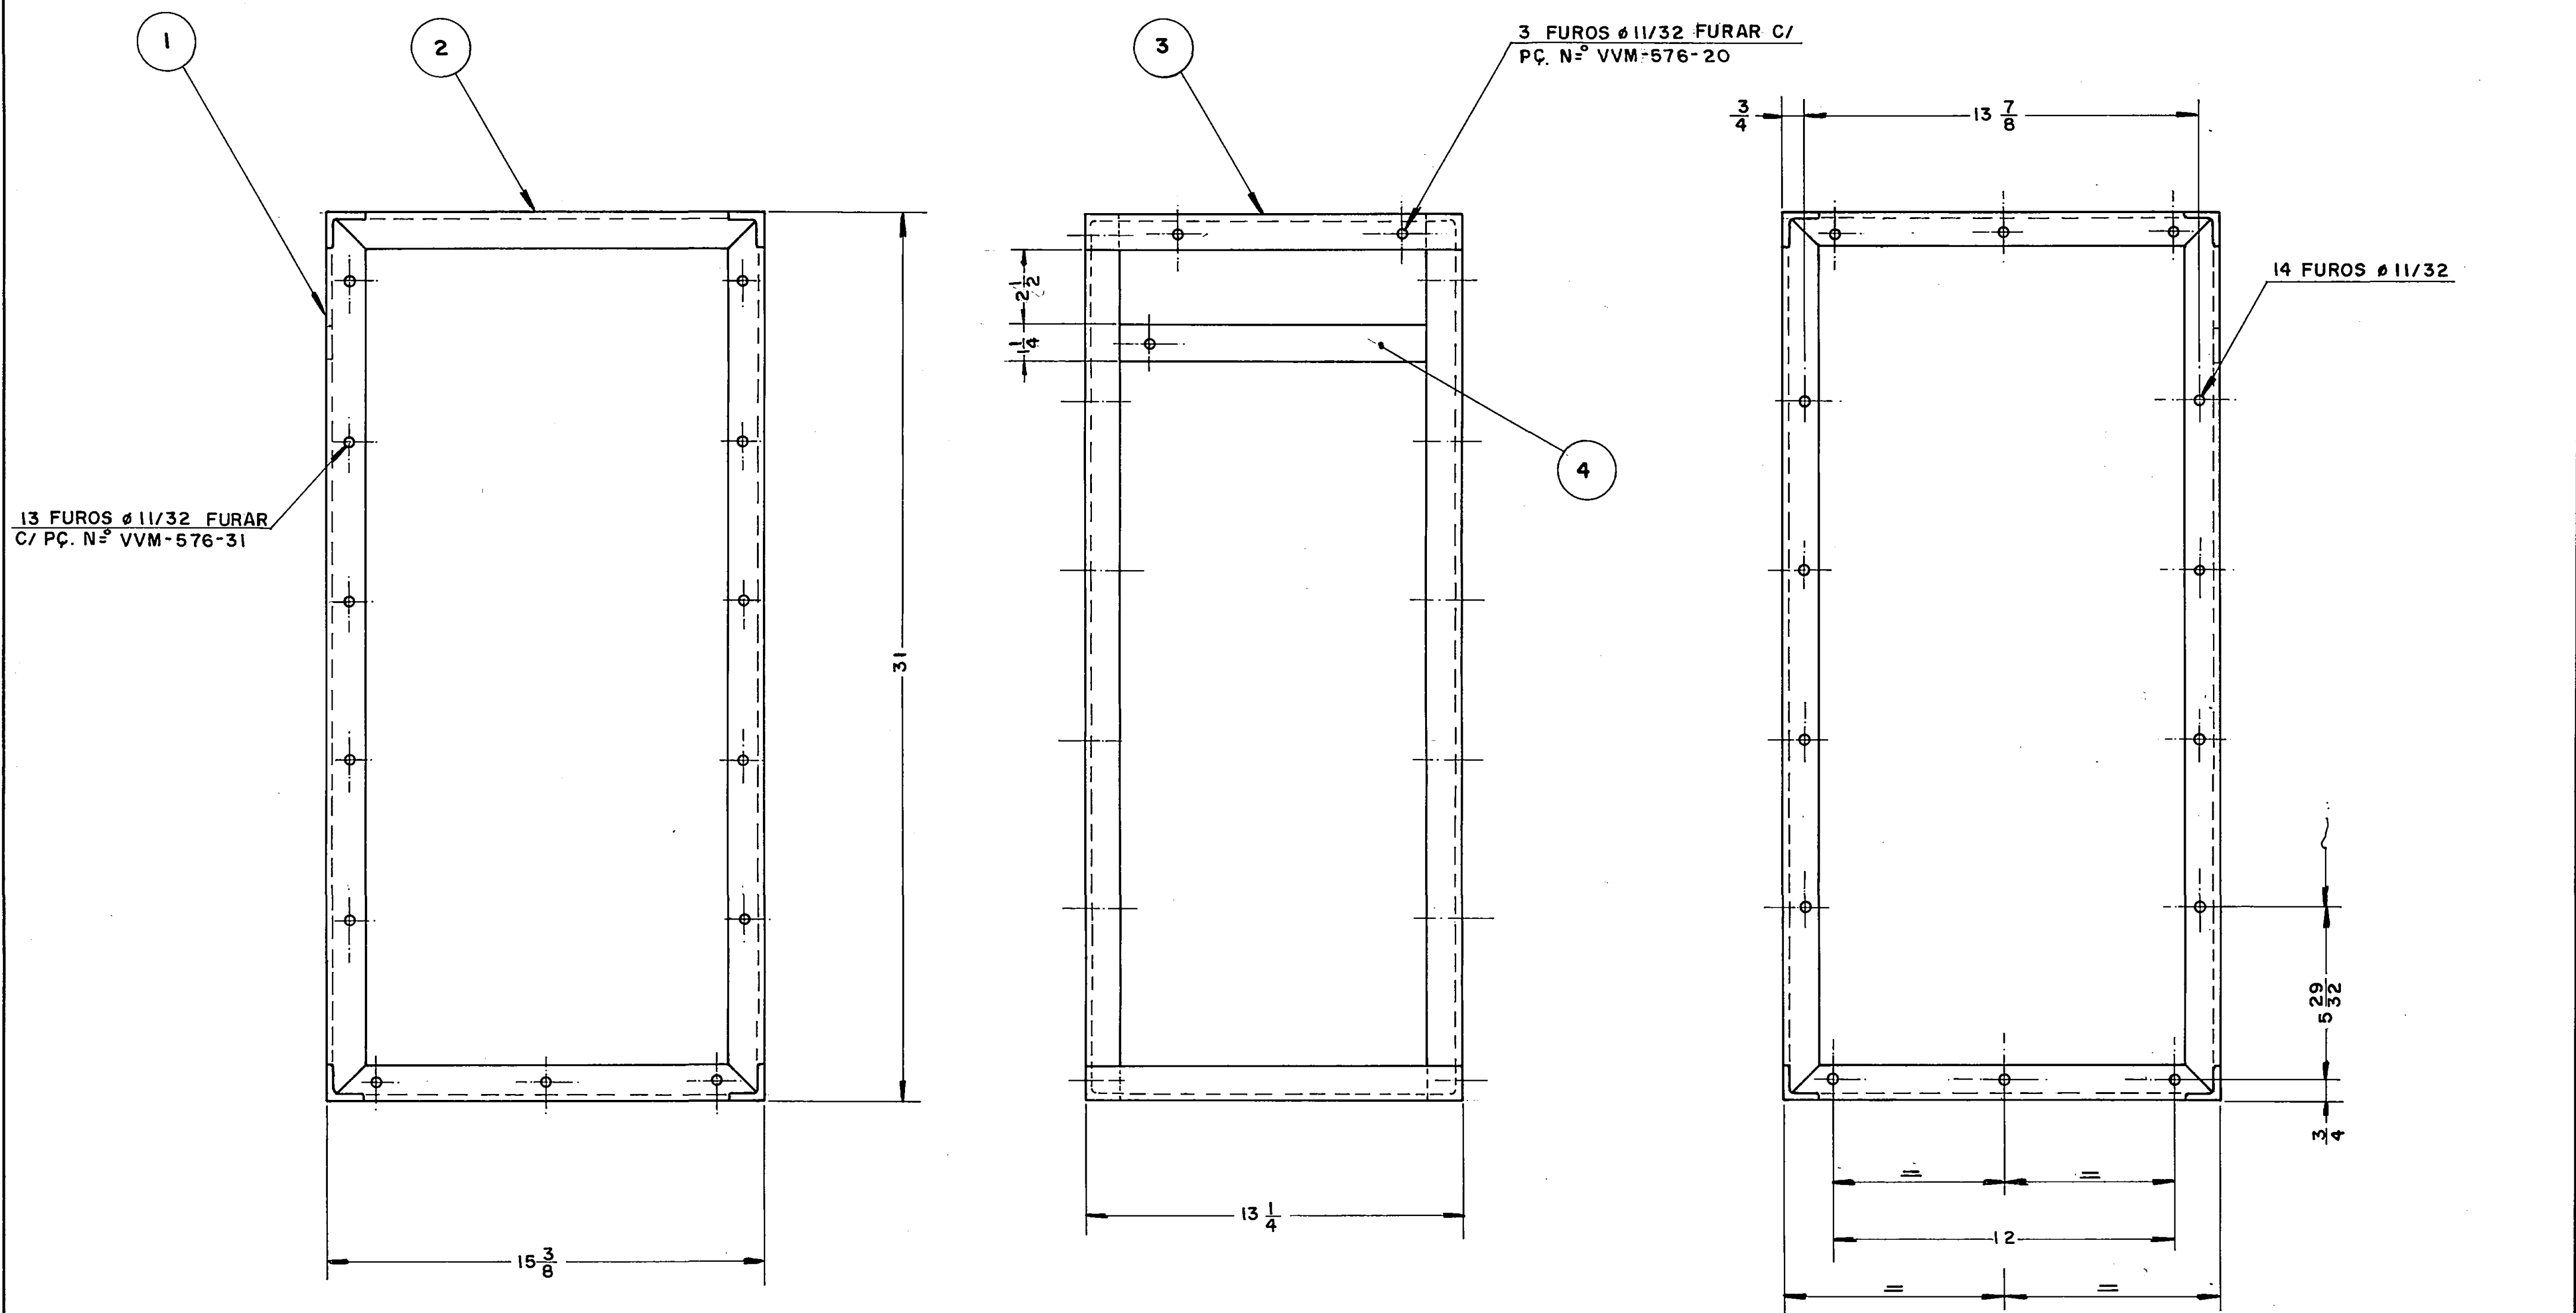

OBS
SOLDAR NAS JUNTAS

QTD	POS	DESCRIÇÃO
1	4	FERRO CHATO DE 1/4 x 1/4 x 10 3/4
4	3	CANTON. DE 1/4 x 1/4 x 1/4 x 13 1/4
4	2	CANTON. DE 1/4 x 1/4 x 1/4 x 15 3/8
4	1	CANTON. DE 1/4 x 1/4 x 1/4 x 31

DATA	REVISÃO	ITEM	20-08-93	VIDROS VITON LTDA.
			TOLERÂNCIAS STANDARD PARA SUPERFÍCIES USINADAS SEM TOLERÂNCIA INDICADA	MAT. VIDE TABELA
			DECIMAL $\pm$ 0,05"	NOME DO CONJ. ESTRUTURA DO PAINEL
			FRAÇÃO	NOME DA PEÇA ESTRUTURA INTERMEDIÁRIA
			DE 0" ATÉ 5" $\pm$ 1/64	1/4"
			DE 5" ATÉ 24" $\pm$ 1/32	
			ACIMA DE 24" $\pm$ 1/16	