

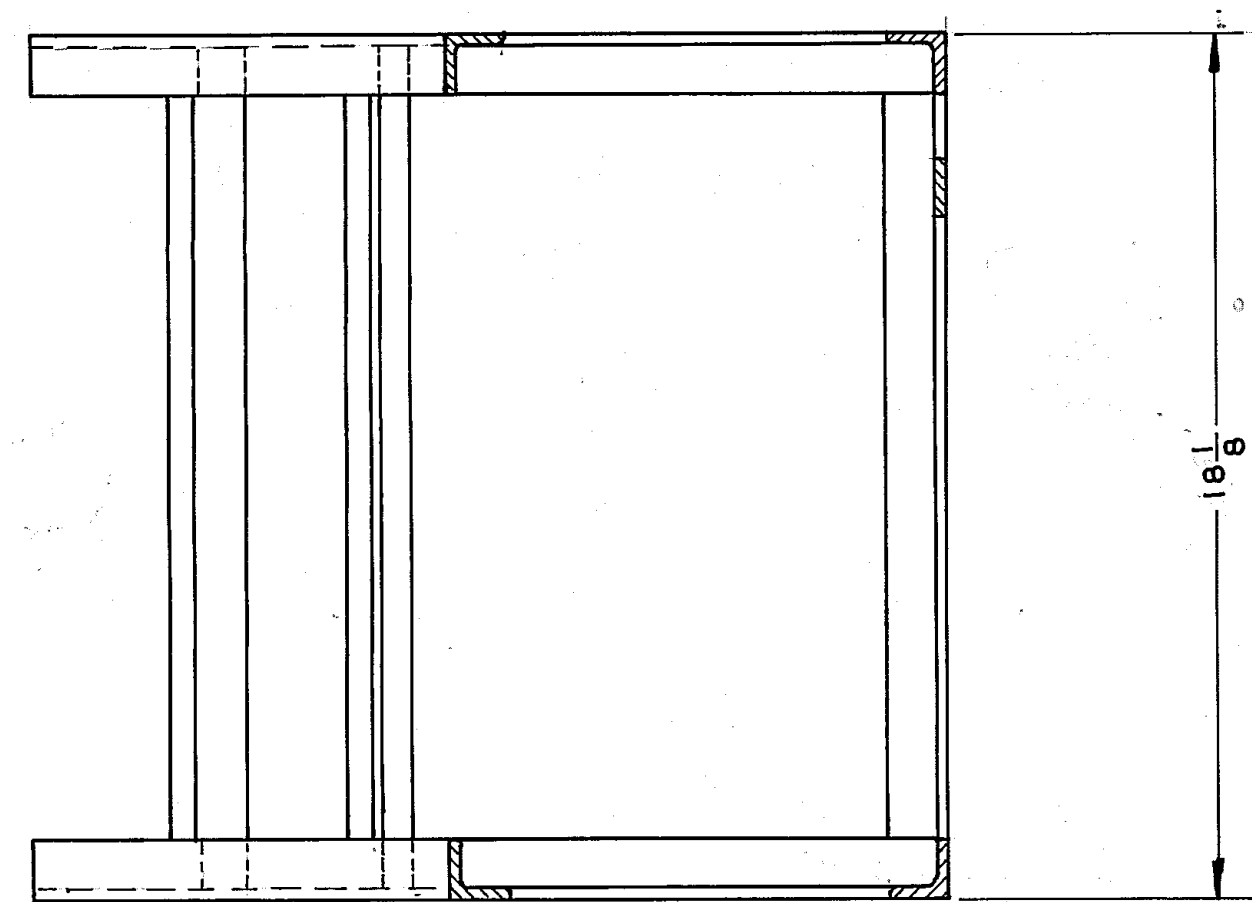


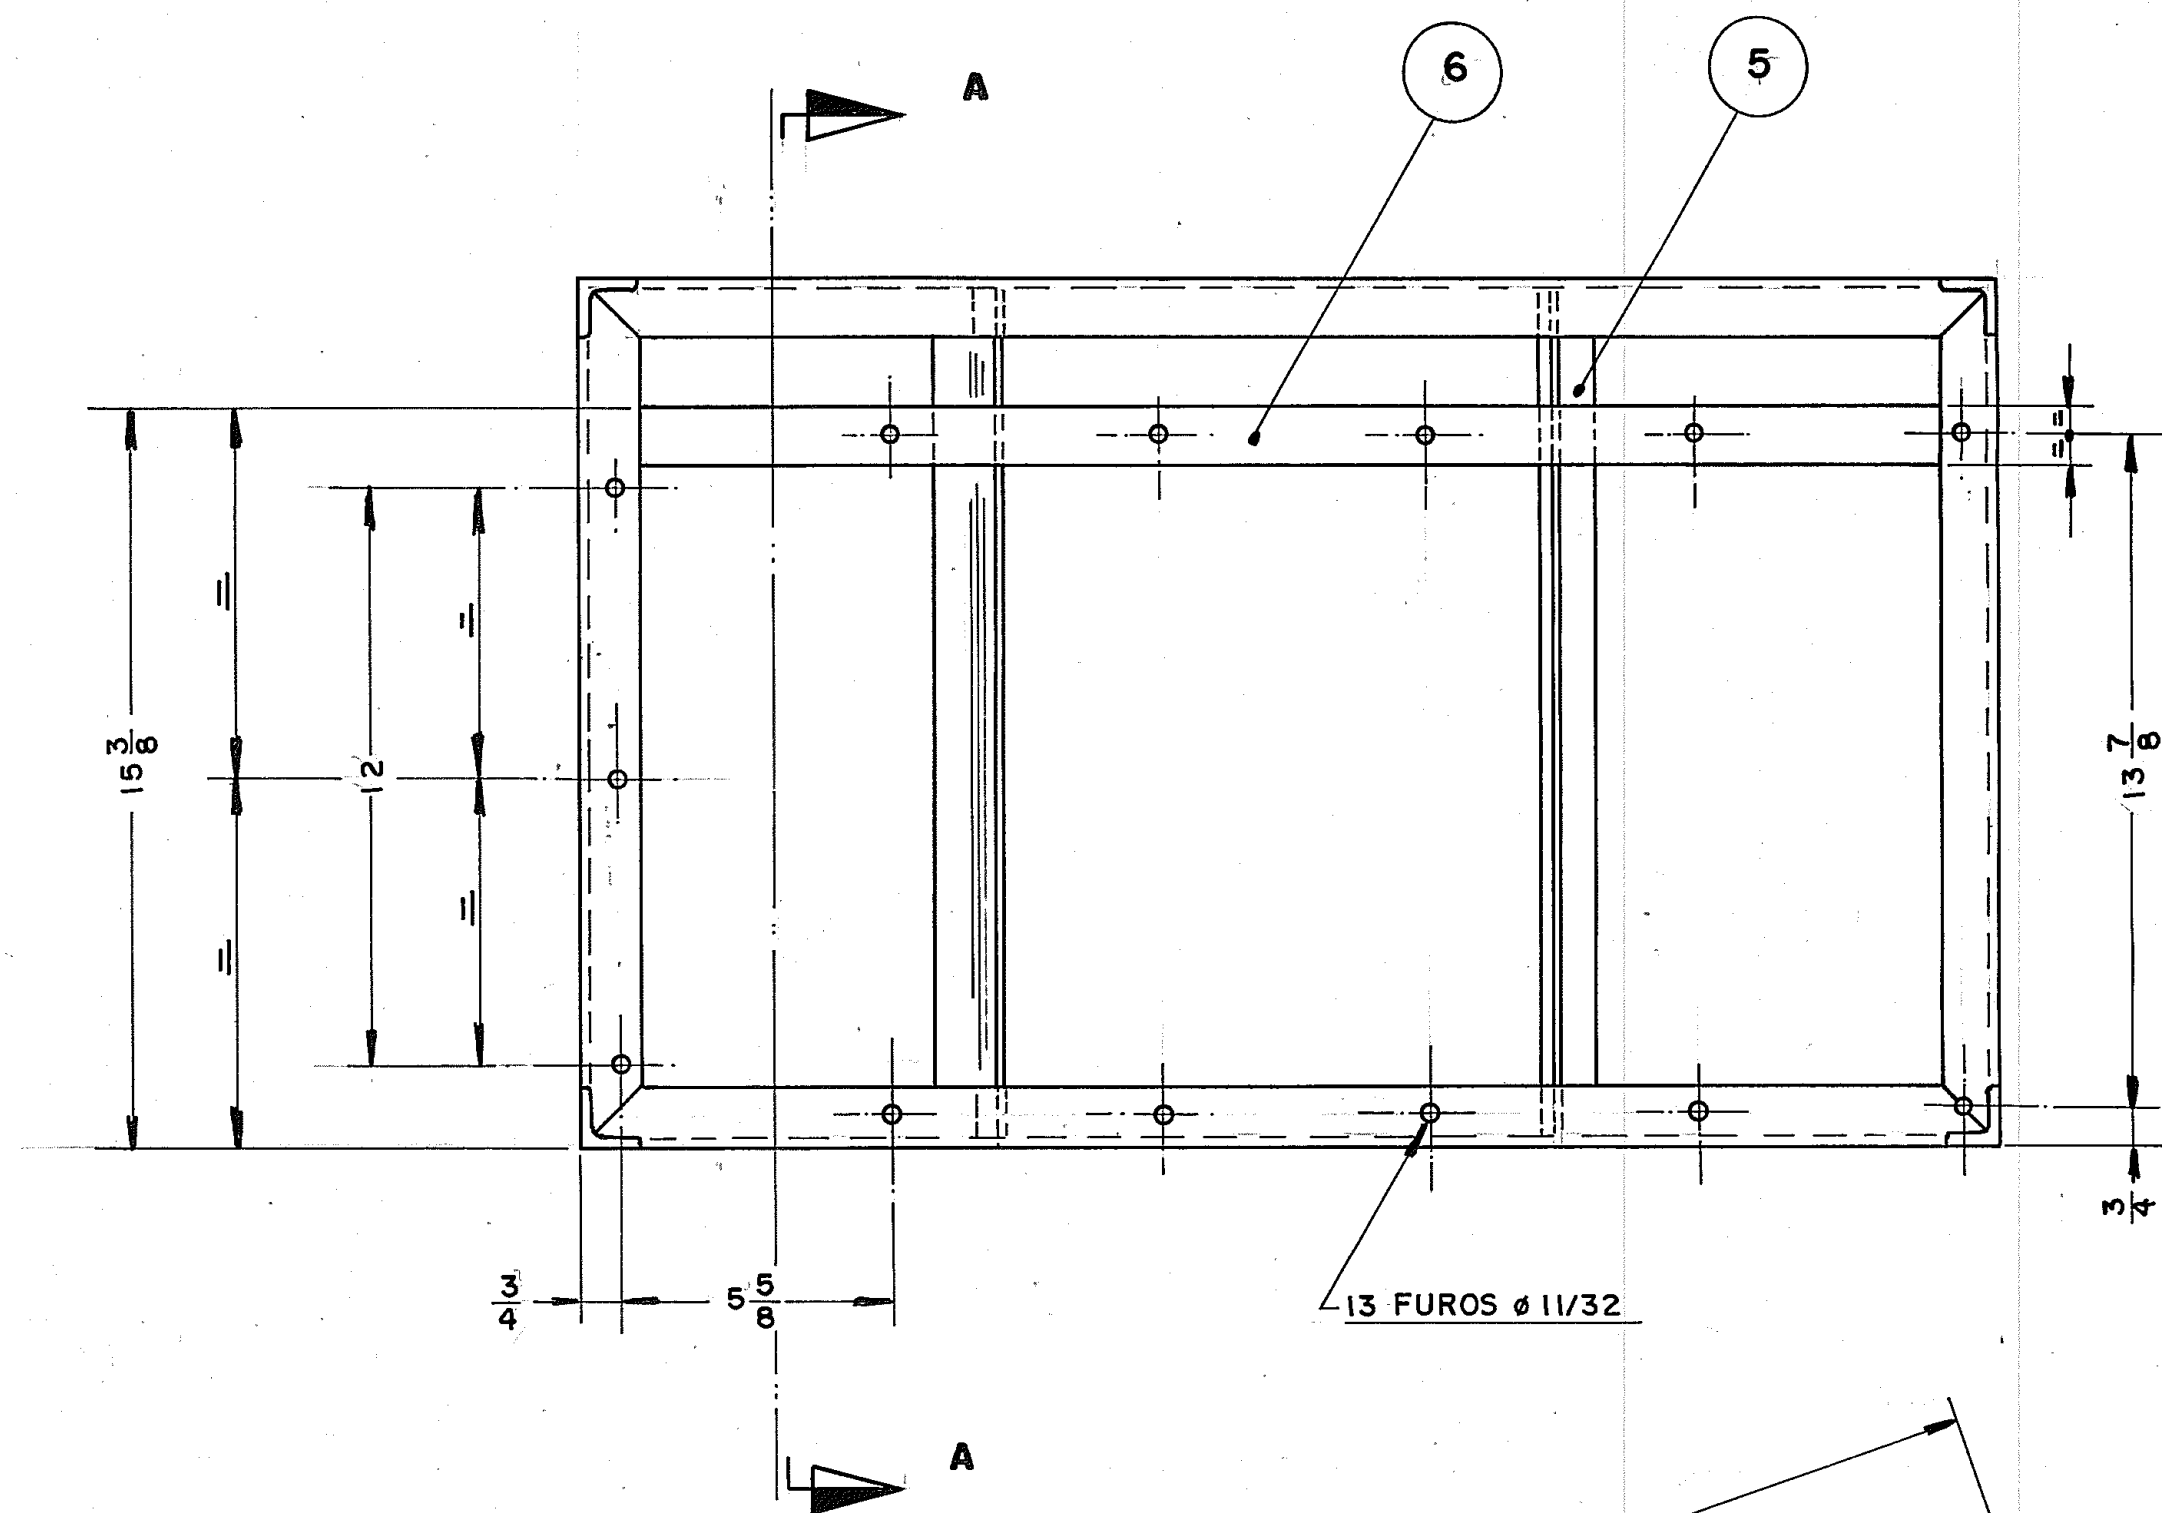

CORTE-AA

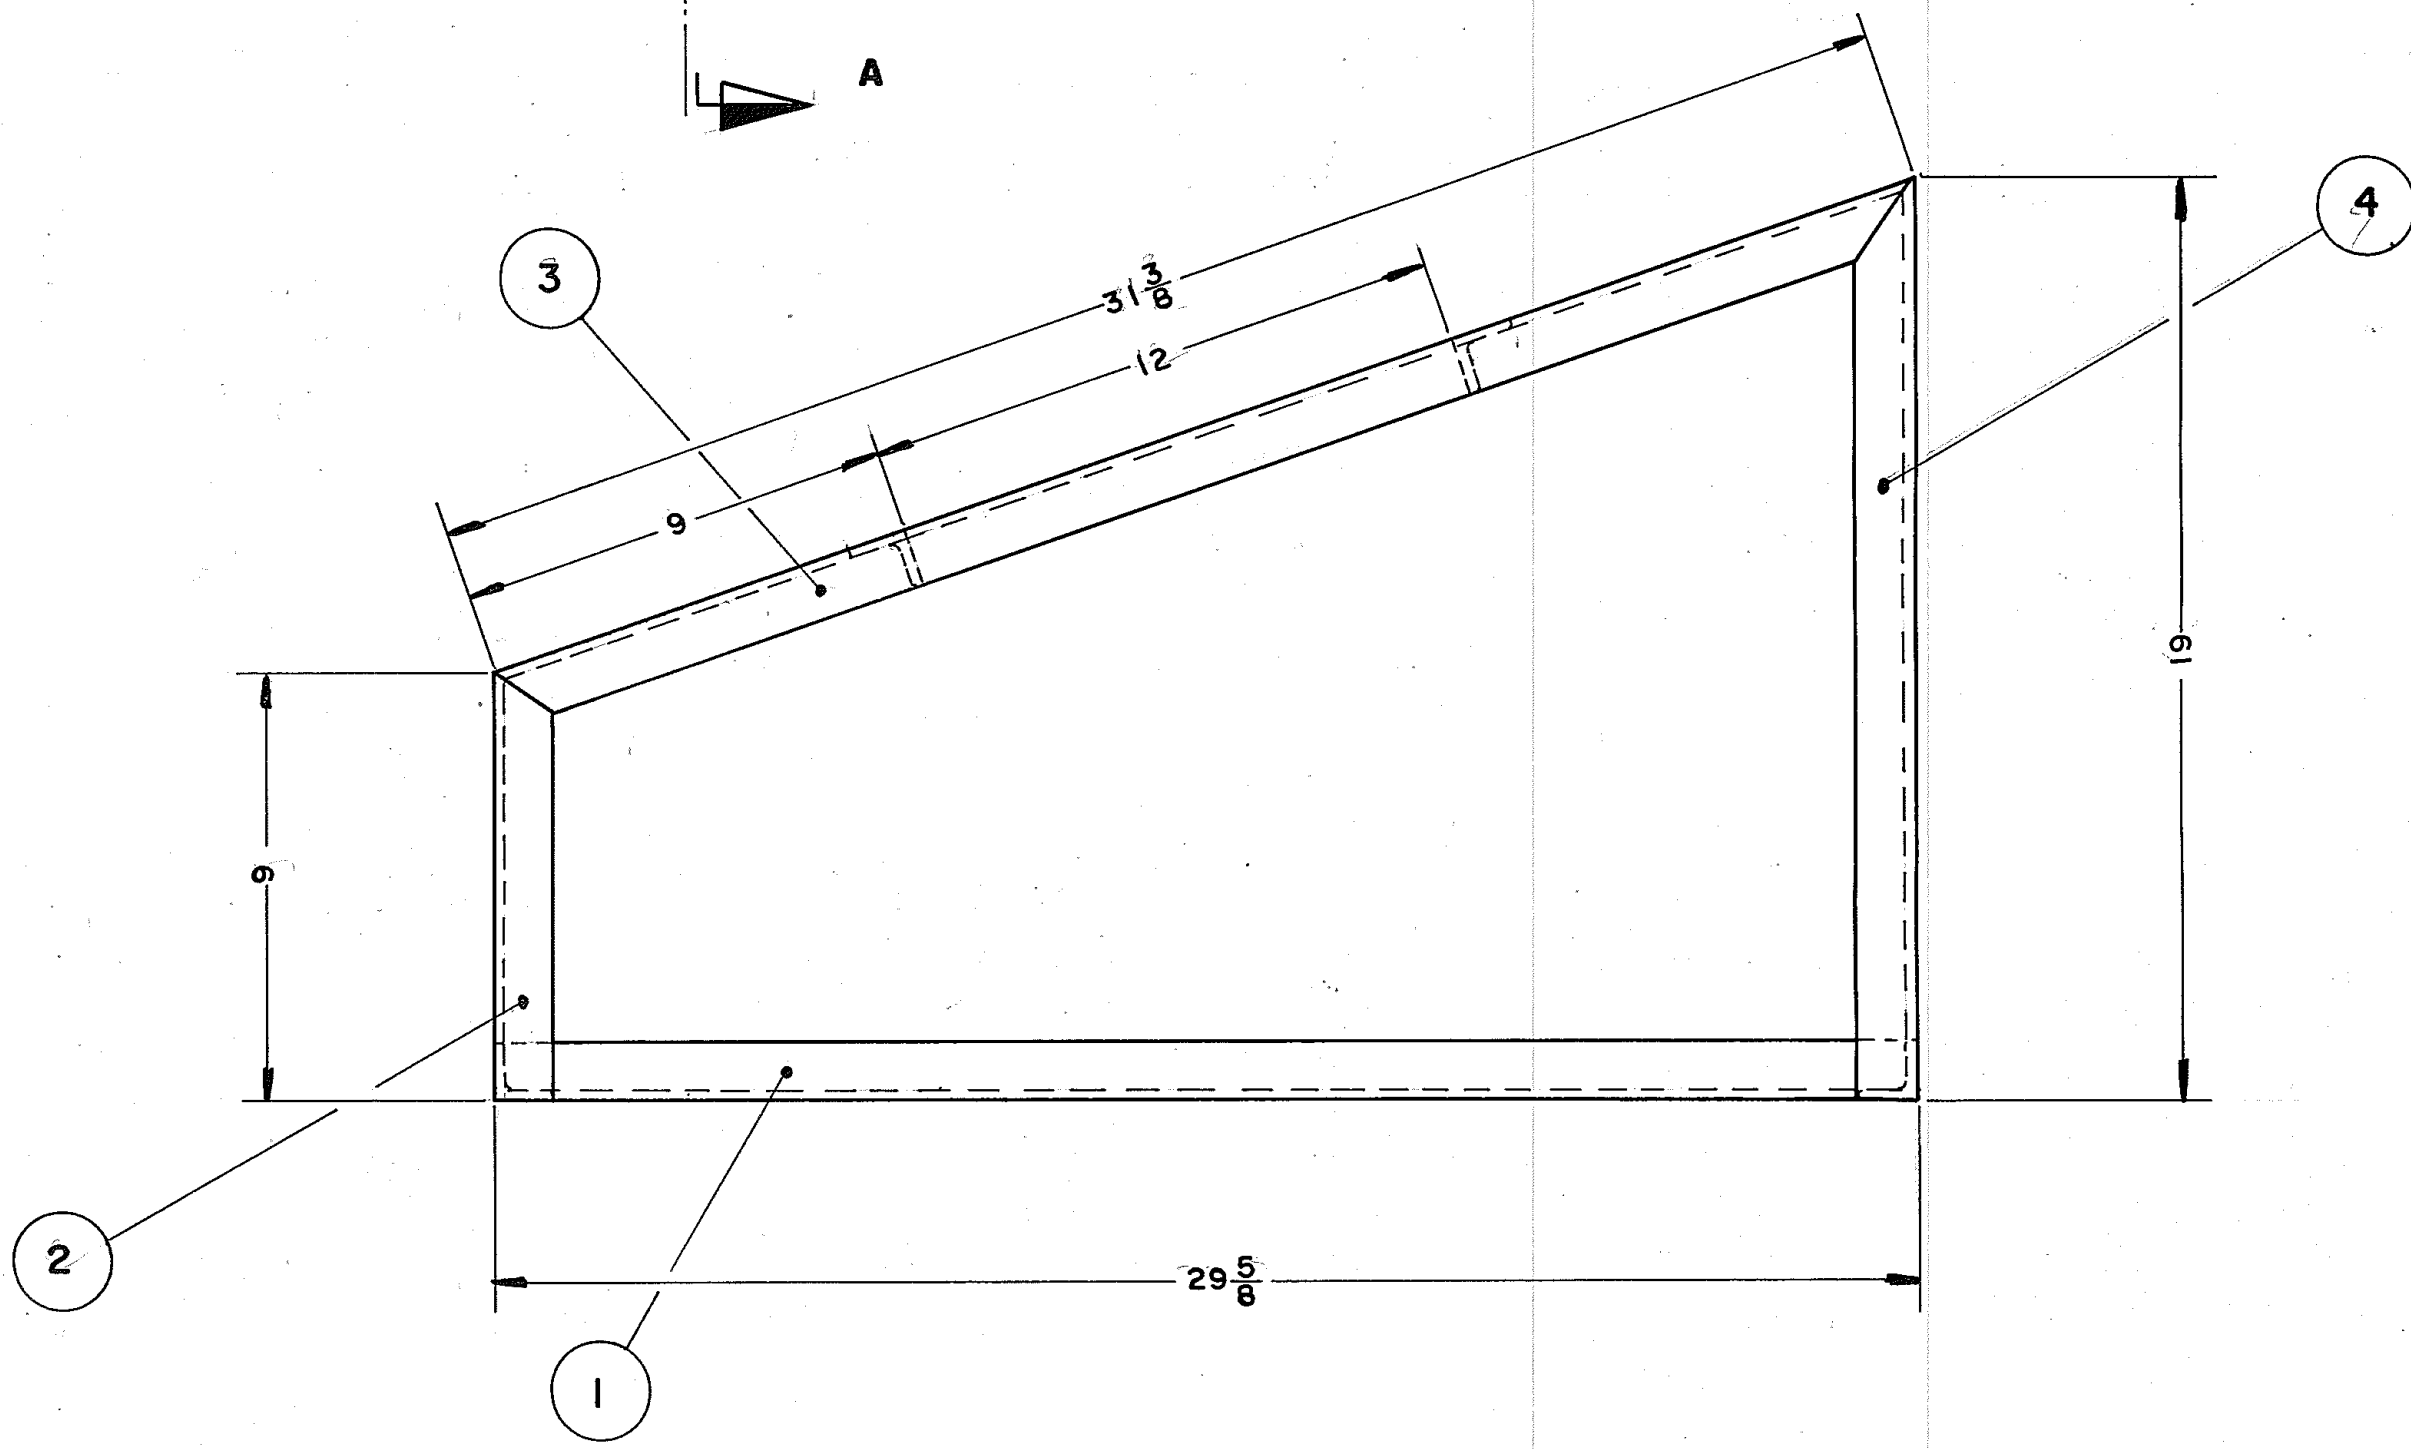

QTD	POS	DESCRIÇÃO
2	8	CANTON. DE 1/4 x 1/4 x 1/4 x 18 1/8
1	6	FERRO CHATO DE 1/4 x 1/4 x 27 1/8
2	5	CANTON. DE 1/4 x 1/4 x 1/4 x 17 5/8
2	4	CANTON. DE 1/4 x 1/4 x 1/4 x 19
2	3	CANTON. DE 1/4 x 1/4 x 1/4 x 31 3/8
2	2	CANTON. DE 1/4 x 1/4 x 1/4 x 9
2	1	CANTON. DE 1/4 x 1/4 x 1/4 x 29 5/8

OBS.
SOLDAR NAS JUNTAS

DATA: 23-08-93		VIDROS VITON LTDA.		ES. <i>M. S. D.</i>
TOLERANCIAS STANDARD PARA SUPERFICIES USINADAS SEM TOLERANCIA INDICADA		M.T. VIDE TABELA		VEP.
DECIMAL ± 005"		NOME DO CONJ. ESTRUTURA DO PAINEL		N.º DO CONJ. VVM-576
FRAÇÃO		NOME DA P.F. CA ESTRUTURA SUPERIOR		N.º DA P.F. CA VVM-576-31
DE 0" ATÉ 5" ± 1/64		TRAT. TERM.		N.º DO P.F. CA
DE 5" ATÉ 24" ± 1/32		ESCALA 1/4		
ACIMA DE 24" ± 1/16				