


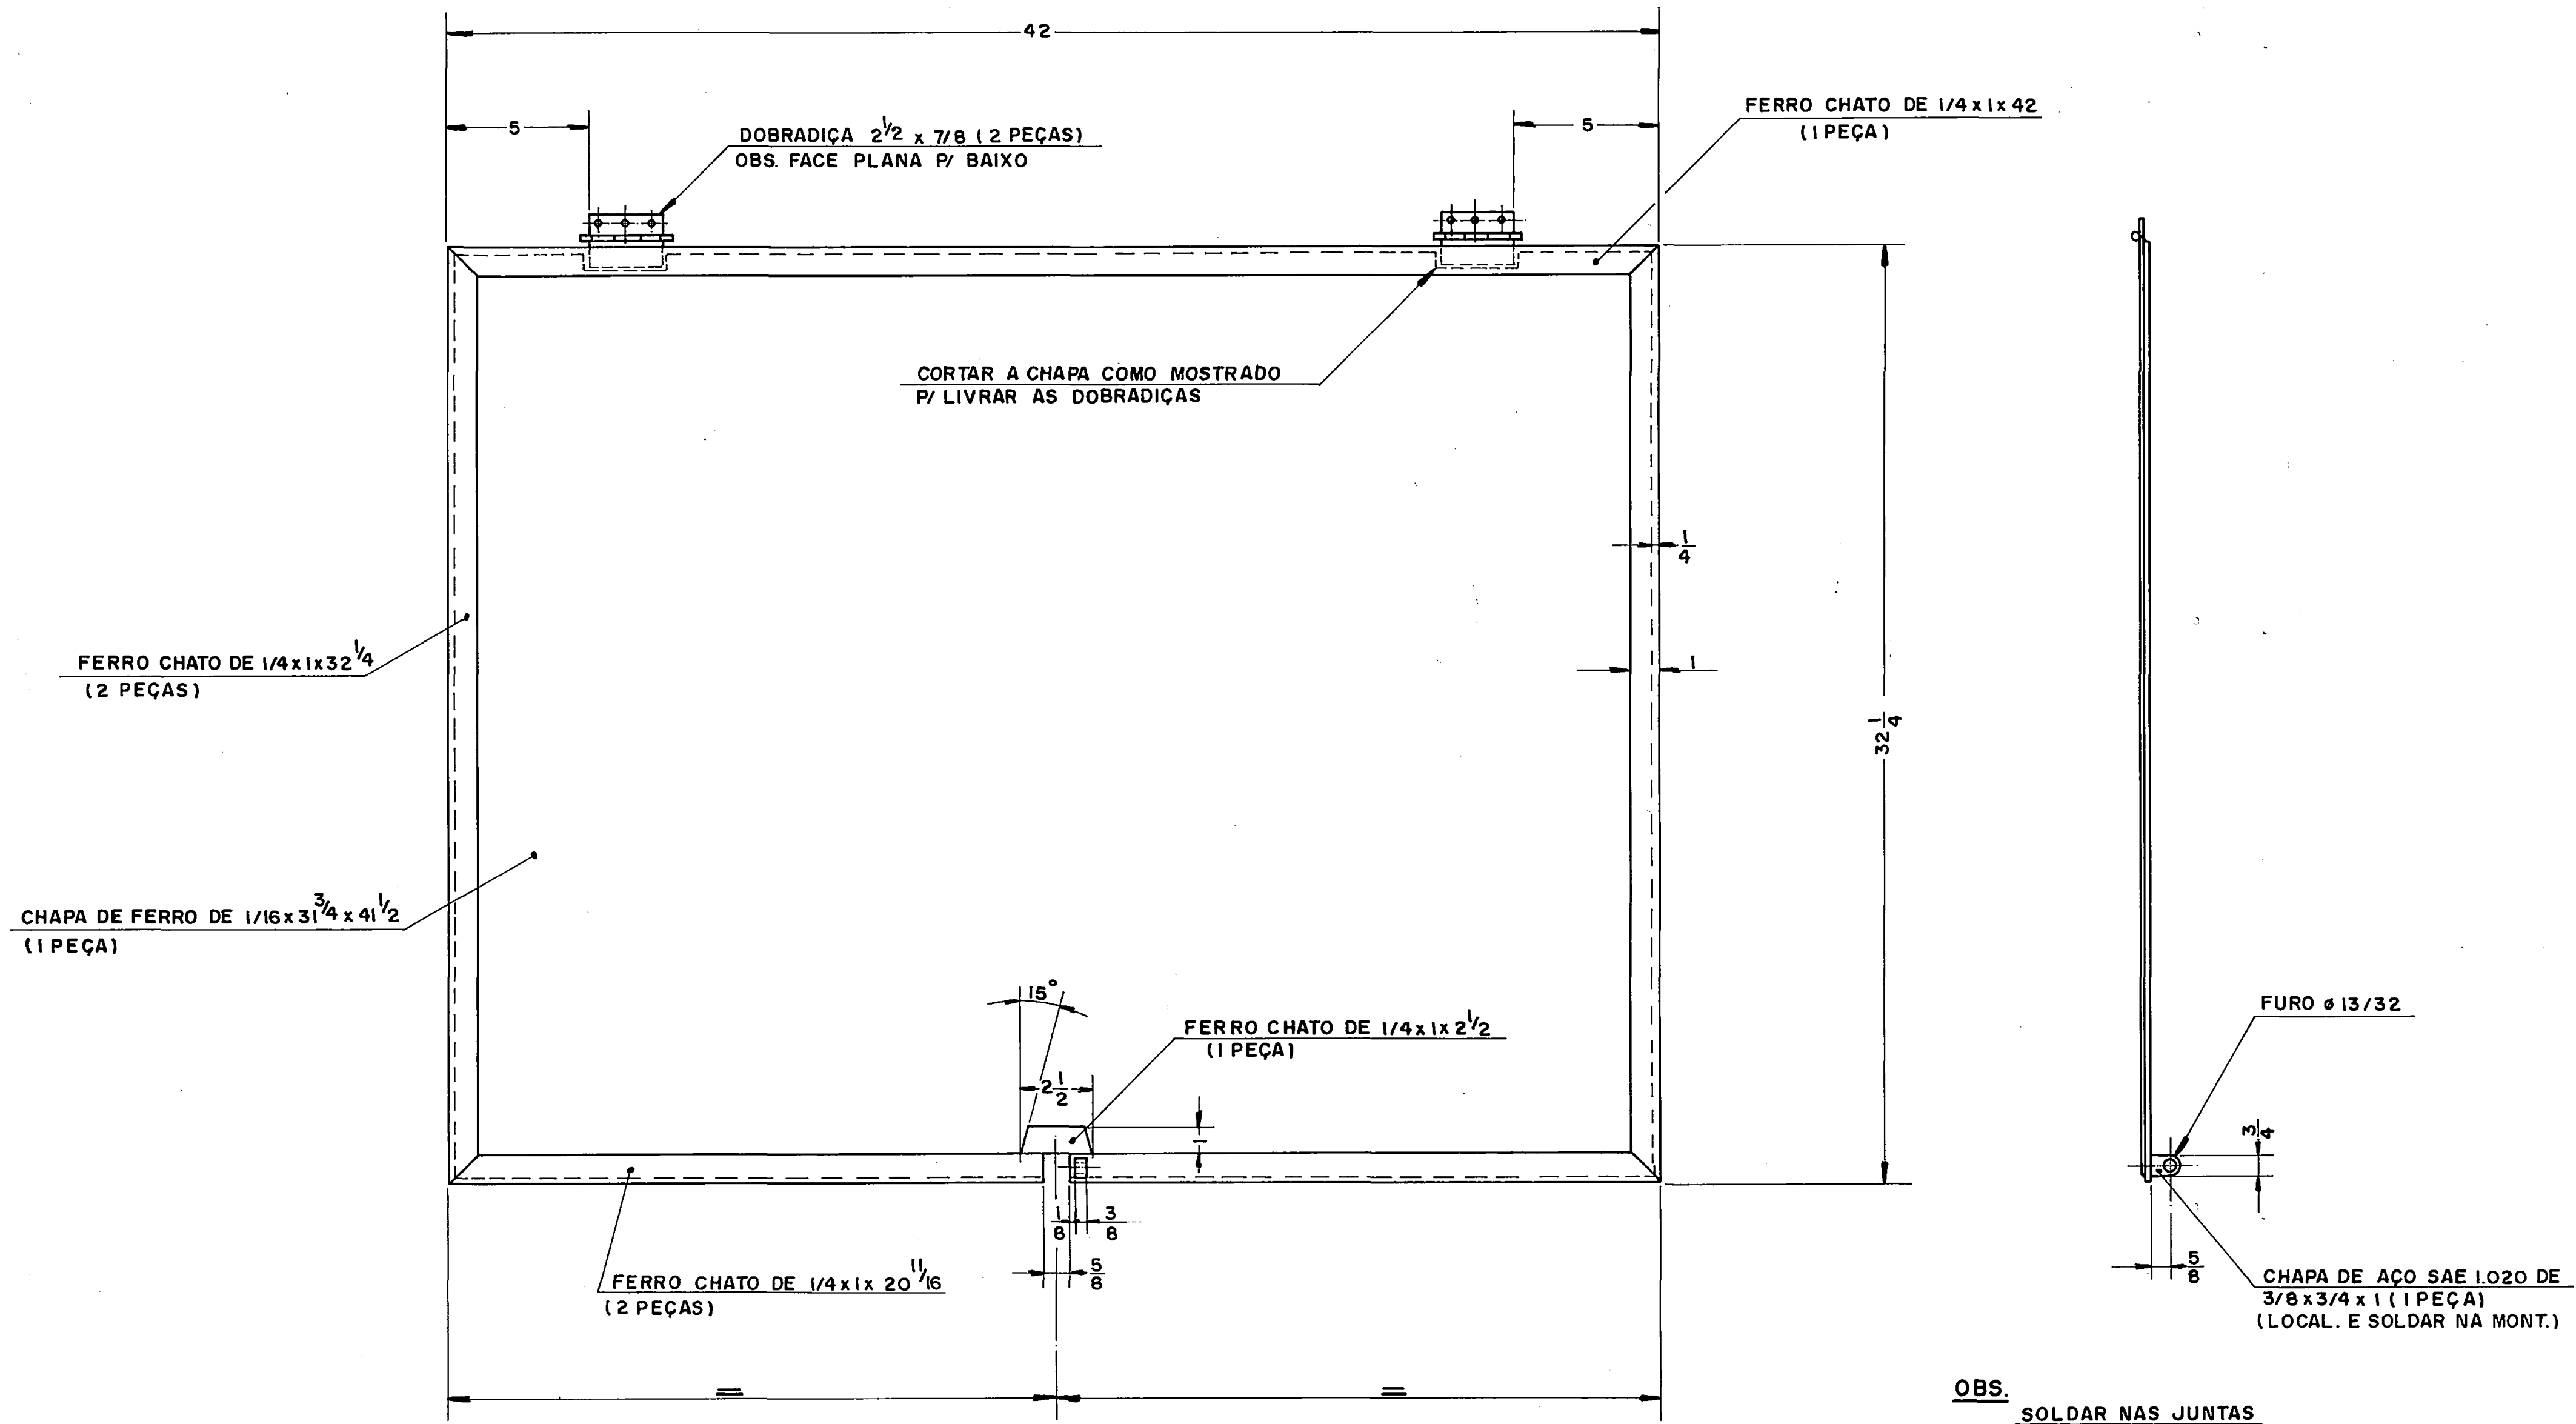

DATA: 14-10-93	VER.	CES.
TOLERANCIAS STANDARD PARA SUPERFÍCIES USINADAS SIM	APROV.	
TOLERANCIA INDICADA: DECIMAL + 0,005	NOME DO CONJ.	N.º DO CONJ.
TRAPAÇO	NOME DA PEÇA	N.º DA PEÇA
DE 0" ATE 5" ± 1/64	TRAT. TERM.	N.º DO BOM.
DE 5" ATE 24" ± 1/32		
ACIMA DE 24" ± 1/16	ESCALA 1/4"	