

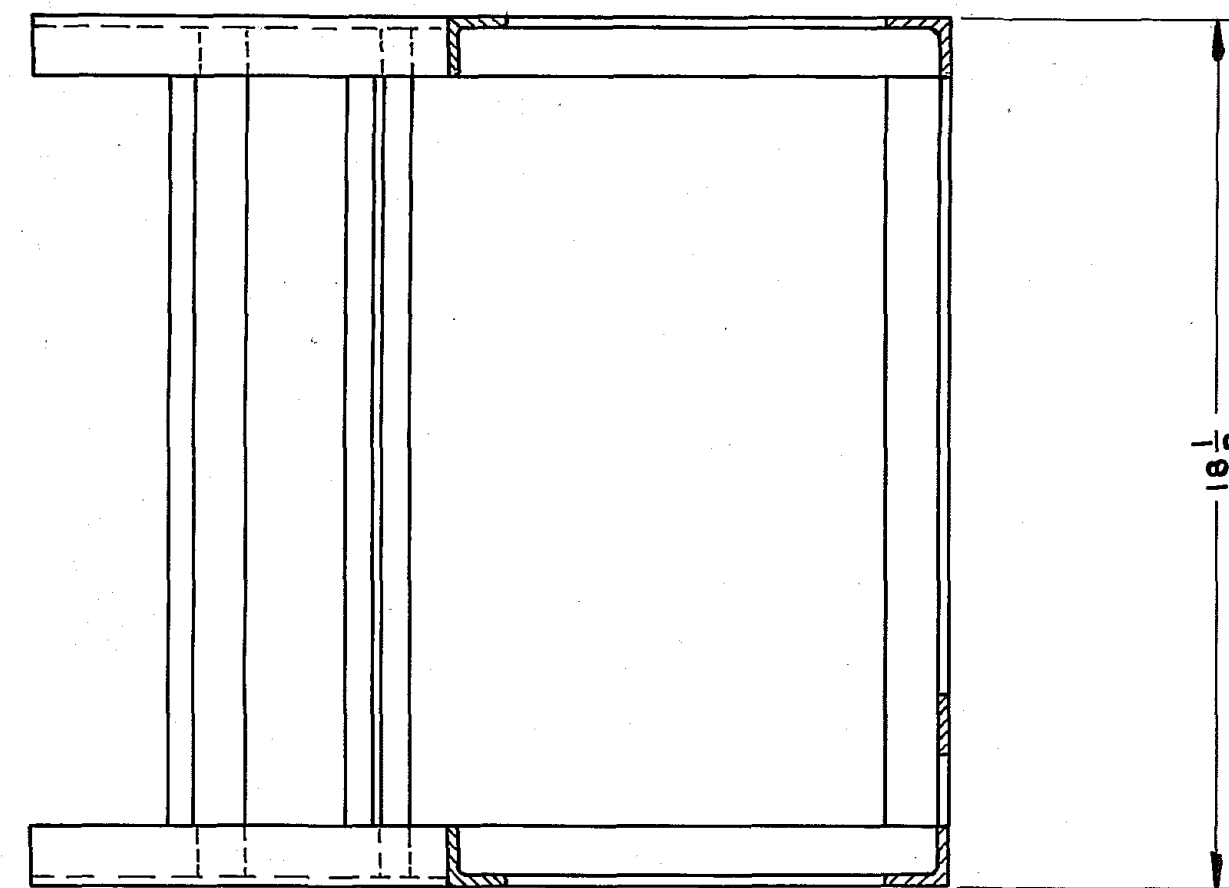


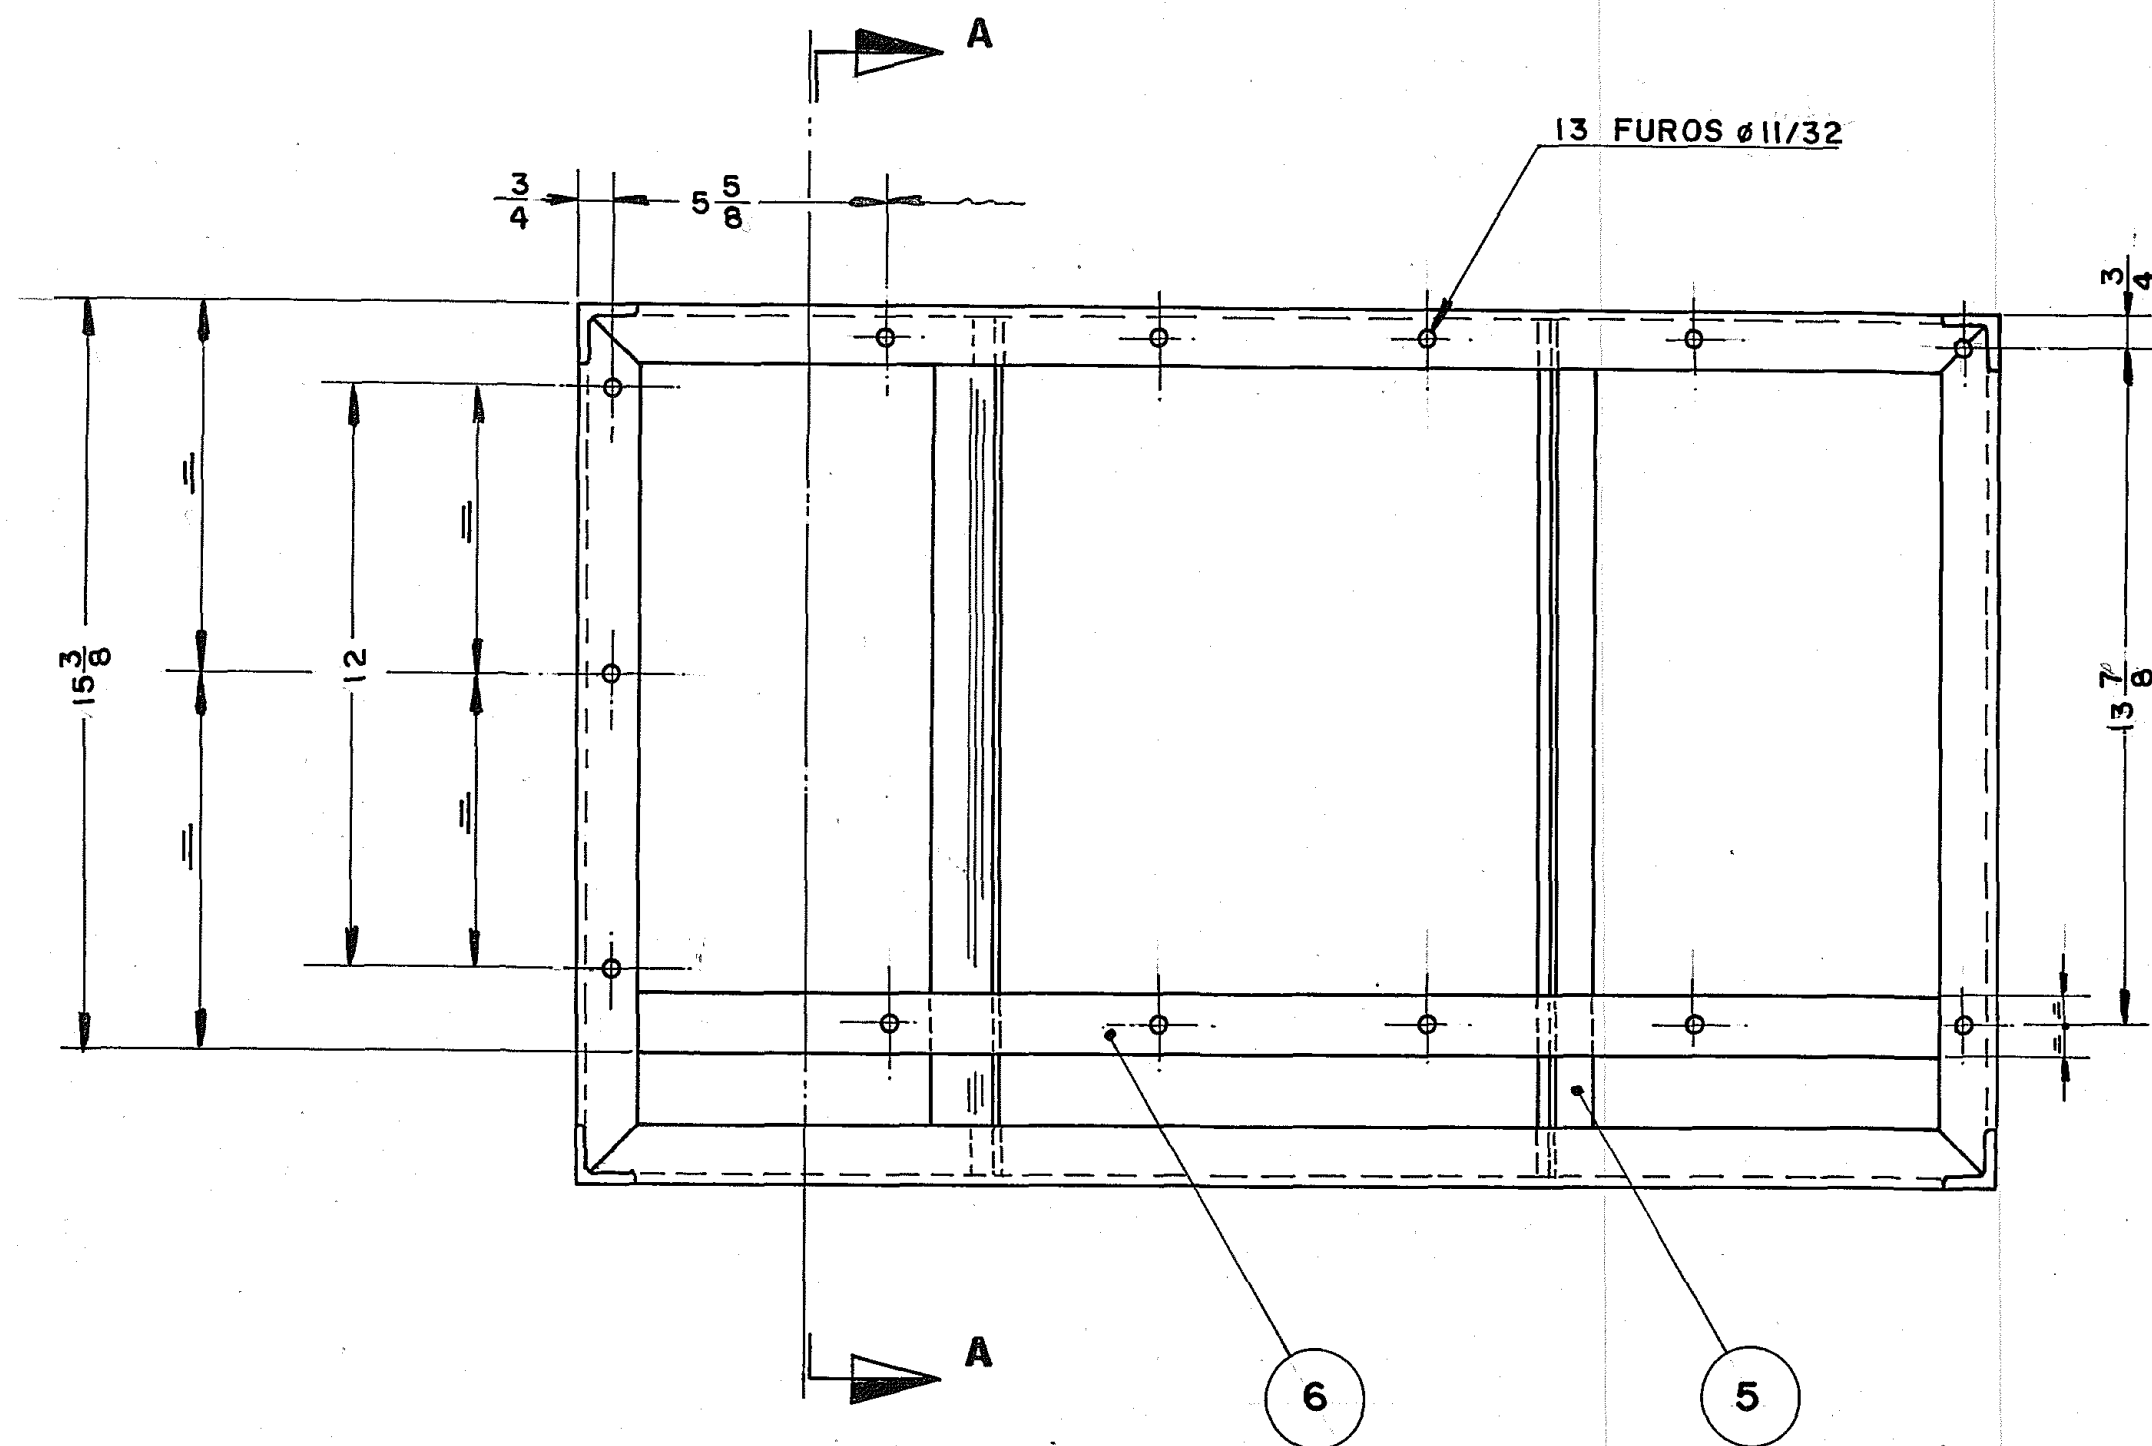

CORTE-AA

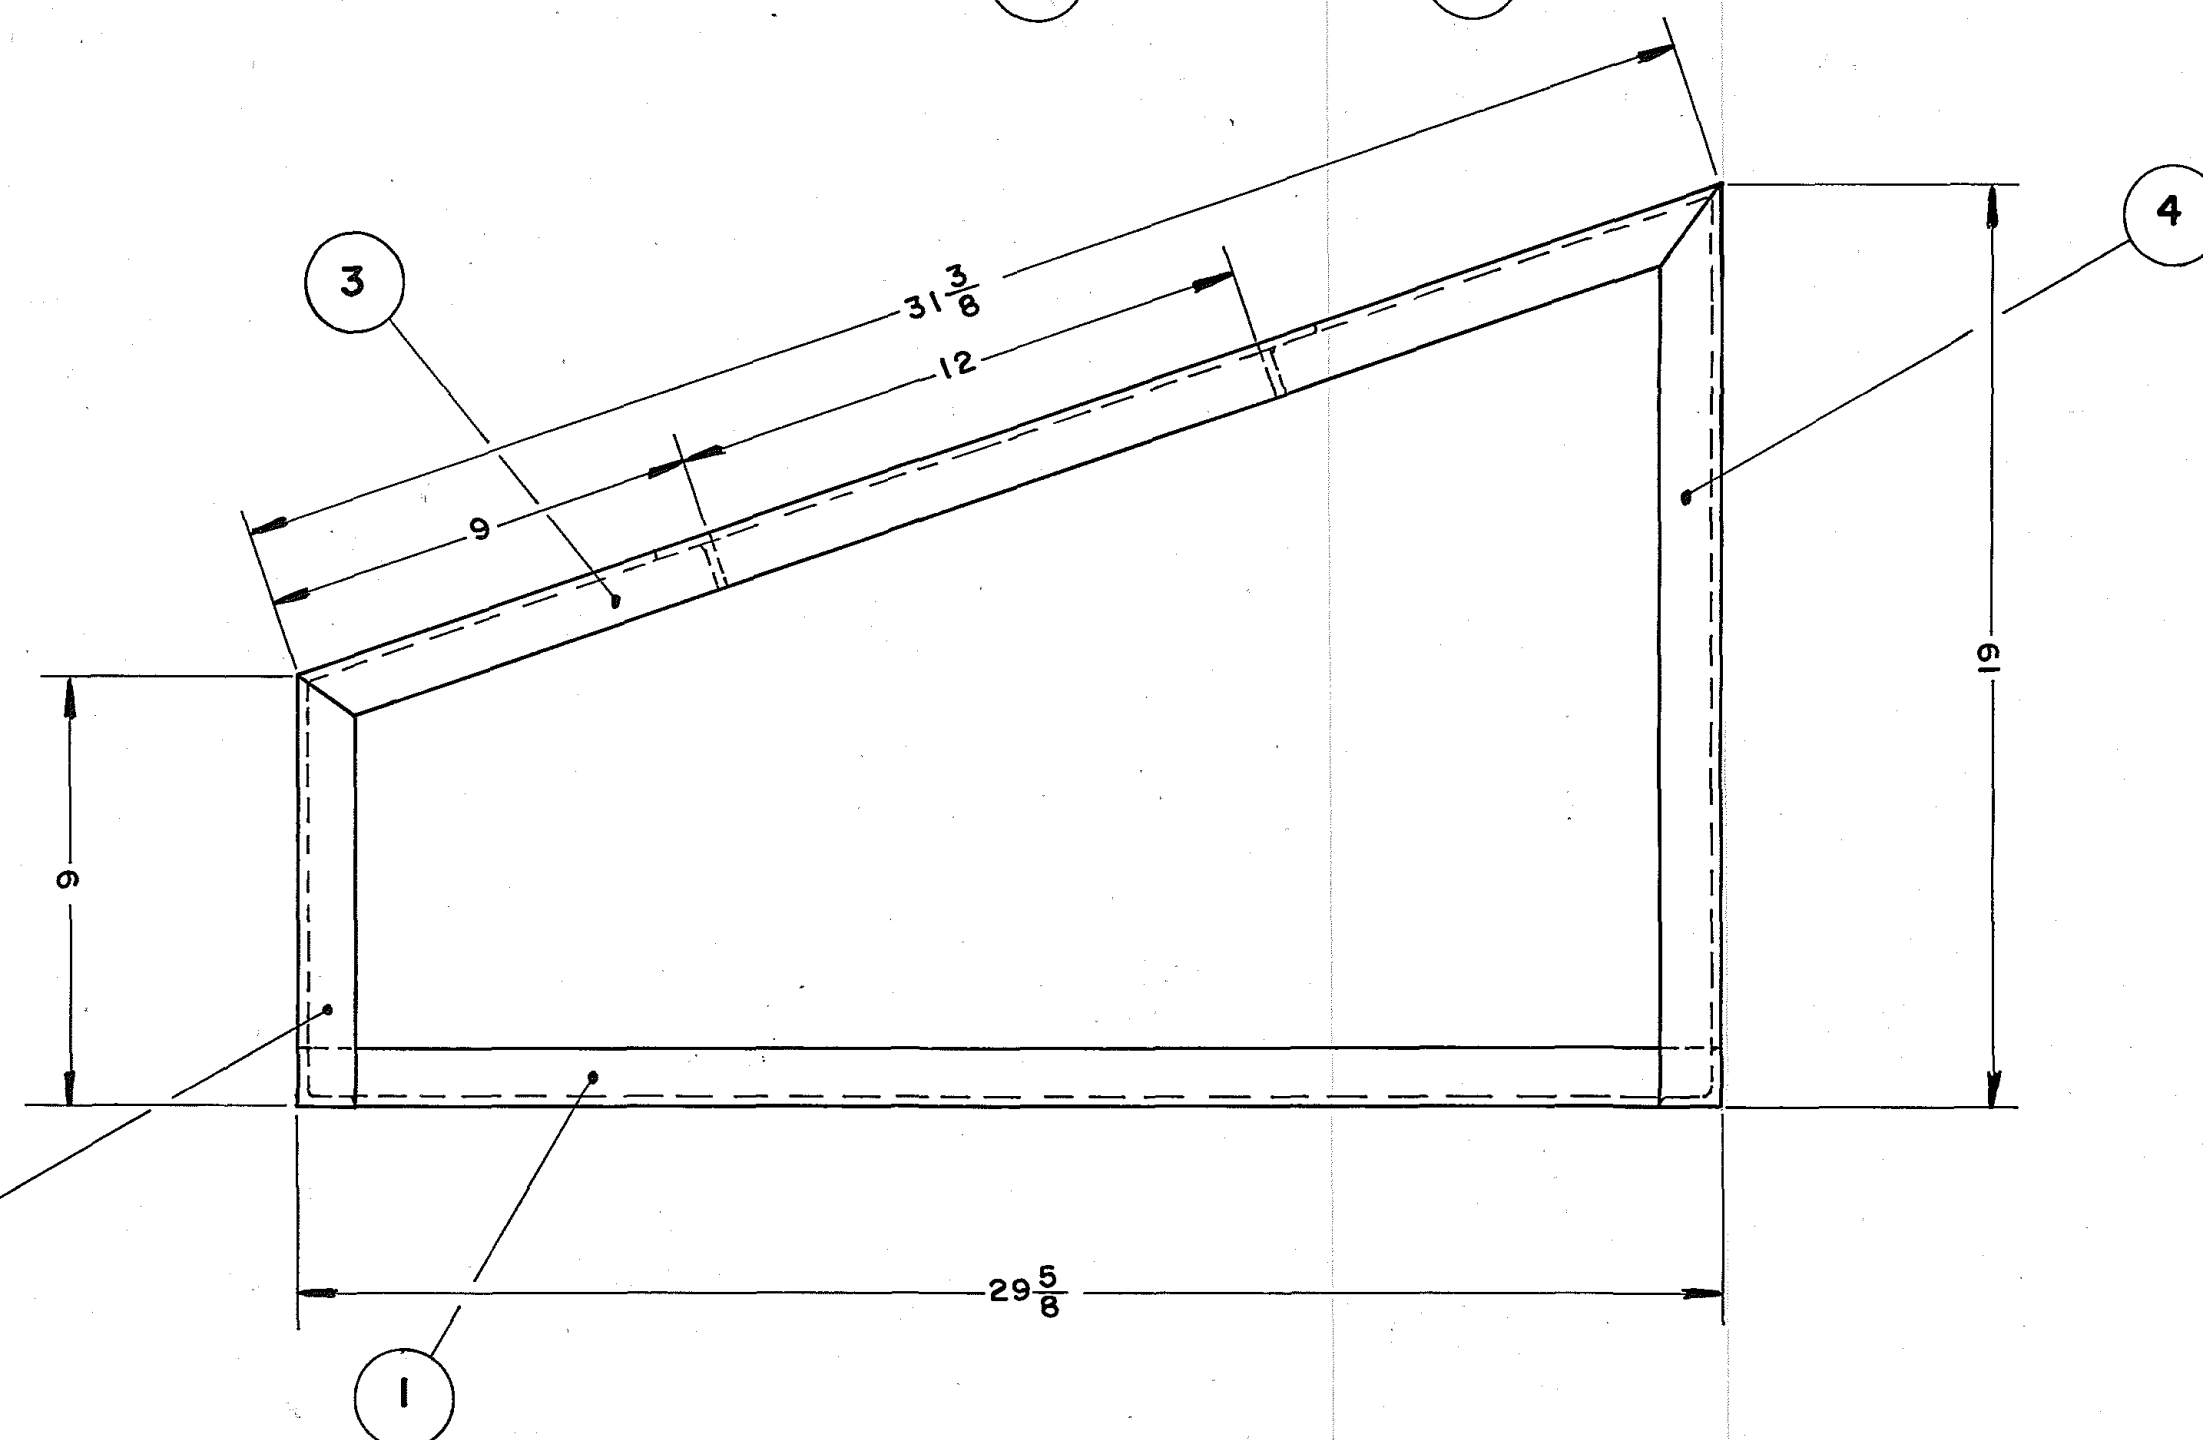

QTD	POS	DESCRIÇÃO
2	7	CANTON. DE $1/4 \times 1/4 \times 1/4 \times 18\frac{1}{8}$
1	6	FERRO CHATO DE $1/4 \times 1/4 \times 27\frac{1}{8}$
2	5	CANTON. DE $1/4 \times 1/4 \times 1/4 \times 17\frac{5}{8}$
2	4	CANTON. DE $1/4 \times 1/4 \times 1/4 \times 19$
2	3	CANTON. DE $1/4 \times 1/4 \times 1/4 \times 31\frac{3}{8}$
2	2	CANTON. DE $1/4 \times 1/4 \times 1/4 \times 9$
2	1	CANTON. DE $1/4 \times 1/4 \times 1/4 \times 29\frac{5}{8}$

OBS.
SOLDAR NAS JUNTAS

DATA	13-10-93	VIDROS VITON LTDA.	ES. <i>[Signature]</i>
REVISÃO	1	MAT. VIDE TABELA	VER.
REVISÃO	1	NOME DO CONJ. ESTRUTURA DO PAINEL	APROV.
REVISÃO	1	NOME DA PEÇA ESTRUTURA SUPERIOR	N.º DO CONJ. VVM-577
REVISÃO	1	TRAT. TERM.	N.º DA PEÇA VVM-577-31
REVISÃO	1	ESCALA 1/4	N.º DO PIS.