


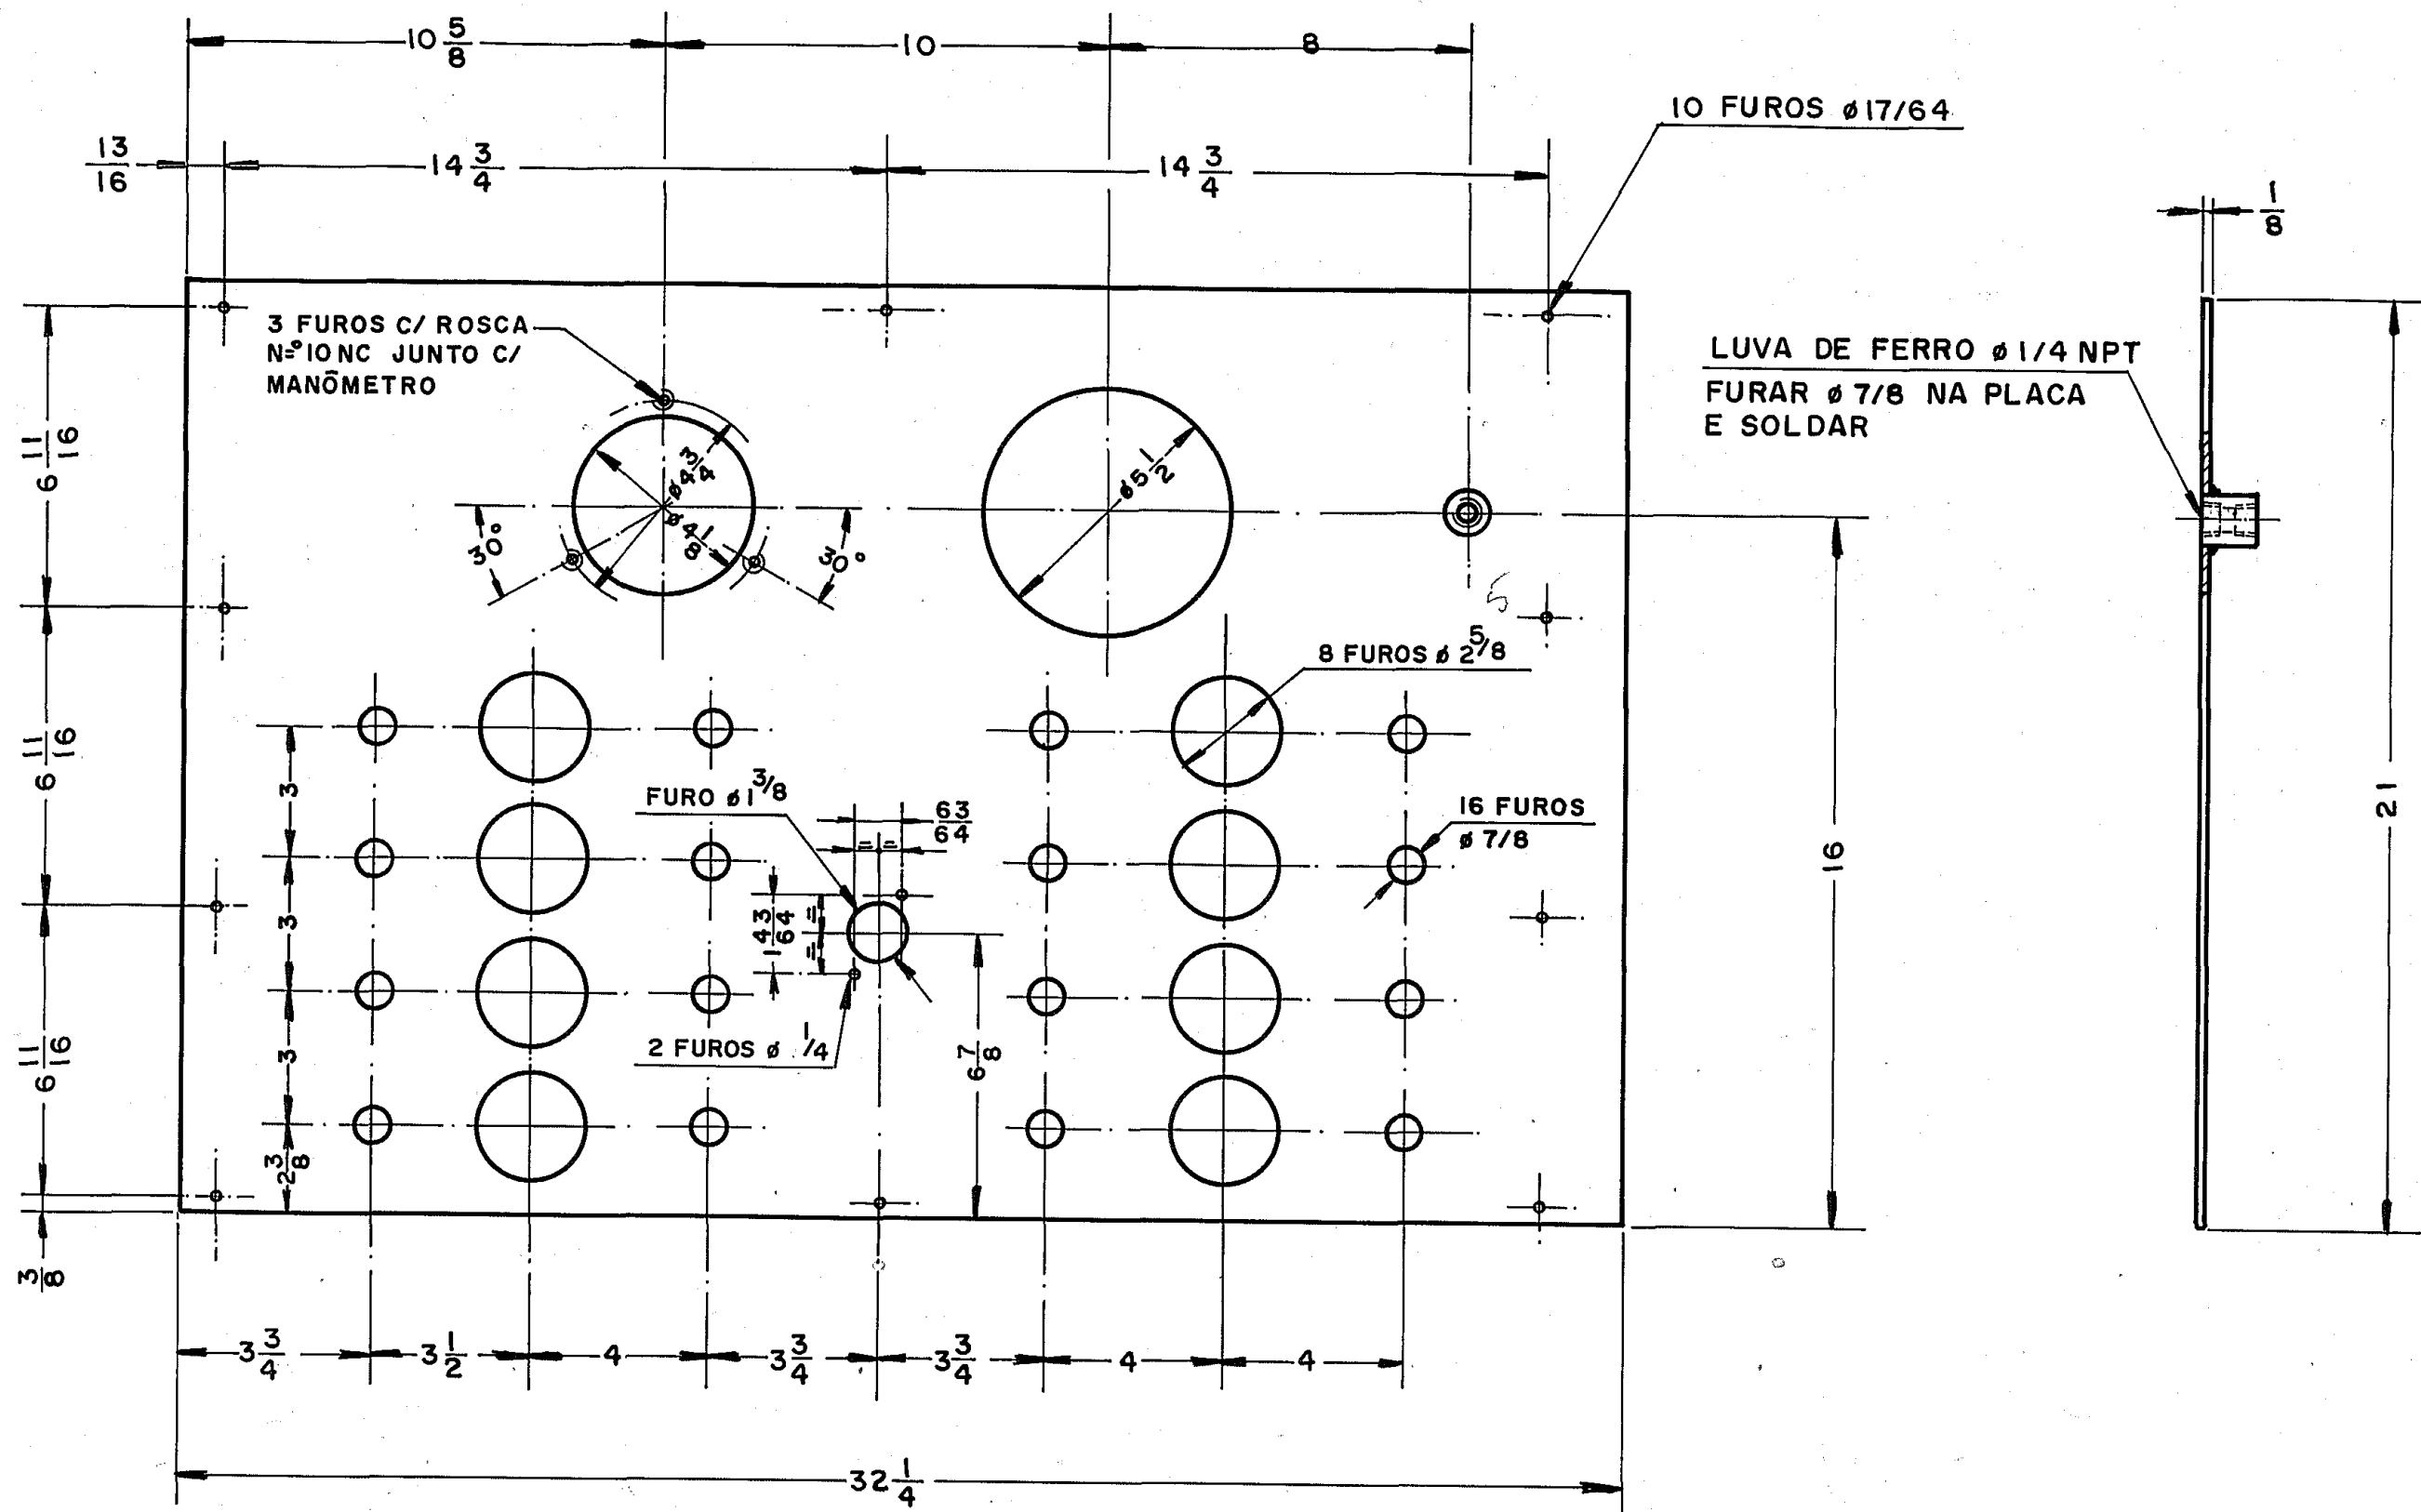

DATA	11-10-93	VIDROS VITON LTDA.	ES. <i>M. P. S.</i>
R. VISÃO	T.C.M.	TOLERÂNCIAS STANDARD PARA SUPERFÍCIES USADAS SEM TOLERÂNCIA INDICADA	VER.
DETA	1/4	DE 0" ATÉ 5" $\pm 1/64$	APROV.
DETA	1/4	DE 5" ATÉ 24" $\pm 1/32$	N.º DO CONJ. VVM-577
DETA	1/4	ACIMA DE 24" $\pm 1/16$	N.º DA PEÇA VVM-577-9
DETA	1/4	ACIMA DE 24" $\pm 1/16$	N.º DO D.S.
DETA	1/4	ACIMA DE 24" $\pm 1/16$	ESCALA 1/4
DETA	1/4	ACIMA DE 24" $\pm 1/16$	TRAT. TERM.
DETA	1/4	ACIMA DE 24" $\pm 1/16$	TRAT. TERM.