


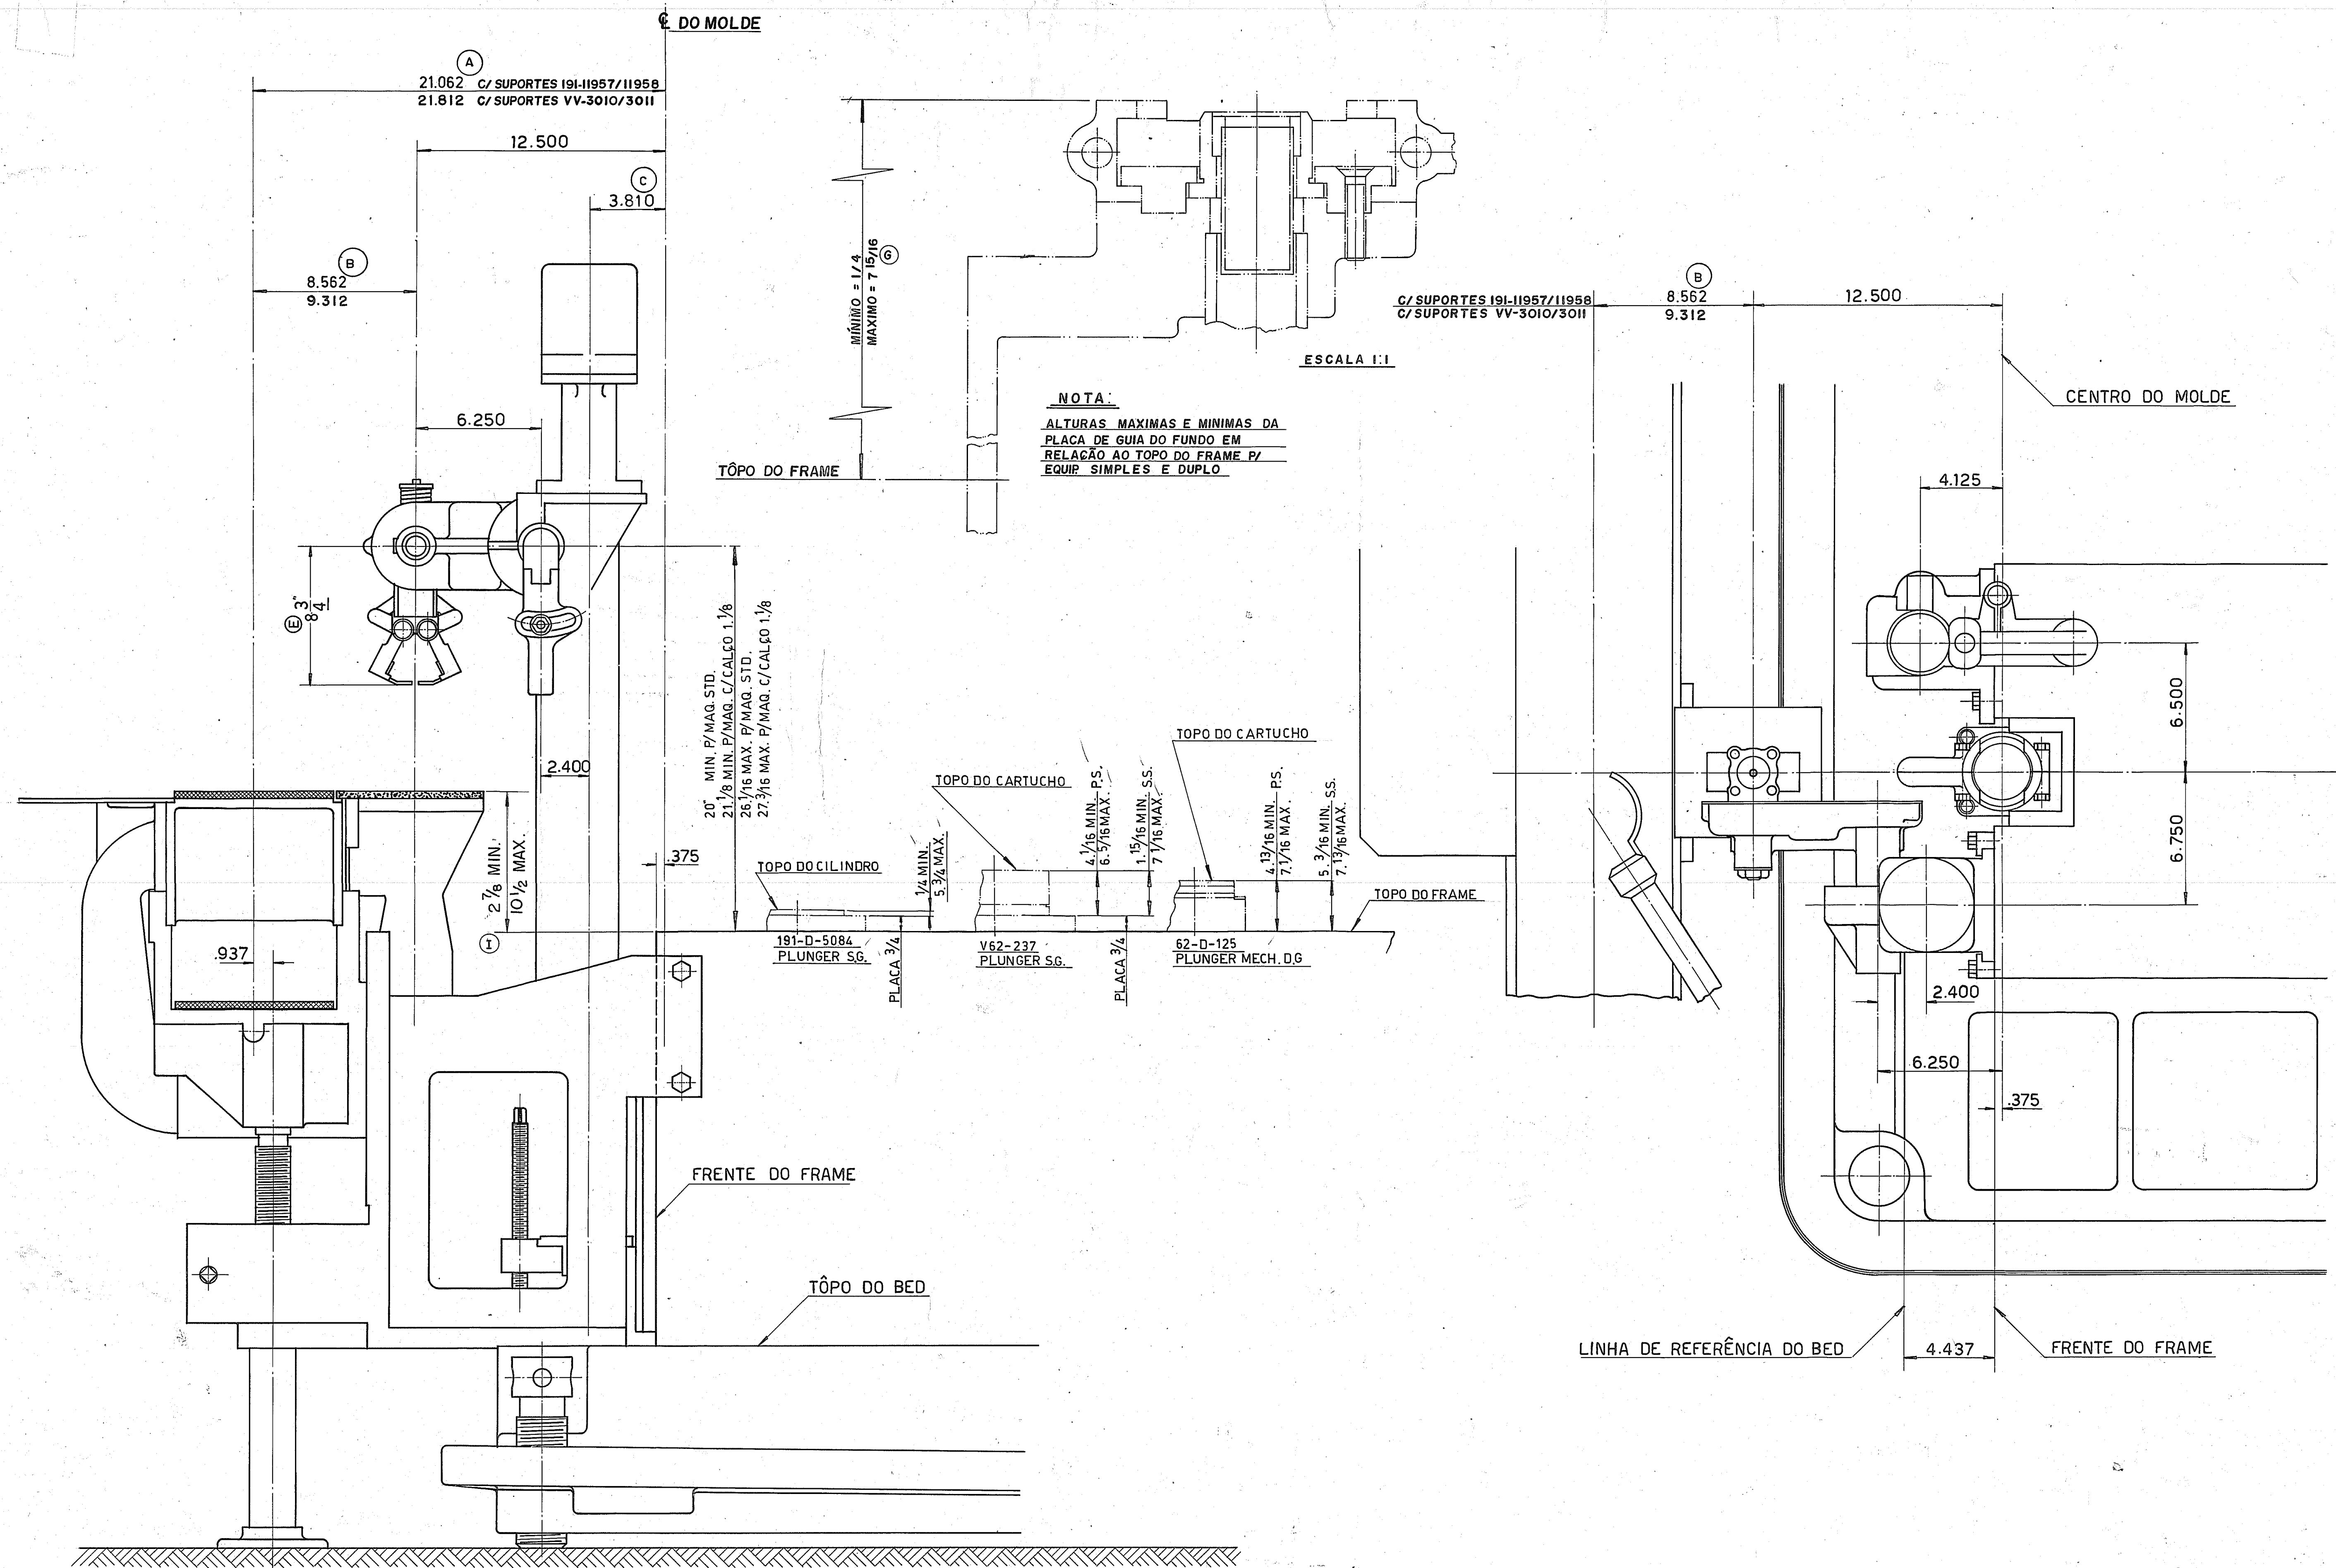

I	ERA A PARTIR DO PISO	22-09-94	D	ERA 19 1/2	01-08-86	Sec.	VIDROS VITON LTDA.	Data 19-7-61
H	ERA: 20" MÍNIMO e 27 5/8 MÁXIMO	01-04-91	C	ERA 3.850	12-07-83	Pag.		Des. JOSÉ
G	ERA: 8 1/2	01-04-91	B	ERA 8.000	12-07-83	Mat		Ver.
F	ERA: 19 1/4, 26 7/8	24-01-91	A	ERA 20.500	12-07-83	Conjunto	MÁQUINA I.S.	Subst.
E	ERA 6 3/4	5.9.89				Nome da	MEDIDAS DE REFERÊNCIA	Nº da
ITEM	MODIFICAÇÃO S	DATA	ITEM	MODIFICAÇÕES	DATA	Peça	LOCALIZAÇÃO DE PEÇAS E CONJ.	Ver.
						Tratam.		Nº do
						Técnico		Desenho