
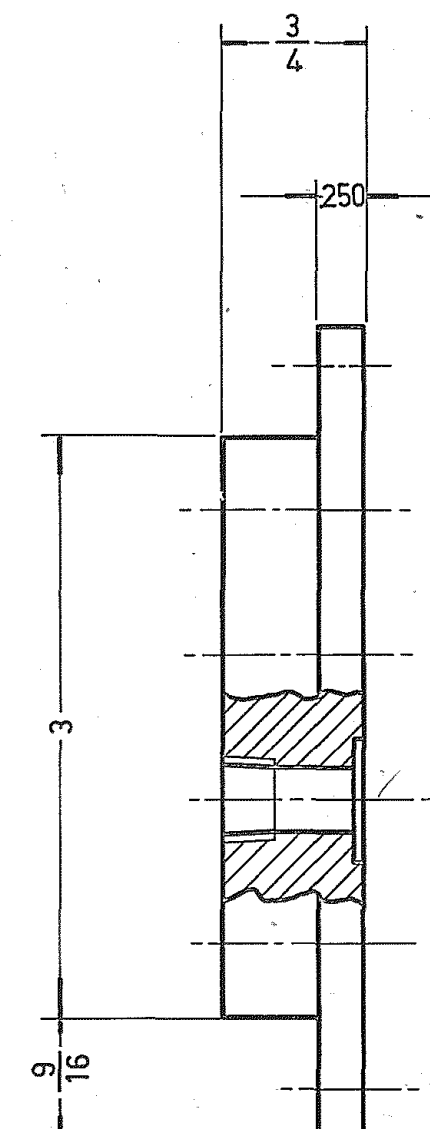


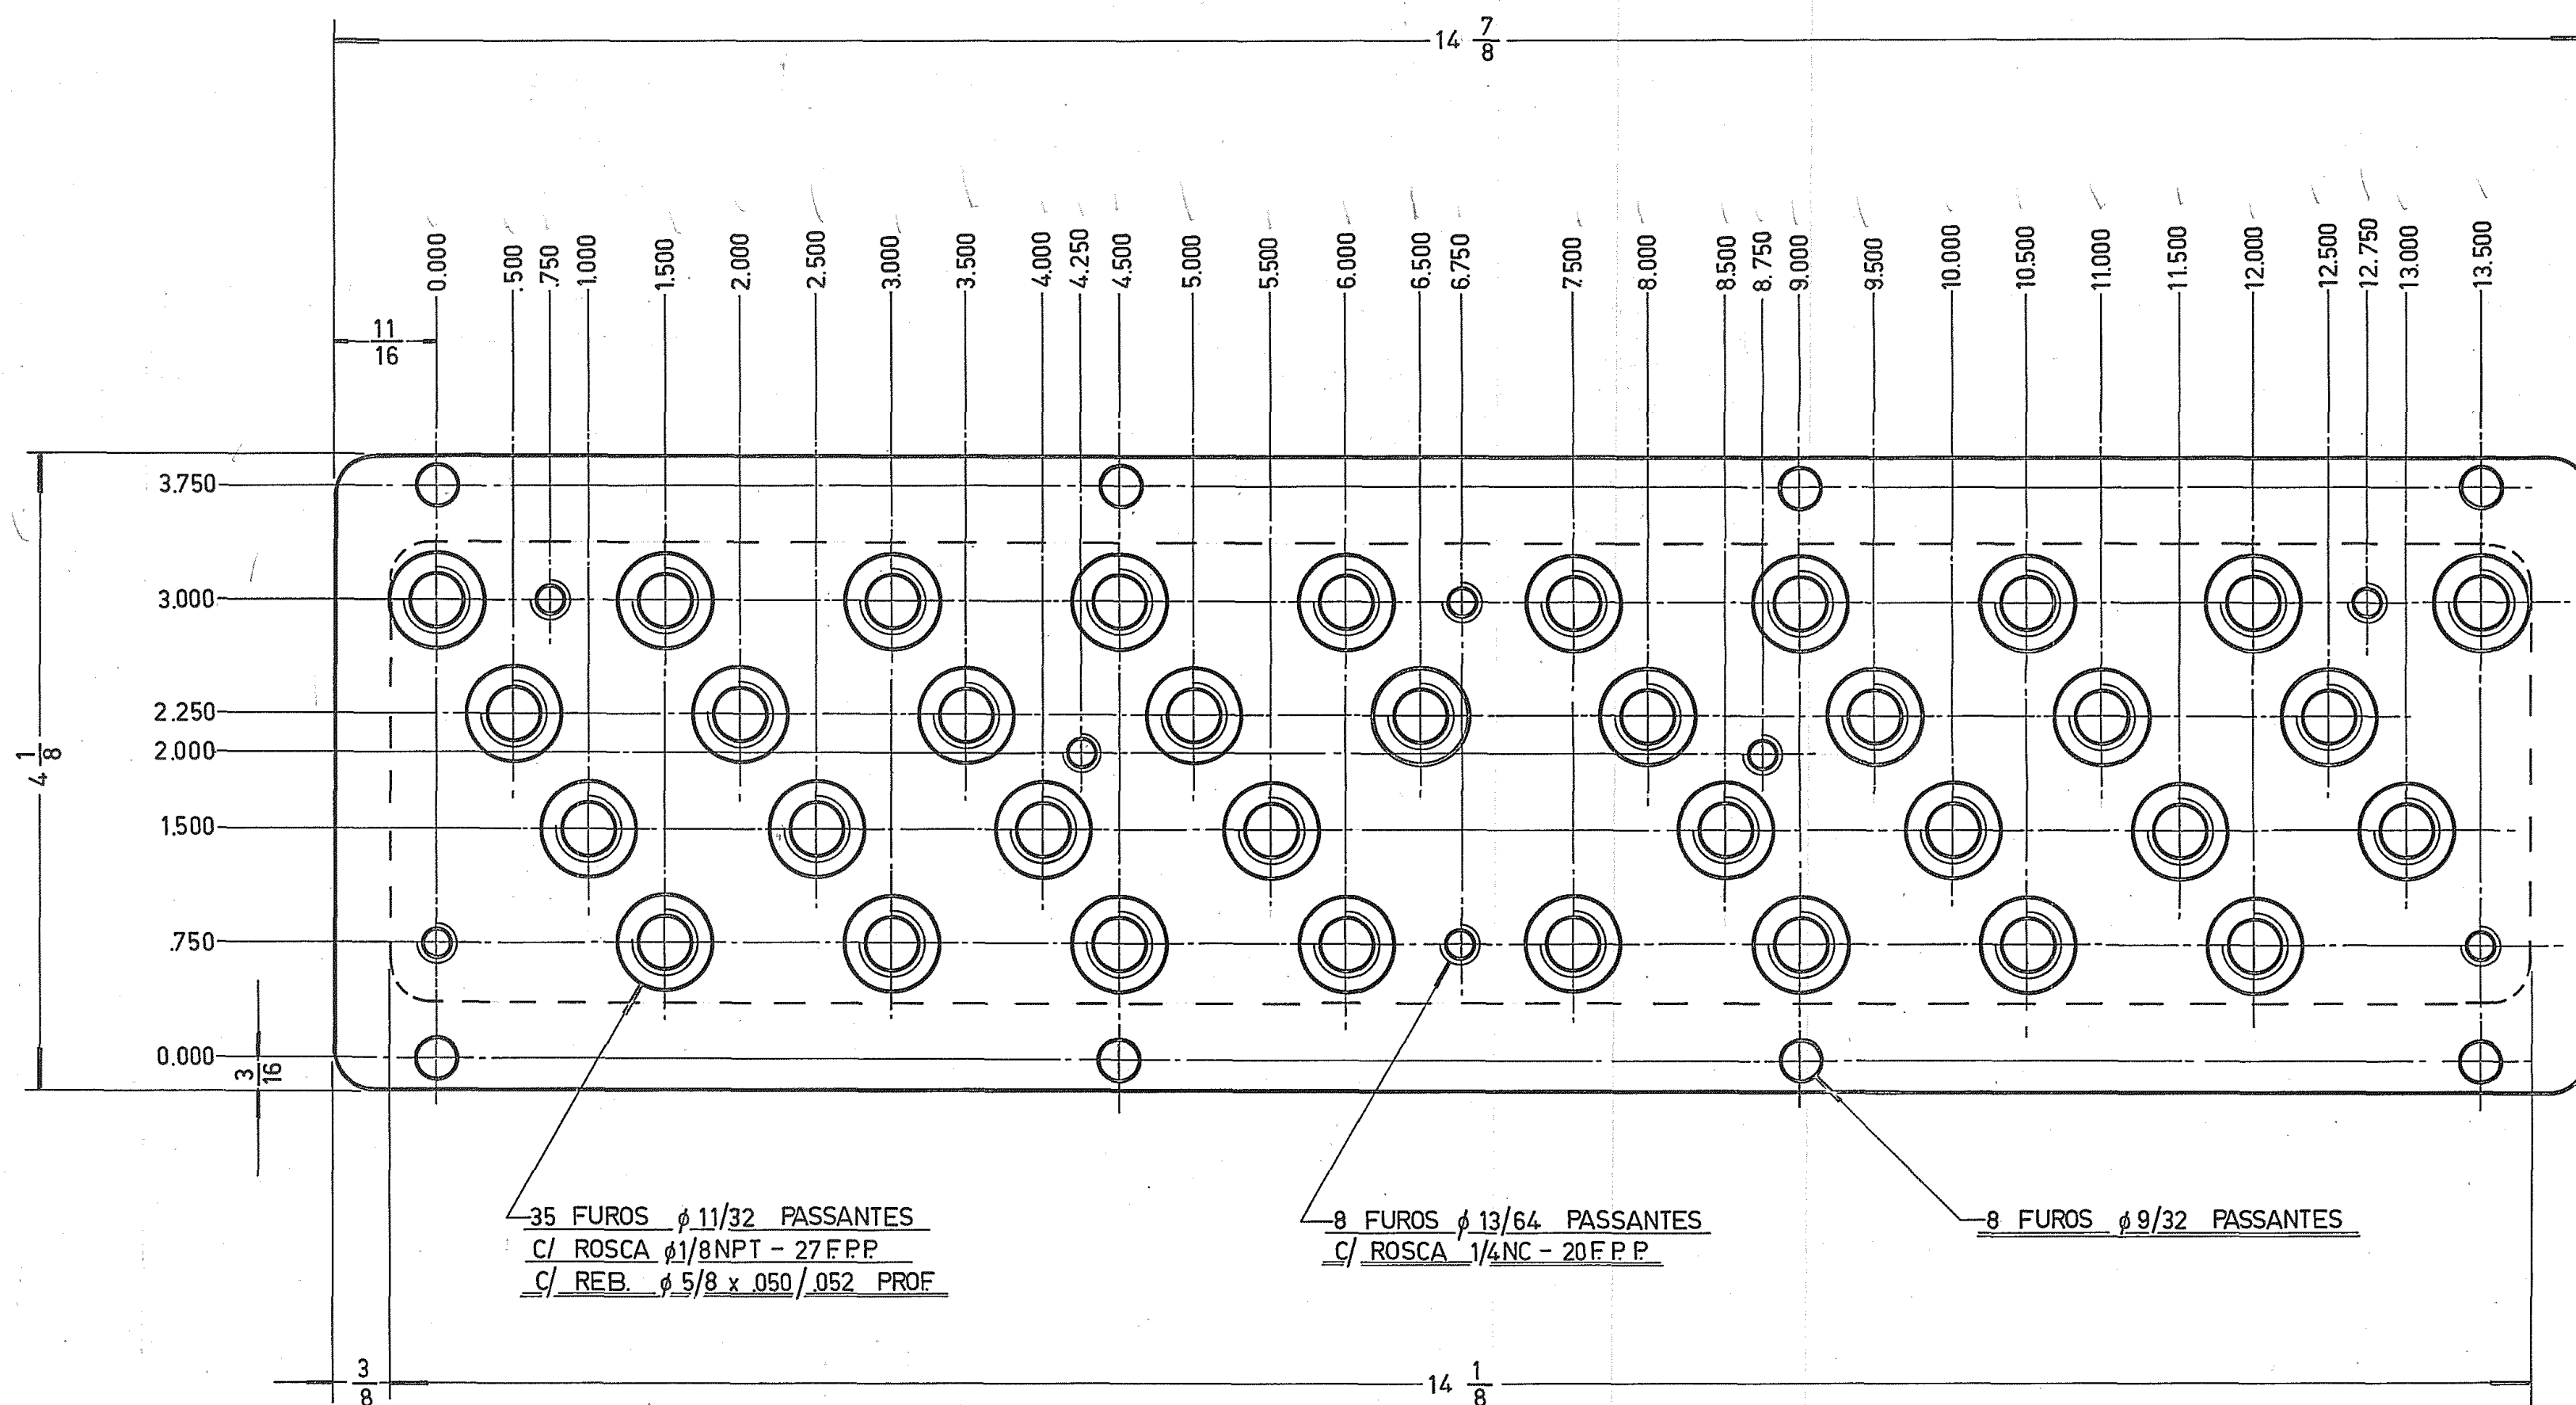

35 FUROS ϕ 11/32 PASSANTES
C/ ROSCA ϕ 1/8 NPT - 27 F.P.P.
C/ REB. ϕ 5/8 x .050/.052 PROF

8 FUROS ϕ 13/64 PASSANTES
C/ ROSCA 1/4 NC - 20 F.P.P.

8 FUROS ϕ 9/32 PASSANTES

R. 1/4

DATA: 26-11-86	DES. <i>Vieira</i>
TOLERANCIAS STANDARD PARA SUPERFICIES USINADAS SEM TOLERANCIA INDICADA	VER. <i>1/1000</i>
DECIMAL $\pm$ 0.05"	APROV. <i>1/1000</i>
FRAÇÃO	N.º DO PROJ. 191-7025
DE 0" ATÉ 5" $\pm$ 1/32	N.º DA PEÇA 191-21982
DE 5" ATÉ 24" $\pm$ 1/32	N.º DO DES.
ACIMA DE 24" $\pm$ 1/16	
TRAT. TERM.	ESCALA 1:1
VIDROS VITON LTDA.	
MAT. AÇO SAE 1020	
NOME LINCOL LUBE TO SECT	
DO CONJ. FRAME "E" MODULE SYSTEM	
NOME DA PEÇA MANIFOLD	