


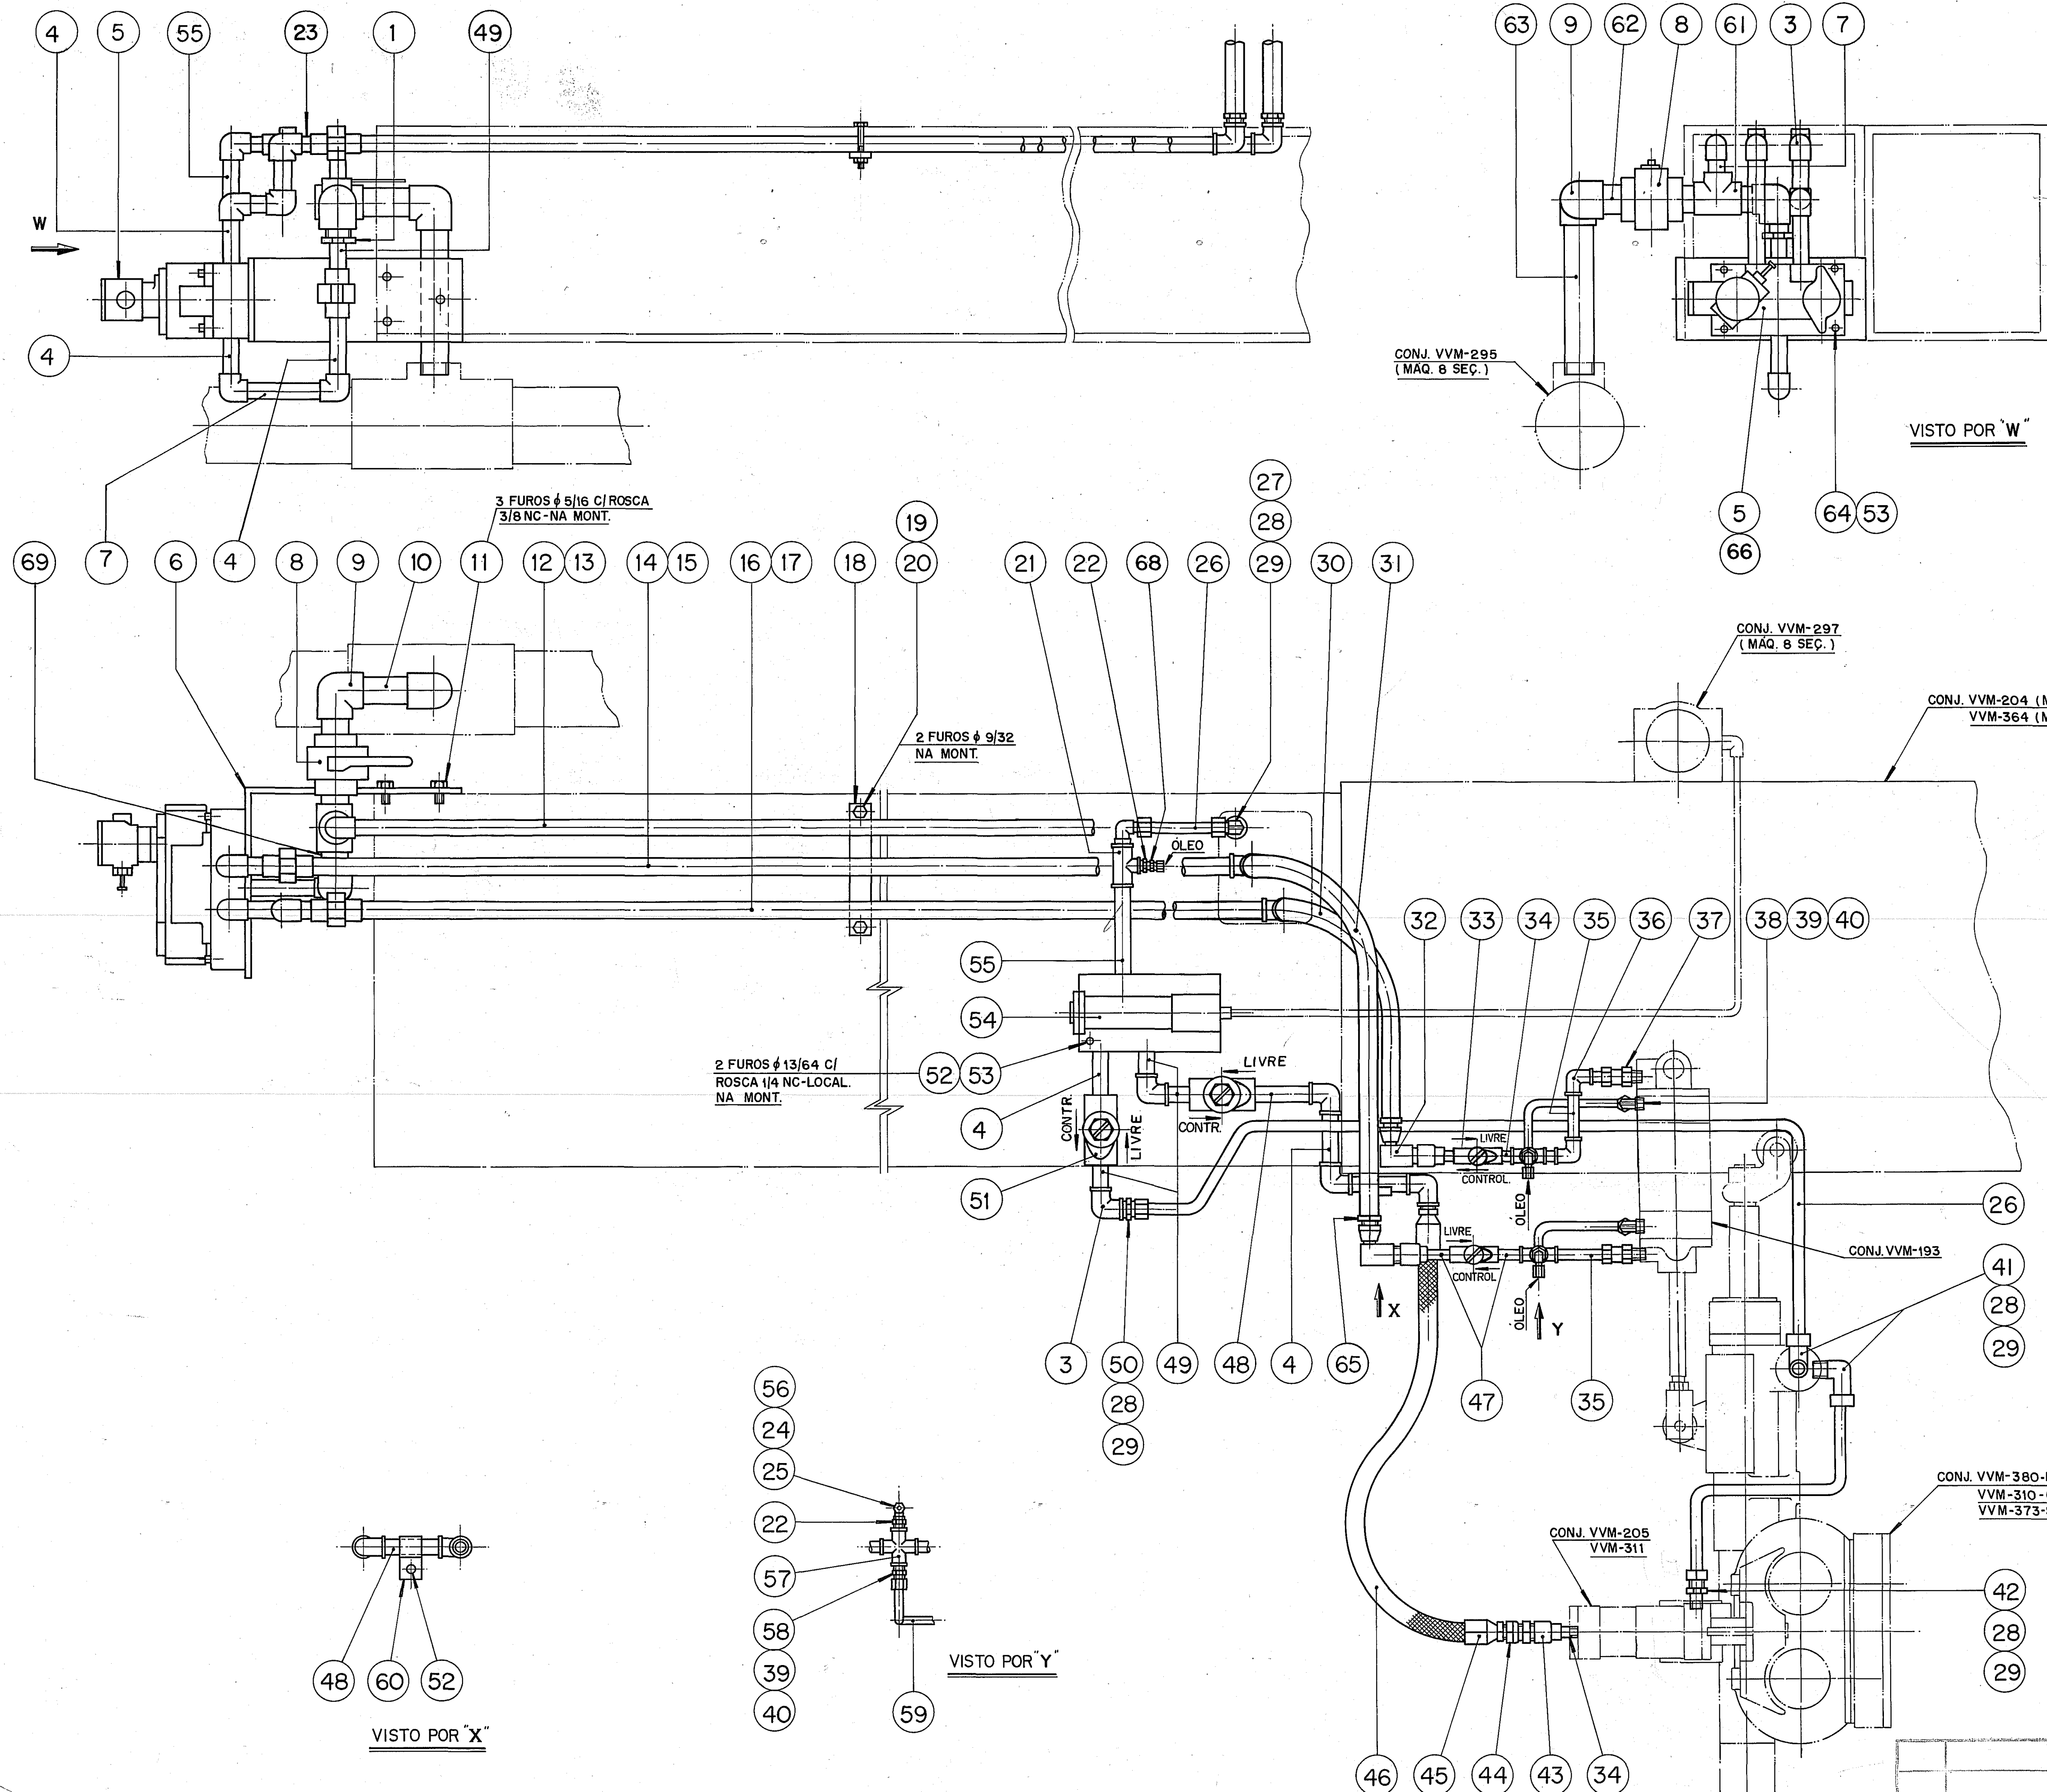

1	1	70	CAIXA DE LIGAÇÃO	VVM-669	—	SUB-CONJ. N. MOSTR.
1	1	69	NIPLE	COMERCIAL (161-F-1)	F. GALV.	1 NPTx1 1/2
1	1	68	UNIÃO NPT EXT. C/CHECK VALVE	COMERCIAL VCL-90	LATÃO	1/8 NPTx1/8 T.
1	1	67	NIPLE	COMERCIAL (161-D-11)	F. GALV.	1/2 NPTx 6"
1	1	66	VÁLVULA SOLENÓIDE	COMERCIAL (208-A-5)	—	SCHRAEDER 5295-8202-NA
4	4	65	CONEXÃO REUSÁVEL	COMERCIAL (121-1-17)	—	AERQUIP Nº 4738-8-10-B
4	4	64	PARAF. ALLEN C/CAB.	COMERCIAL (163-D-12)	—	AÇO 1/4 NCx 2"
1	1	63	NIPLE	COMERCIAL (161-F-3)	F. GALV.	1 NPTx 1 1/2
2	2	62	NIPLE	COMERCIAL (193-B-9)	F. GALV.	1 NPTx 2"
1	1	61	TEE DE REDUÇÃO	COMERCIAL (161-F-3)	F. GALV.	1 NPTx 1/2 NPT
1	1	60	SUPORTE DO CANO	VV 2719	AÇO	—
59	59	59	TUBO	COMERCIAL BUNDY TUBING	—	4 3/8 COMP. CONF. NECES.
2	2	58	UNIÃO DE COMPRES.	COMERCIAL (VCL-97)	LATÃO	1/4 NPTx 3/8 T.
2	2	57	CRUZETA	COMERCIAL (VCL-17)	F. GALV.	1/4 NPT
2	2	56	COTOVELO DE COMPRES.	COMERCIAL (VCL-17)	LATÃO	1/8 NPTx 1/8 T.
2	2	55	NIPLE	COMERCIAL (161-D-2)	F. GALV.	1/2 NPTx 1 1/2
1	1	54	VÁLVULA ISO 3	COMERCIAL (208-A-7)	—	SCHRAEDER 5295-430-00
6	6	53	ARRUELA DE PRESSÃO	COMERCIAL (163-D-8)	AÇO	1/4
3	3	52	PARAF. ALLEN C/CAB.	COMERCIAL (206-A-7)	—	AÇO 1/4 NC x 1"
2	2	51	VÁLV. DE CONTR. FLUXO	COMERCIAL (VCL-119)	—	SCHRAEDER 3250-C-1/2 NPT
1	1	50	UNIÃO DE COMPRES.	COMERCIAL (VCL-119)	LATÃO	1/2 NPTx 1/2 T.
3	3	49	NIPLE	COMERCIAL (161-D-5)	F. GALV.	1/2 NPTx 1 1/2
2	2	48	NIPLE	COMERCIAL (161-D-5)	F. GALV.	1/2 NPTx 3"
2	2	47	NIPLE	COMERCIAL (161-D-2)	F. GALV.	1/4 NPTx 1 1/2
1	1	46	MANGUEIRA FLEXÍVEL	COMERCIAL (121-1-8)	—	AERQUIP Nº 1503-10
2	2	45	CONEXÃO REUS. PADRÃO	COMERCIAL (101-H-7)	AÇO	AERQUIP Nº 4412-8-10 S
1	1	44	PORCA GIRATÓRIA	COMERCIAL (152-C-4)	AÇO	AERQUIP Nº 2045-8-8 S
2	2	43	LUVA DE REDUÇÃO	COMERCIAL (VCL-37)	F. GALV.	1/2 NPTx 1/4 NPT
1	1	42	UNIÃO DE COMPRES.	COMERCIAL (VCL-37)	LATÃO	1/4 NPTx 1/2 T.
2	2	41	COTOVELO DE COMPRES.	COMERCIAL (VCL-37)	LATÃO	3/8 NPTx 1/2 T.
4	4	40	PORCA DE COMPRES.	COMERCIAL (VCL-56)	LATÃO	3/8 T.
4	4	39	ANEL	COMERCIAL (VCL-05)	LATÃO	1/4
2	2	38	COTOVELO DE COMPRES.	COMERCIAL (VCL-05)	LATÃO	1/8 NPTx 3/8 T.
2	2	37	VÁLVULA DE RETENÇÃO	COMERCIAL (127-B-1)	—	SCHRAEDER 5050-110-1 1/4 PT
2	2	36	COTOVELO 90°	COMERCIAL (161-B-5)	F. GALV.	1/4 NPT
2	2	35	NIPLE	COMERCIAL (161-B-5)	F. GALV.	1/4 NPTx 1 1/2
4	4	34	NIPLE	COMERCIAL (161-B-1)	F. GALV.	1/4 NPTx 1"
2	2	33	VÁLV. DE CONTR. FLUXO	COMERCIAL (206-A-3)	—	SCHRAEDER 3250-AM-1/4 PT
2	2	32	PORCA GIRATÓRIA	COMERCIAL (101-H-18)	AÇO	RODOL Nº 740 8-8
1	1	31	MANGUEIRA FLEXÍVEL	COMERCIAL (AERQUIP)	BORRACHA	Nº 2555-10 22" COMPR.
1	1	30	MANGUEIRA FLEXÍVEL	COMERCIAL (AERQUIP)	BORRACHA	Nº 2556-10 20" COMPR.
6	6	29	PORCA DE COMPRES.	COMERCIAL (VCL-56)	LATÃO	1/2 T.
6	6	28	ANEL	COMERCIAL (VCL-06)	LATÃO	1/2 T.
2	2	27	COTOVELO DE COMPRES.	COMERCIAL (VCL-124)	LATÃO	1/2 NPTx 1/2 T.
26	26	26	TUBO	COMERCIAL BUNDY TUBING	—	1/2 COMP. CONF. NECES.
2	2	25	PORCA DE COMPRES.	COMERCIAL (VCL-01)	LATÃO	1/8 T.
2	2	24	ANEL	COMERCIAL (VCL-01)	LATÃO	1/8 T.
5	5	23	NIPLE	COMERCIAL (161-D-1)	F. GALV.	1/2 NPTx 1"
3	3	22	BUCHA DE REDUÇÃO	COMERCIAL (VCL-09)	LATÃO	1/4 NPTx 1/8 NPT
1	1	21	TEE DE REDUÇÃO	COMERCIAL (193-B-3)	F. GALV.	1/2 NPTx 1/4 NPT
4	4	20	PORCA SEXT.	COMERCIAL (176-A-4)	AÇO	1/4 NC
4	2	19	PARAF. CAB. SEXT.	COMERCIAL (170-C-10)	AÇO	1/4 NCx 2"
2	1	18	SUPORTE DOS CANOS	VV-5287	AÇO	—
1	—	17	CANO	COMERCIAL	F. GALV.	1/2 NPTx 81"
—	1	16	CANO	COMERCIAL	F. GALV.	1/2 NPTx 60"
1	—	15	CANO	COMERCIAL	F. GALV.	1/2 NPTx 85 1/2"
—	1	14	CANO	COMERCIAL	F. GALV.	1/2 NPTx 64 1/2"
1	—	13	CANO	COMERCIAL	F. GALV.	1/2 NPTx 84"
—	1	12	CANO	COMERCIAL	F. GALV.	1/2 NPTx 63"
3	3	11	PARAF. CAB. SEXT.	COMERCIAL (170-E-6)	AÇO	3/8 NCx 1"
1	1	10	NIPLE	COMERCIAL (161-F-5)	F. GALV.	1 NPTx 3"
3	3	9	COTOVELO 90°	COMERCIAL (127-B-5)	F. GALV.	1" NPT
1	1	8	VÁLVULA ESFÉRICA	COMERCIAL (161-D-3)	F. GALV.	1" NPT
2	2	7	NIPLE	COMERCIAL (161-D-3)	F. GALV.	1/2 NPTx 2"
1	1	6	SUPORTE	VV-2718	AÇO	—
—	—	5	VÁLVULA SOLENÓIDE	COMERCIAL (208-A-6)	—	SCHRAEDER-SB-645-4302-NA
4	4	4	NIPLE	COMERCIAL (161-D-4)	F. GALV.	1/2 NPTx 2 1/2"
15	15	3	COTOVELO 90°	COMERCIAL (127-B-3)	F. GALV.	1/2 NPT
3	3	2	UNIÃO	COMERCIAL (201-A-3)	F. GALV.	1/2 NPT
1	1	1	BUCHA DE REDUÇÃO	COMERCIAL (116-D-1)	F. GALV.	1 NPTx 1/2 NPT
QUANT.	POS.	DENOMINAÇÃO	PEÇA Nº	MATERIAL	OBS.	
2	1	GR. Nº	VIDROS VITON LTDA.	U.S. VER. DATA 18-05-93		
MAQUINA I.S. 6 SEÇÕES	MAQUINA I.S. 6 SEÇÕES	DESCR. DO GRUPO	MAQUINA I.S. 6 e 8 SEÇÕES ENCANAMENTO GERAL	U.S. DATA 18-05-93		
REDES. 18-05-93	REDES. 18-05-93	REDES. 18-05-93	ENCANAM. DE AR P/ INTERCEPTADOR DE GOTAS e CILINDRO RETRATOR	U.S. DATA 18-05-93		
ITEM	MODIFICAÇÕES	DATA	ITEM	MODIFICAÇÕES	DATA	
A	ACRESC. POS. 70	07.05.97				
ESCALA	1/4					