
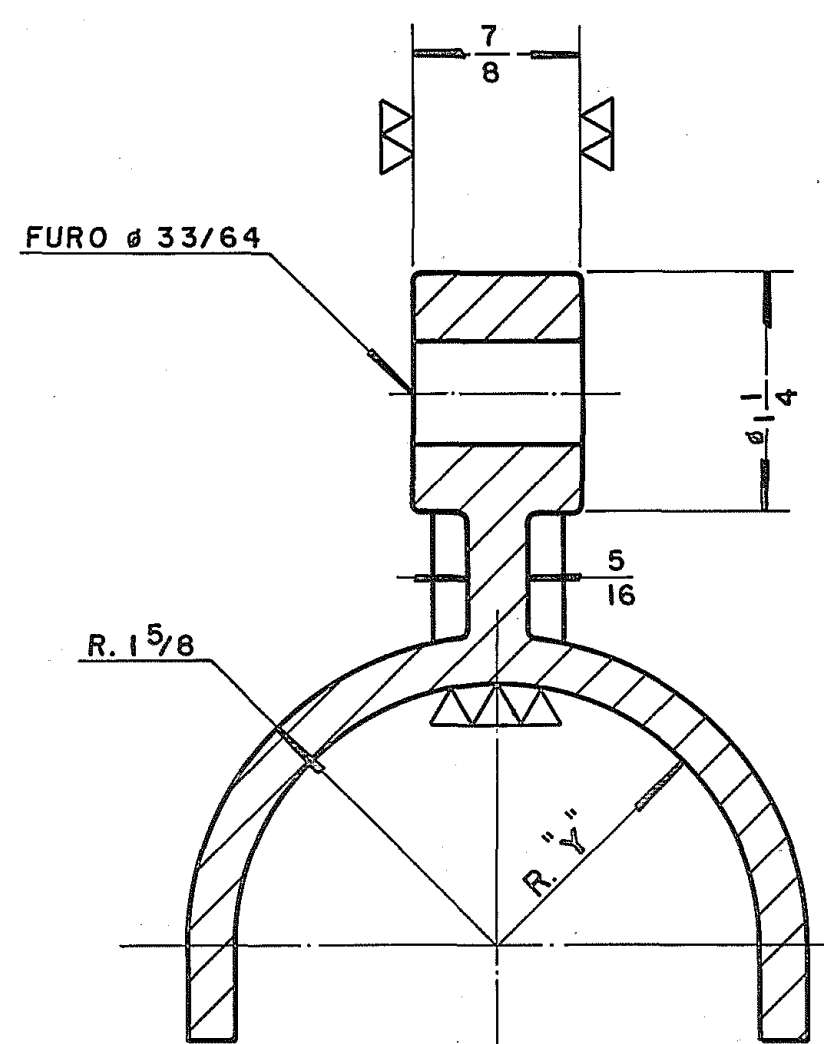


**ATENÇÃO!**  
MANTER ESTA ORELHA CONF AS DIMEN.  
INDICADAS, CORTAR FORA AS RESTANTES

ANTES DE FURAR ESMERILHAR  
ESTAS FACES ESQUADRANDO-AS  
MANTENDO A ESPESSURA DE 3/4


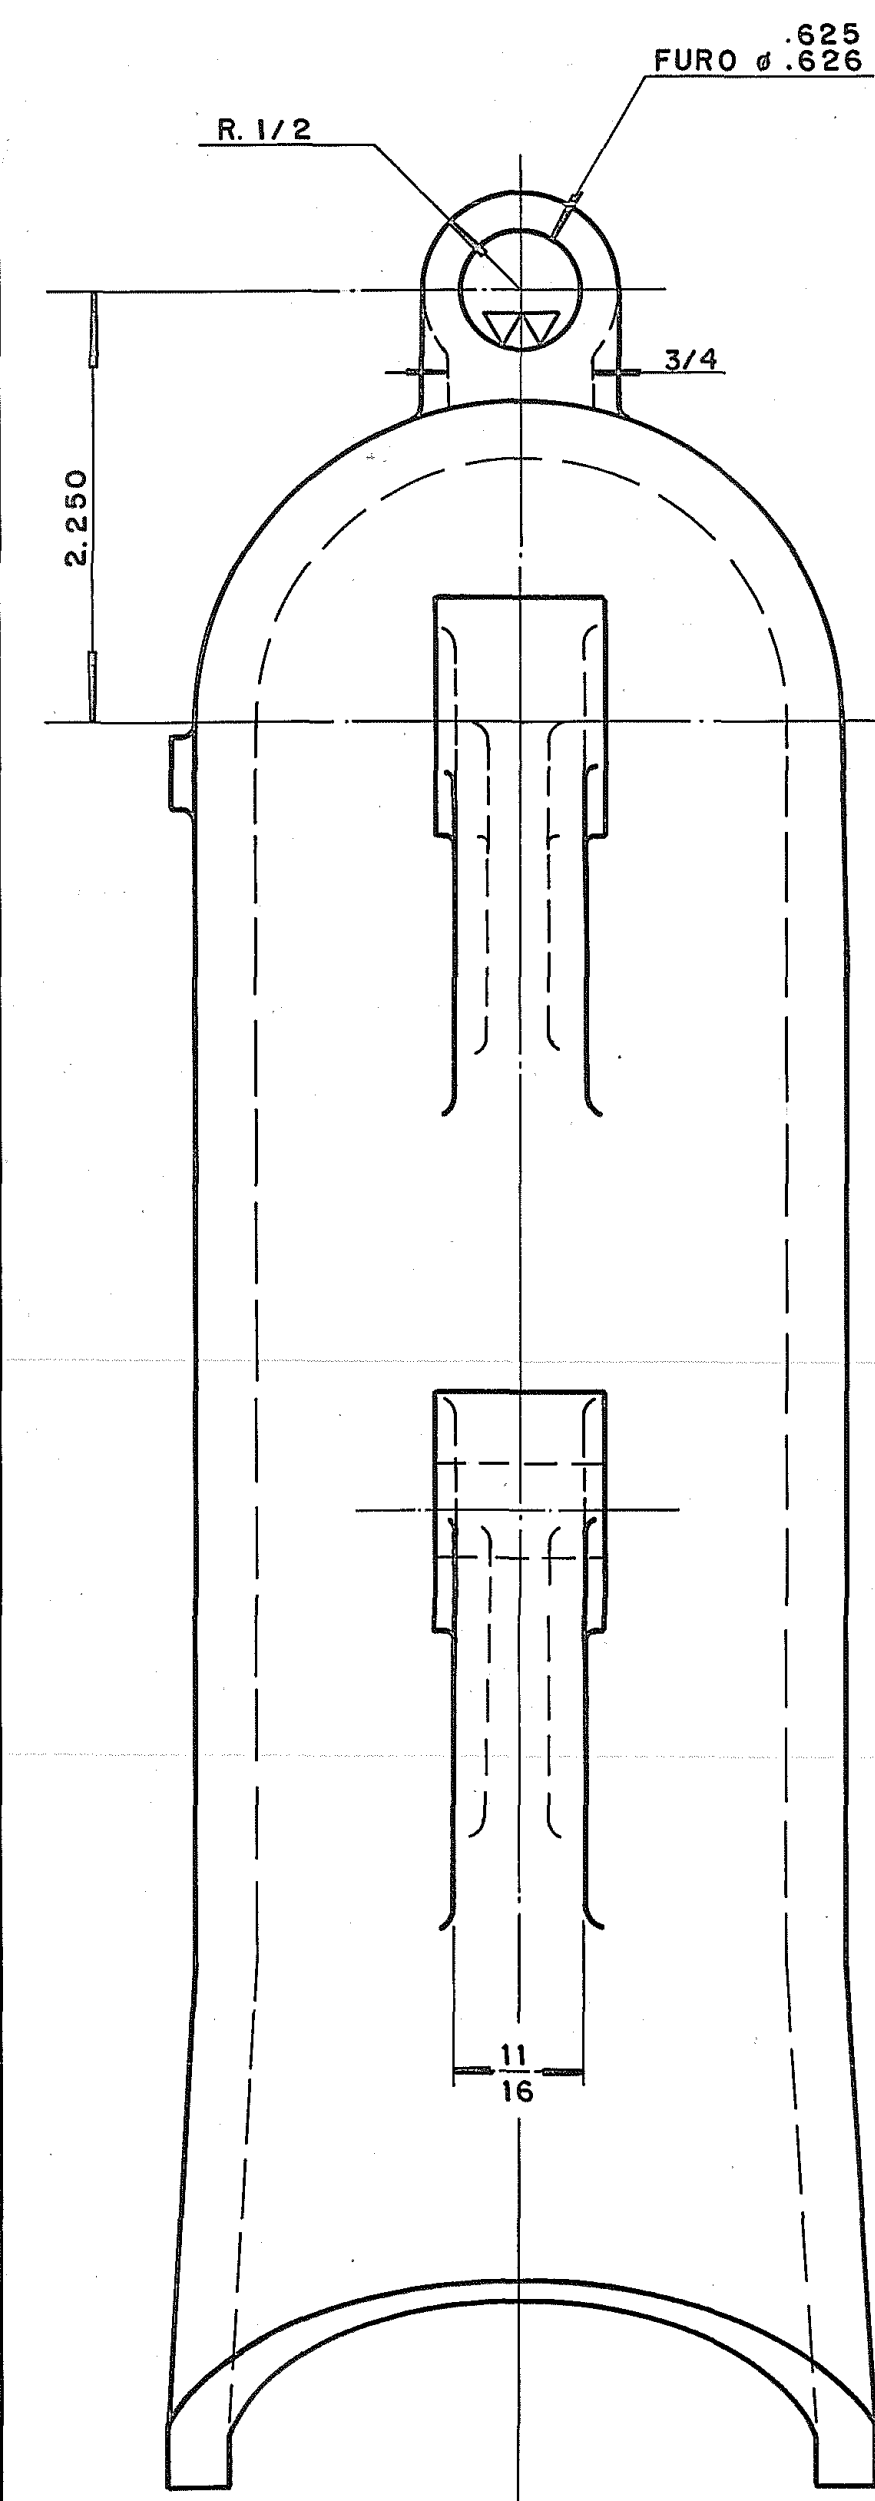


CORTE CC

PART Nº

8 SEC. MACH. SEC.

SIZE

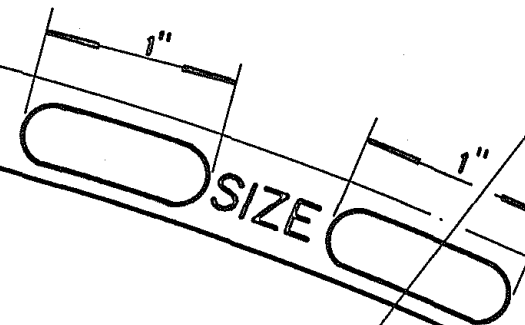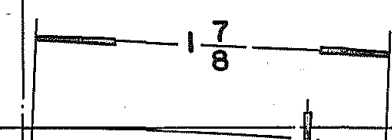

1 1/2

18"

2 4"

18 1/2

4 5/16

25°

Ø 1 1/4

35°

C

DIM. Z

15°

15°


2"

PARTE CONICA

30°

X

15 19/32

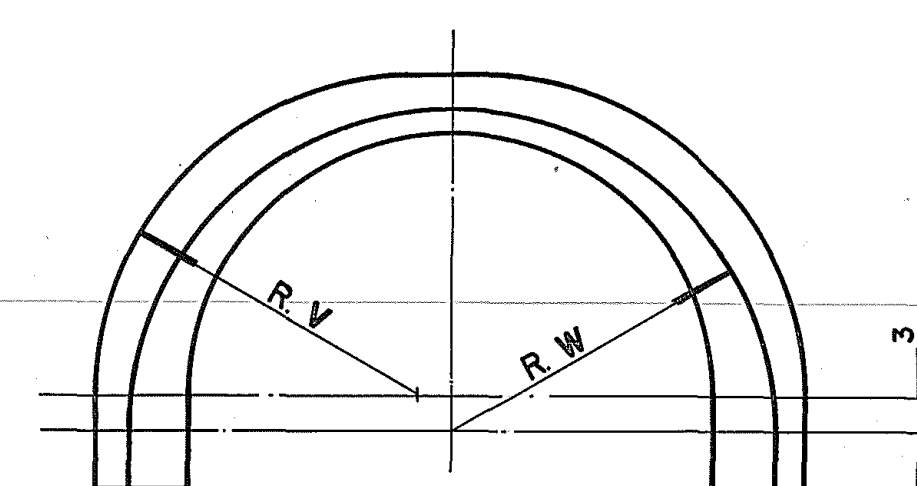

VISTO POR X

| PEÇA Nº | DIÂM. | RAIO V | RAIO W | RAIO Y | DIM. Z | USAR PEÇA EM BRUTO Nº |
|---------|-------|--------|--------|--------|--------|-----------------------|
| 23-6132 | 2 3/4 | 1 5/8  | 1 1/16 | 1 3/8  | 1.494  | VV-2995               |
| 23-6131 | 2 5/8 | 1 5/8  | 1 5/8  | 1 5/16 | 1.557  | VV-2996               |
| 23-6130 | 2 1/2 | 1 5/8  | 1 9/16 | 1 1/4  | 1.619  | VV-2997               |

|                                                                        |  |                                         |  |                         |
|------------------------------------------------------------------------|--|-----------------------------------------|--|-------------------------|
| DATA: 19-02-93                                                         |  | VIDROS VITON LTDA.                      |  | DES. <i>[Signature]</i> |
| TOLERANCIAS STANDARD PARA SUPERFICIES USINADAS SEM TOLERANCIA INDICADA |  | MAT. FERRO FUNDIDO CINZENTO GG-15       |  | APR. <i>[Signature]</i> |
| DECIMAL ± 0.05"                                                        |  | NOME DO CONJ. 8 SECT IN LINE IS MACHINE |  | Nº DO CONJ. 191-D-6646  |
| FRAÇÃO                                                                 |  | NOME DA PEÇA DEFLECTOR SEC. 2 & 7       |  | Nº DA VIDE TABELA       |
| DE 0" ATE 3" ± 1/64                                                    |  | TRAT.                                   |  | Nº DO DES.              |
| DE 3" ATE 24" ± 1/32                                                   |  | ACAB. DE 24" ± 1/16                     |  | ESCALA 1:1              |
| DE 24" ATE 48" ± 1/16                                                  |  |                                         |  |                         |