


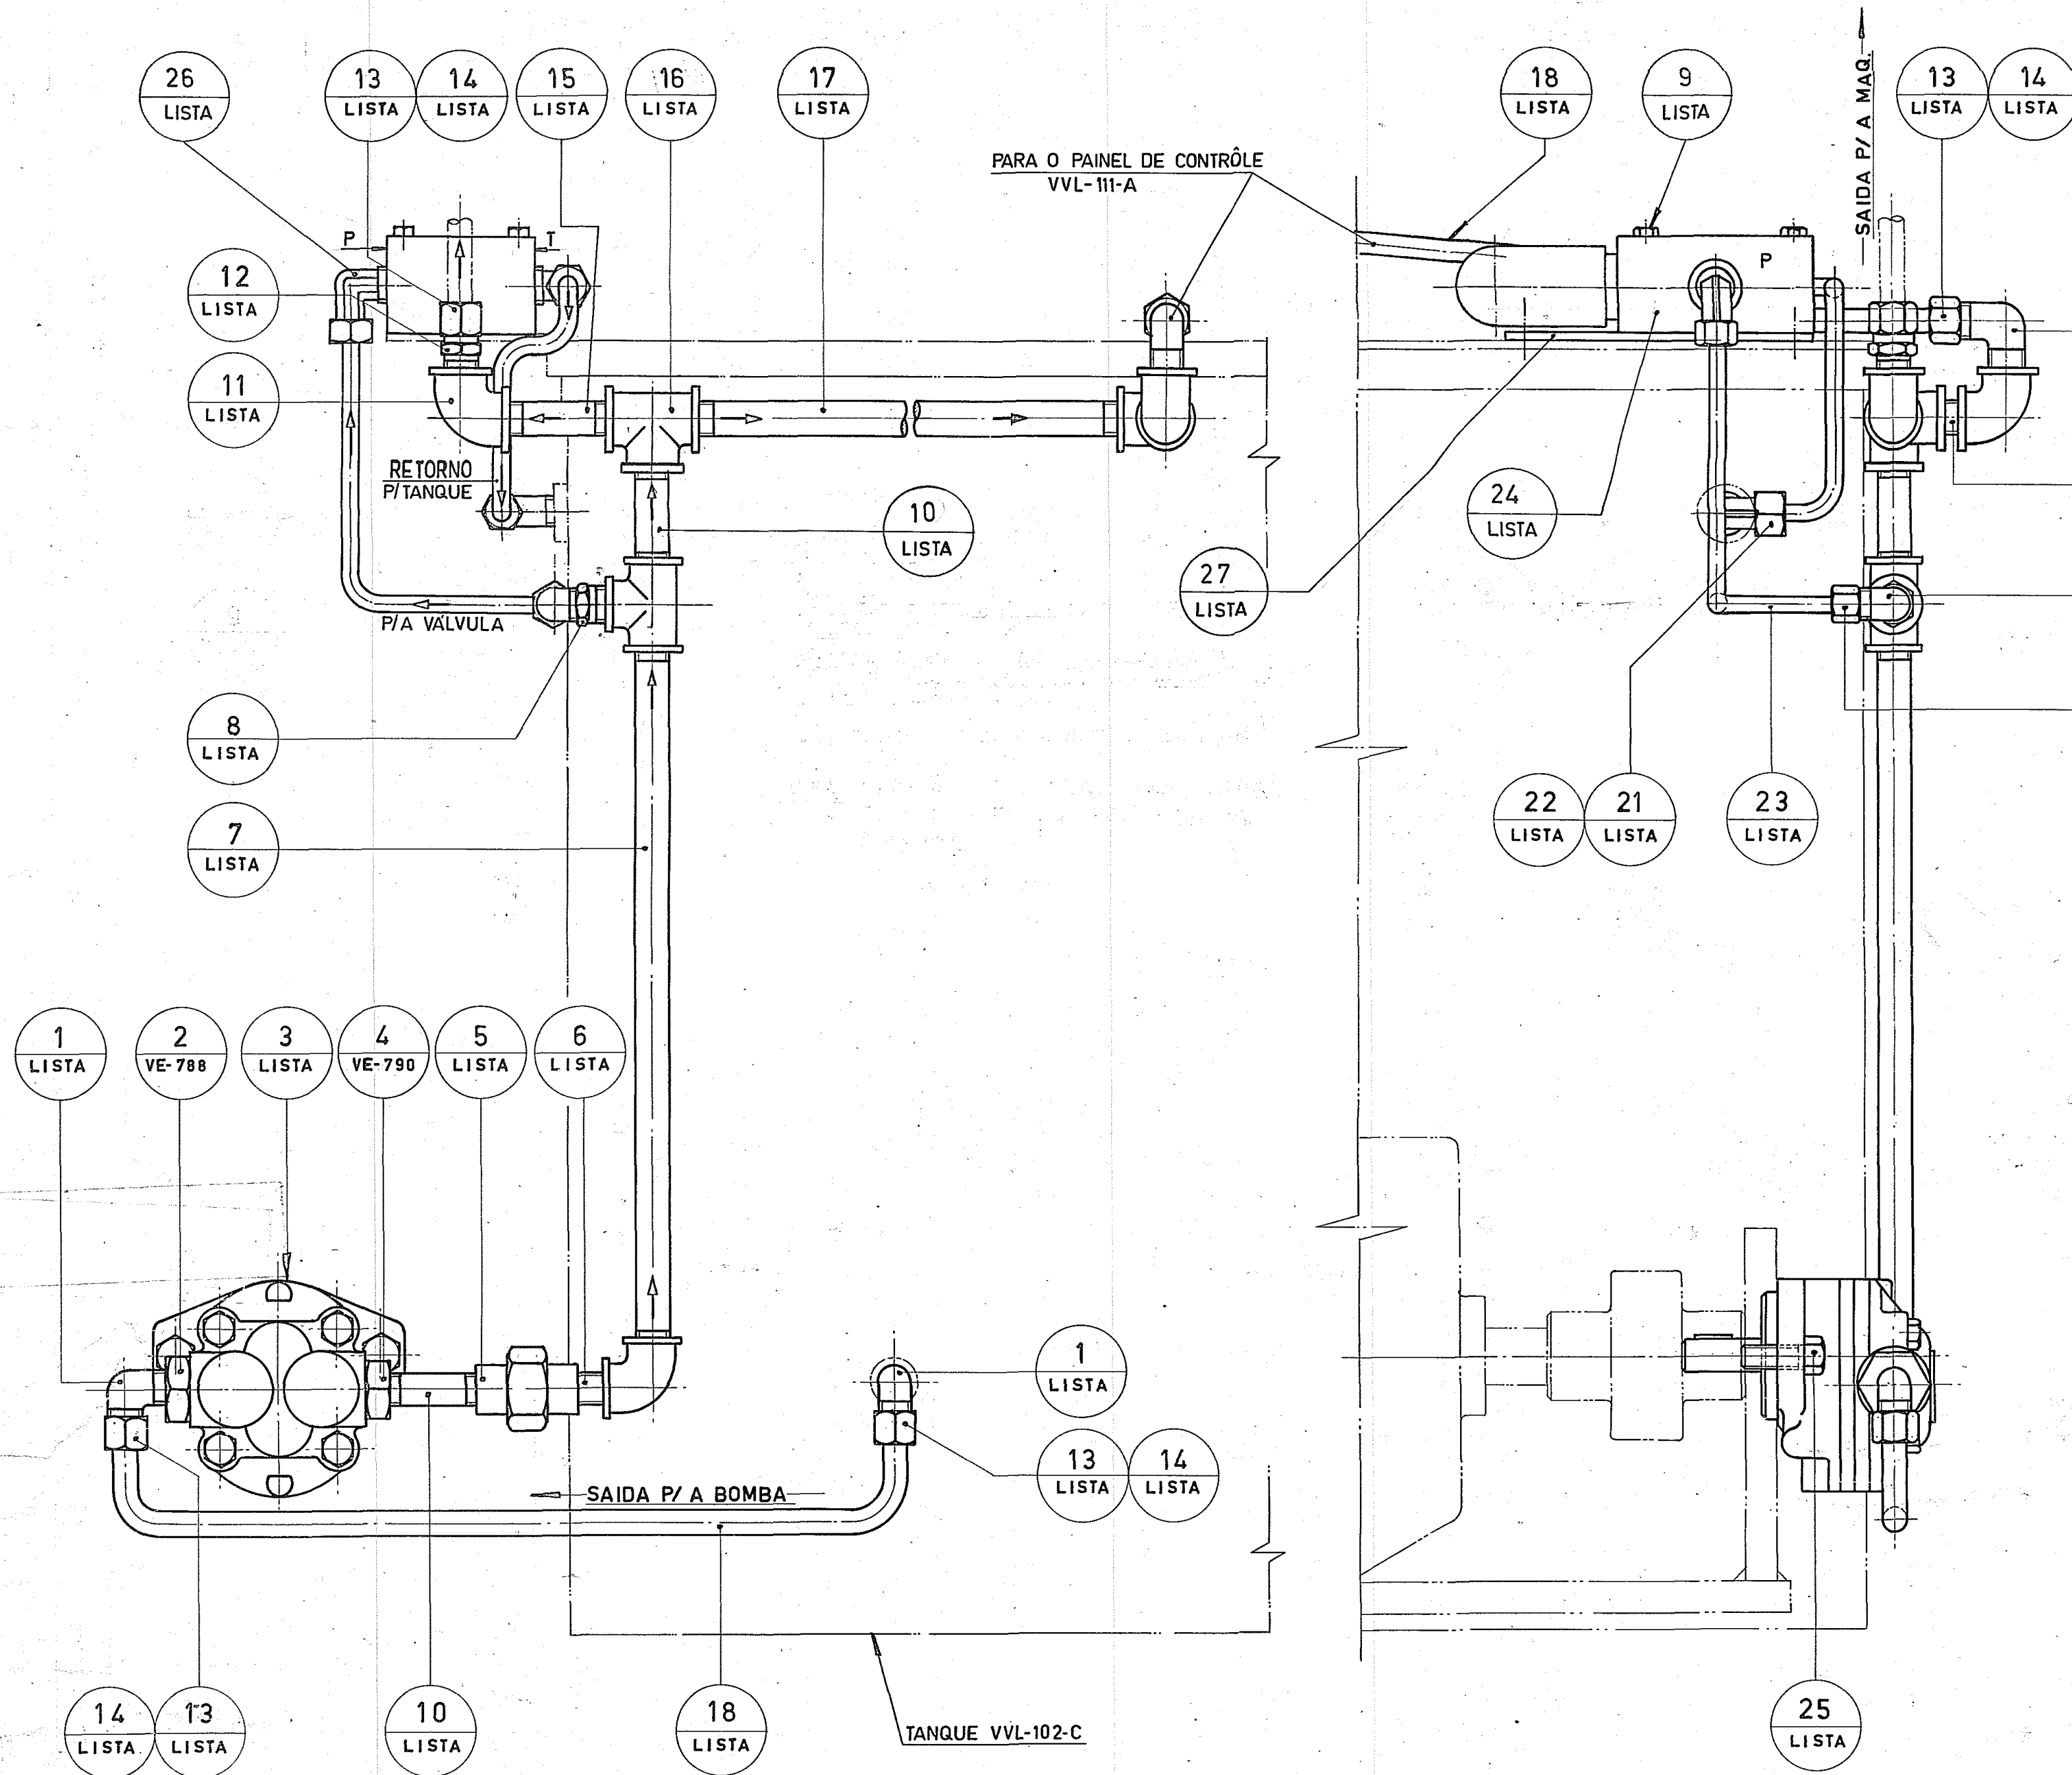

1	27	SUPORTE DA VÁLVULA	VE-1553	AÇO	
2	26	COT. DE COMP. 1/4 NPT x 1/4 TUBO	COMERCIAL	LATÃO	VCL-29
2	25	PARAF. CAB. SEXT.	COMERCIAL	AÇO	3/8 NC x 7/8
1	24	VÁLVULA REXROTH DBDS 6G-13/200	COMERCIAL		
1	23	TUBO 1/4	COMERCIAL	COBRE	1/4 x
4	22	ANEL	COMERCIAL	LATÃO	VCL-04
4	21	PORCA DE COMPR. 1/4	COMERCIAL	LATÃO	VCL-53
2	20	COTOV. DE COMPR. 1/8 NPT x 1/4 TUBO	COMERCIAL	LATÃO	VCL-25
1	19	NIPLE 1/4 NPT	COMERCIAL	F. GALV.	1/4 NPT x 3/4
1	18	TUBO 3/8	COMERCIAL	COBRE	3/8
1	17	TUBO 1/4	COMERCIAL	F. GALV.	1/4 x
2	16	TEE 1/4 NPT	COMERCIAL	F. GALV.	1/4 NPT
1	15	NIPLE 1/4 NPT	COMERCIAL	F. GALV.	1/4 NPT x 1/2
4	14	ANEL	COMERCIAL	LATÃO	VCL-05
4	13	PORCA DE COMPR. 3/8	COMERCIAL	LATÃO	VCL-54
1	12	UNIÃO DE COMPRESSÃO 1/4 NPT x 3/8 TUBO	COMERCIAL	LATÃO	VCL-105
4	11	COTOVELO 90°- 1/4 NPT	COMERCIAL	F. GALV.	1/4 NPT
2	10	NIPLE 1/4 NPT	COMERCIAL	F. GALV.	1/4 NPT x 2"
4	9	PARAF. C/CAB. SEXT.	COMERCIAL	AÇO	1/4 NC x 3/4
1	8	BUCHA DE RED. 1/4 NPT x 1/8 NPT	COMERCIAL	LATÃO	VCL-09
1	7	TUBO 1/4	COMERCIAL	F. GALV.	1/4 x 11"
1	6	NIPLE 1/4 NPT	COMERCIAL	F. GALV.	1/4 NPT x 1"
1	5	UNIÃO 1/4 NPT	COMERCIAL	F. GALV.	1/4 NPT
1	4	BUCHA DE RED. 3/4 SAE / 1/4 NPT	VE-790	AÇO	
1	3	BOMBA DE TRANSF.	COMERCIAL (PARKER)		MODELO D-05-AA-1A
1	2	BUCHA DE RED. 7/8 SAE / 1/4 NPT	VE-788	AÇO	
3	1	COTOV. DE COMPR. 1/4 NPT x 3/8 TUBO	COMERCIAL	LATÃO	VCL-33
QTD.	POS.	DENOMINAÇÃO	PEÇA Nº	MATERIAL	OBS.
1	GR. Nº				
DESCRIÇÃO DO GRUPO					
DATA					

27-08-75

Des. *[assinatura]*

Escala *[assinatura]*

Pop. *[assinatura]*

Ver. *[assinatura]*

Subst. *[assinatura]*

1/2

MÁQUINA I.S. LUBRIFICAÇÃO AUTOM. ENCANAMENTO DO TANQUE DE ÓLEO C/ BOMBA PARKER

VVL-102-C-45

N.º do Desenho