


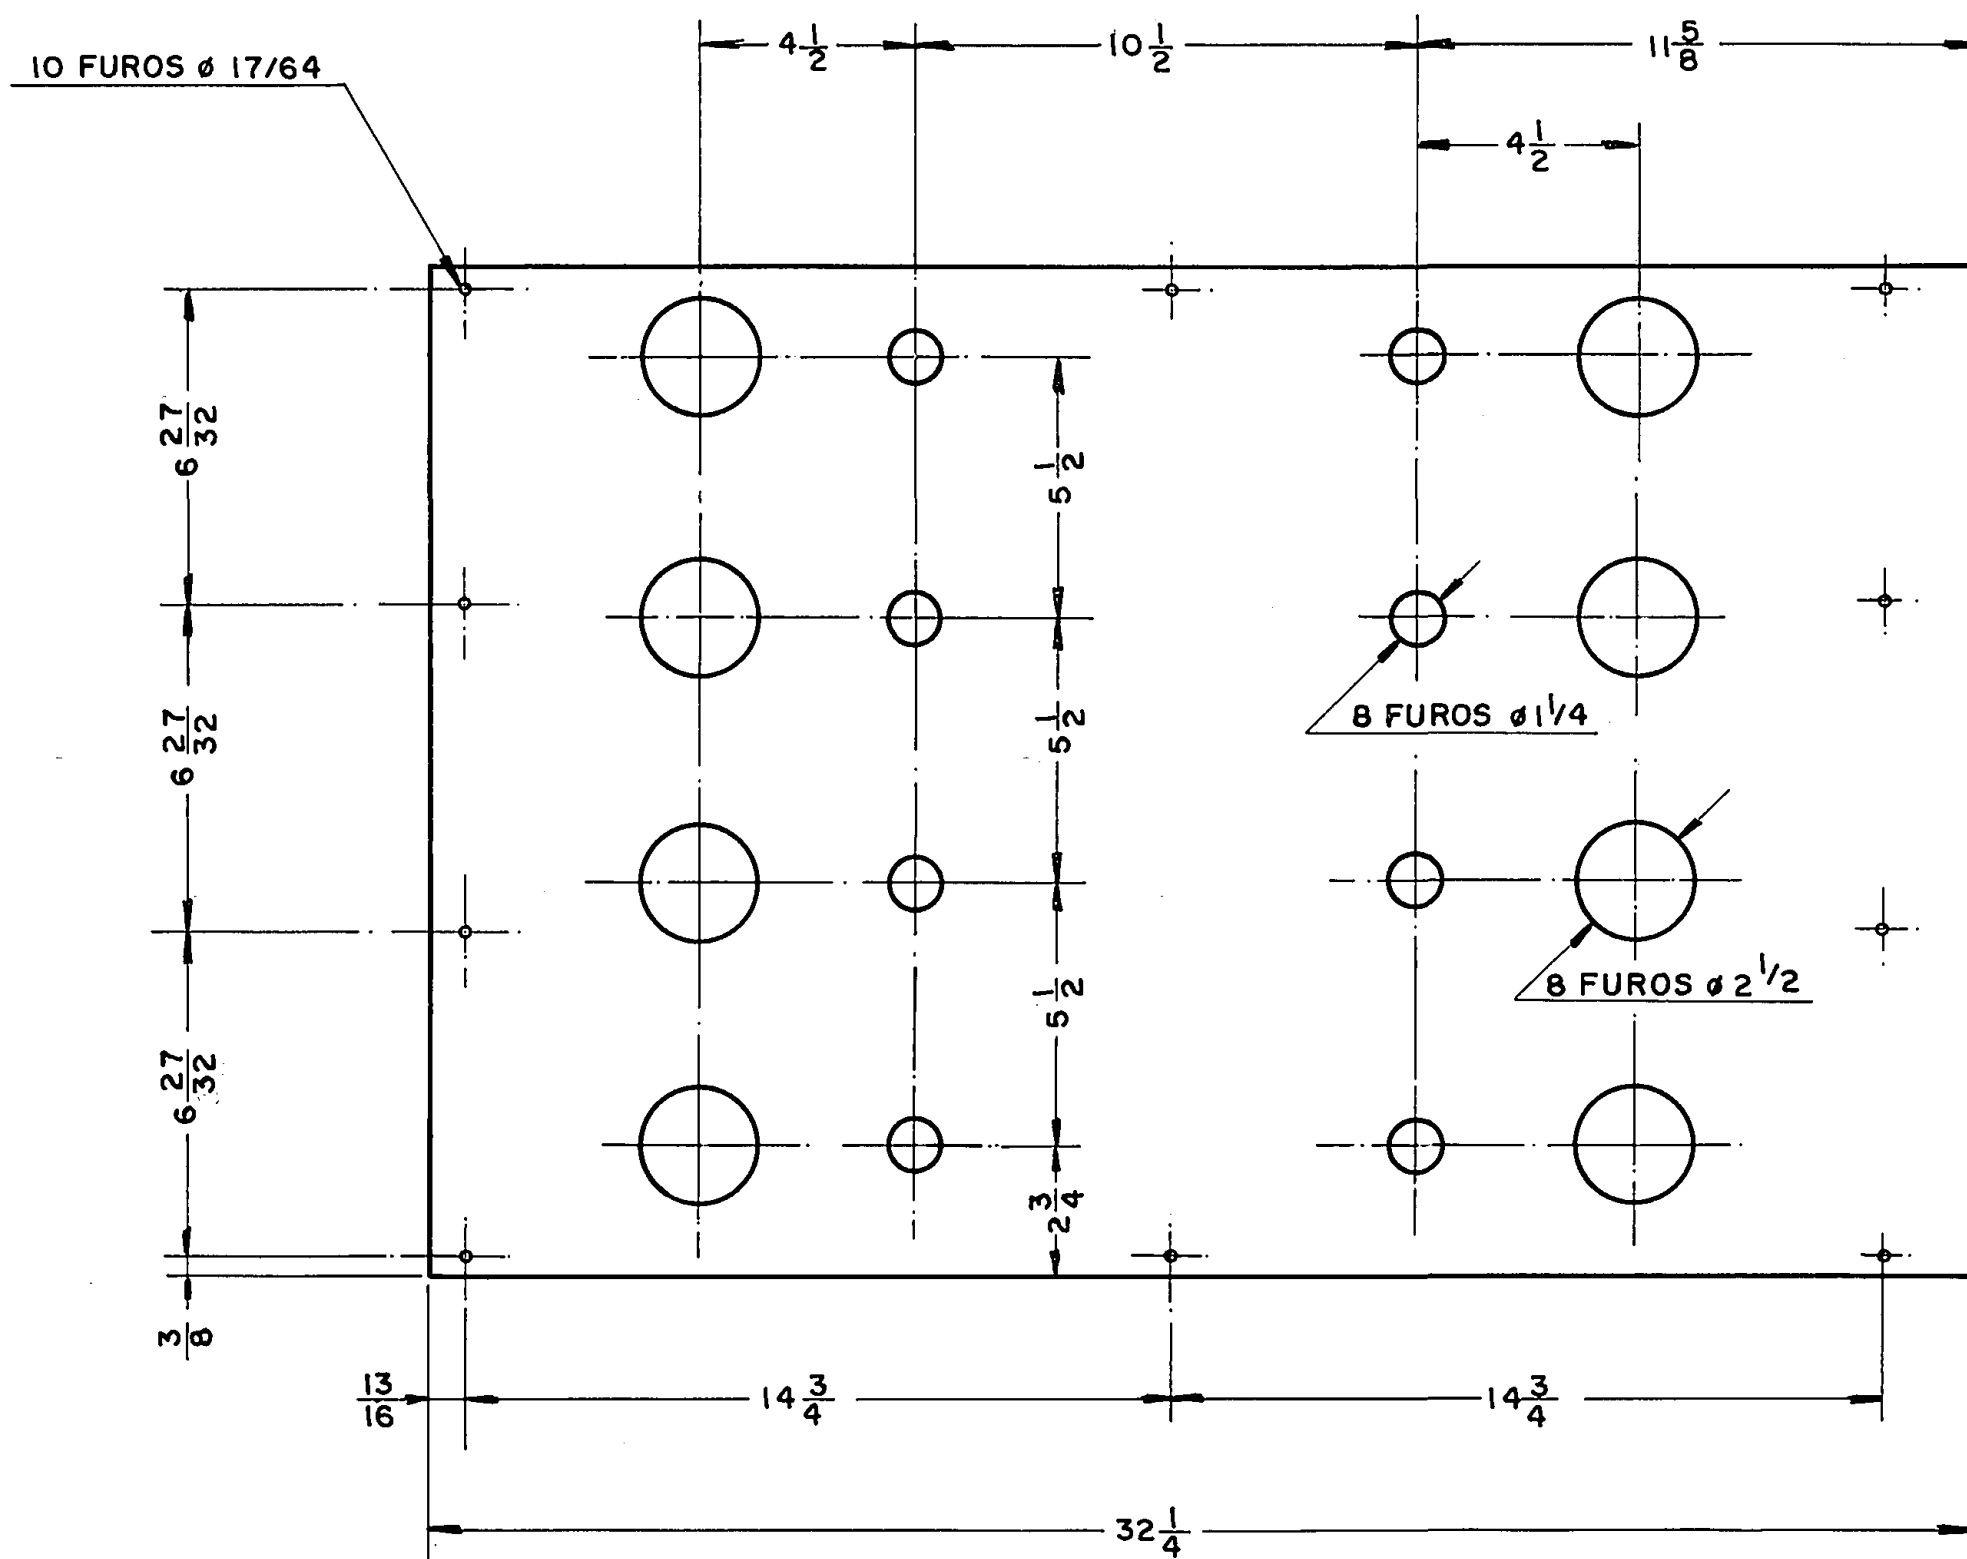

DATA: 24 - 08 - 93	VIDROS VITON LTDA.	SS. <i>M. B. B.</i>
TOLERANCIAS STANDARD PARA SUPERFICIES USINADAS SEM TOLERANCIA INDICADA	MAT. CHAPA DE AÇO SAE 1020 - 1/8	APPROV.
DECIMAL $\pm$ 0.05"	NOME DO CONJ. ESTRUTURA DO PAINEL	N.º DO CONJ. VVM-576
FRAÇÃO	NOME DA PEÇA TAMPA FRONTAL	N.º DA PEÇA VVM-576-7
DE 0" ATÉ 5" $\pm$ 1/64	TRAT. TERM.	N.º DO DTS.
DE 5" ATÉ 24" $\pm$ 1/32	ESCALA 1/4	
ACIMA DE 24" $\pm$ 1/16		